

EMPLACEMENT BOITE
EN ATTENTE DANS COMBLES
A DEFINIR AVANT POSE

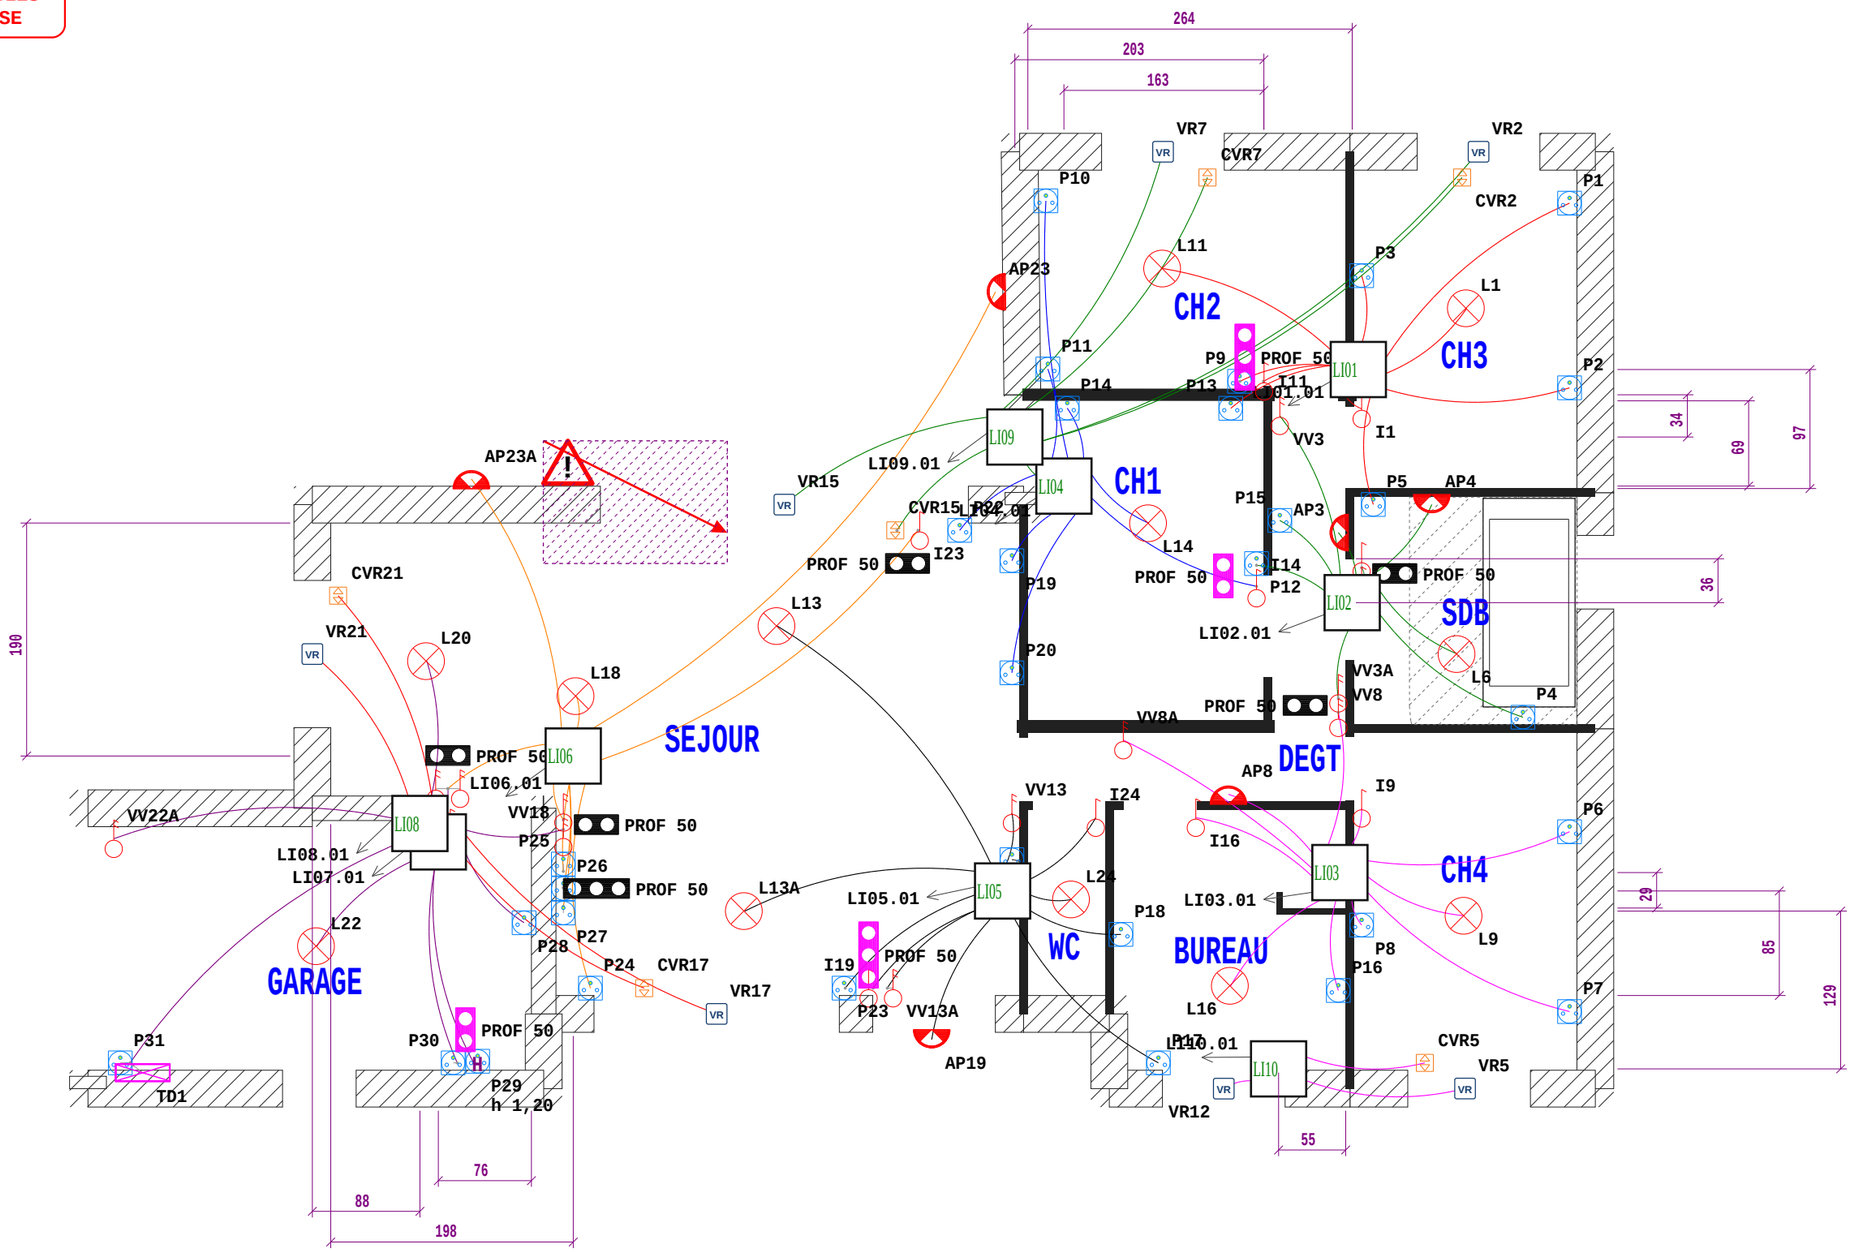

KiTēOHM pour une maison branchée	www.kiteohm.fr	Client	*Maisons CPR*
		Chantier	*MAILLARD AF544567*
		N°	

Echelle : *1 / 50*
Dess :
Date: *03/11/2026*

Les appareillages sont positionnés sur le plan à titre indicatif, ils doivent être installés en fonction des normes en vigueur.
Les hauteurs en cm sont données à titre indicatif, suivre les valeurs indiquées sur le plan .
⚠ Les hauteurs sont données à partir du sol fini ! ⚠

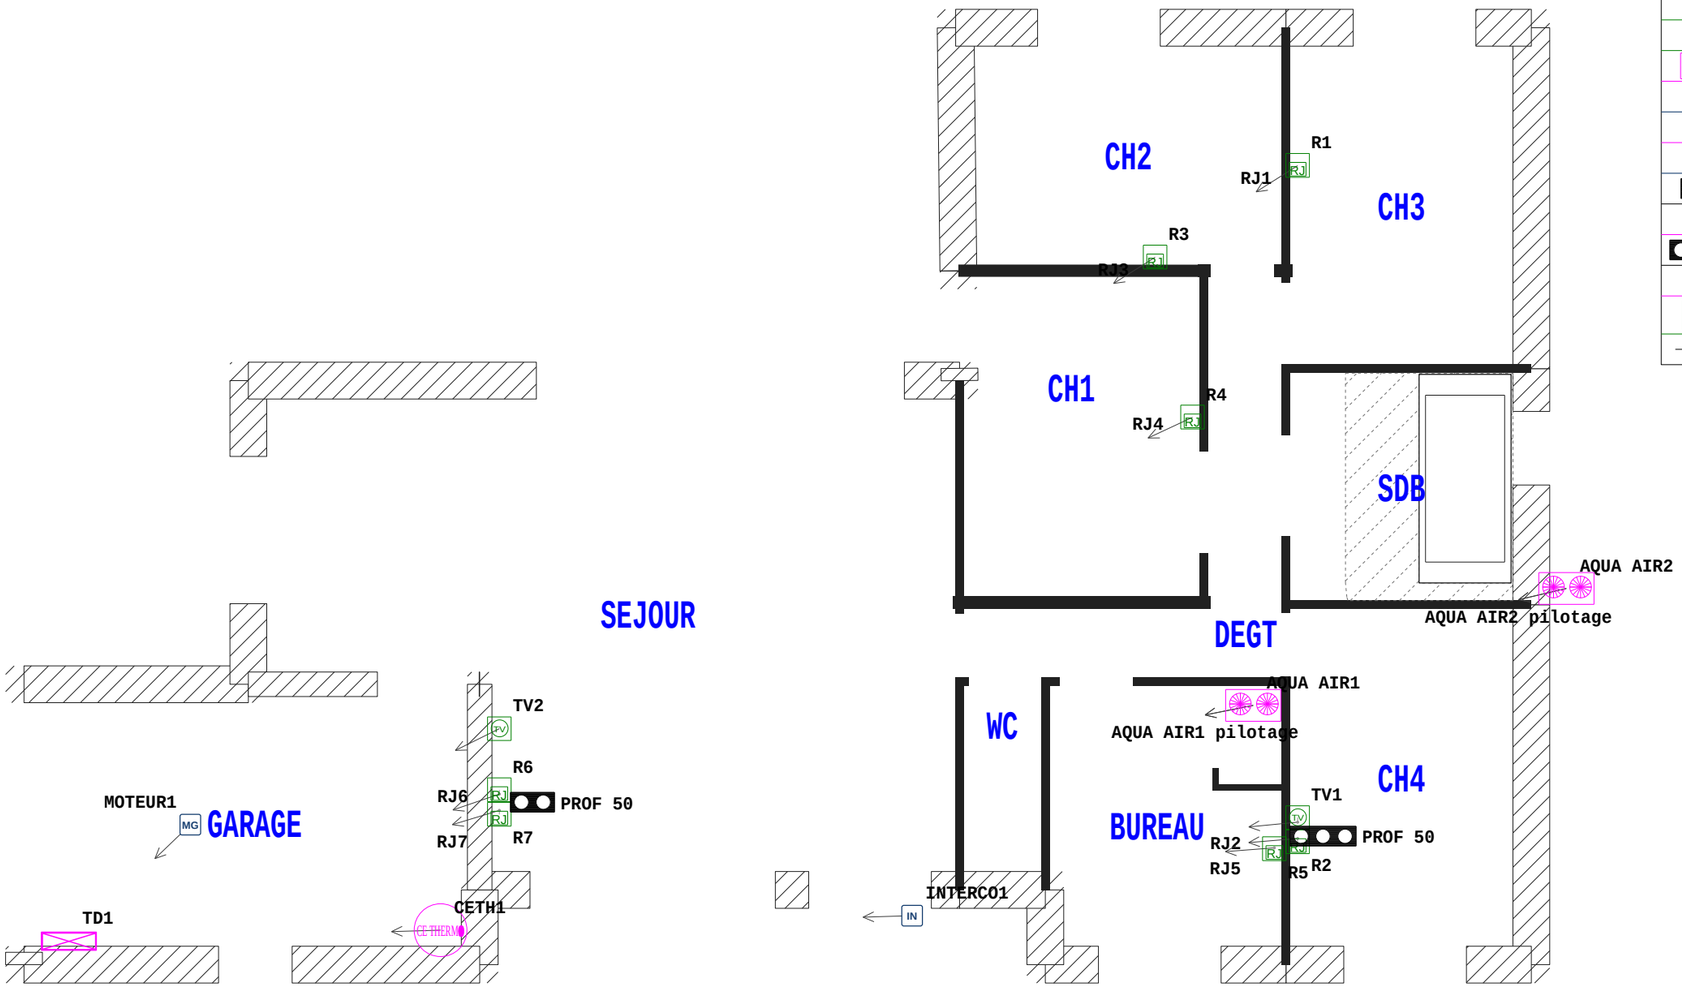

	Prise de courant H0.30m (PMR H0.40m)
	Point lumineux
	Interrupteur simple allumage
VR	Volet roulant (moteur)
	Interrupteur volet roulant connecté
	Applique étanche
	Interrupteur Va-et-Vient
	Prise de courant H1.20m
	Tableau d'alimentation générale basse tension
RJ	Prise RJ45 H0.30m (PMR H0.40m)
TV	Prise télévision H0.30m (PMR H0.40m)
	Pompe à chaleur unité extérieur
IN	Interphone
	Chauffe-eau électrique thermodynamique
MG	Moteur de garage
	Plaque double Horizontale
	Plaque double Verticale
	Plaque triple Horizontale
	Plaque triple Verticale
LI	Boîte de dérivation (pieuvre)
	Départ vers le tableau (boîte, ligne directe)

KiTēOHM pour une maison branchée

www.kiteohm.fr

Client	*Maisons CPR*	Echelle :	*1 / 50*
Chantier	*MAILLARD AF544567*	Dess :	
N°		Date:	*03/11/2026*

Les appareillages sont positionnés sur le plan à titre indicatif, ils doivent être installés en fonction des normes en vigueur.
Les hauteurs en cm sont données à titre indicatif, suivre les valeurs indiquées sur le plan .
⚠ Les hauteurs sont données à partir du sol fini ! ⚠