
	Boite pavillonnaire
DUO	Interrupteur double allumage
DUO	Interrupteur double Va-et-Vient
	Interrupteur simple allumage
	Interrupteur simple allumage lumineux
	Interrupteur Va-et-Vient
	Plaque double Horizontale
	Plaque double Verticale
	Plaque triple Horizontale
	Applique étanche
IP44	Applique murale salle de bain
	Douille chantier + coiffe
	Point lumineux
	Prise de courant 2.5² H0.30m (PMR H0.40m)
	Prise de courant 2.5² H1.20m
	Prise de courant Hotte
	Bouton saillie pour carillon filaire
	Carillon filaire
	Renvoi de tableau
	Liaison équipotentielle

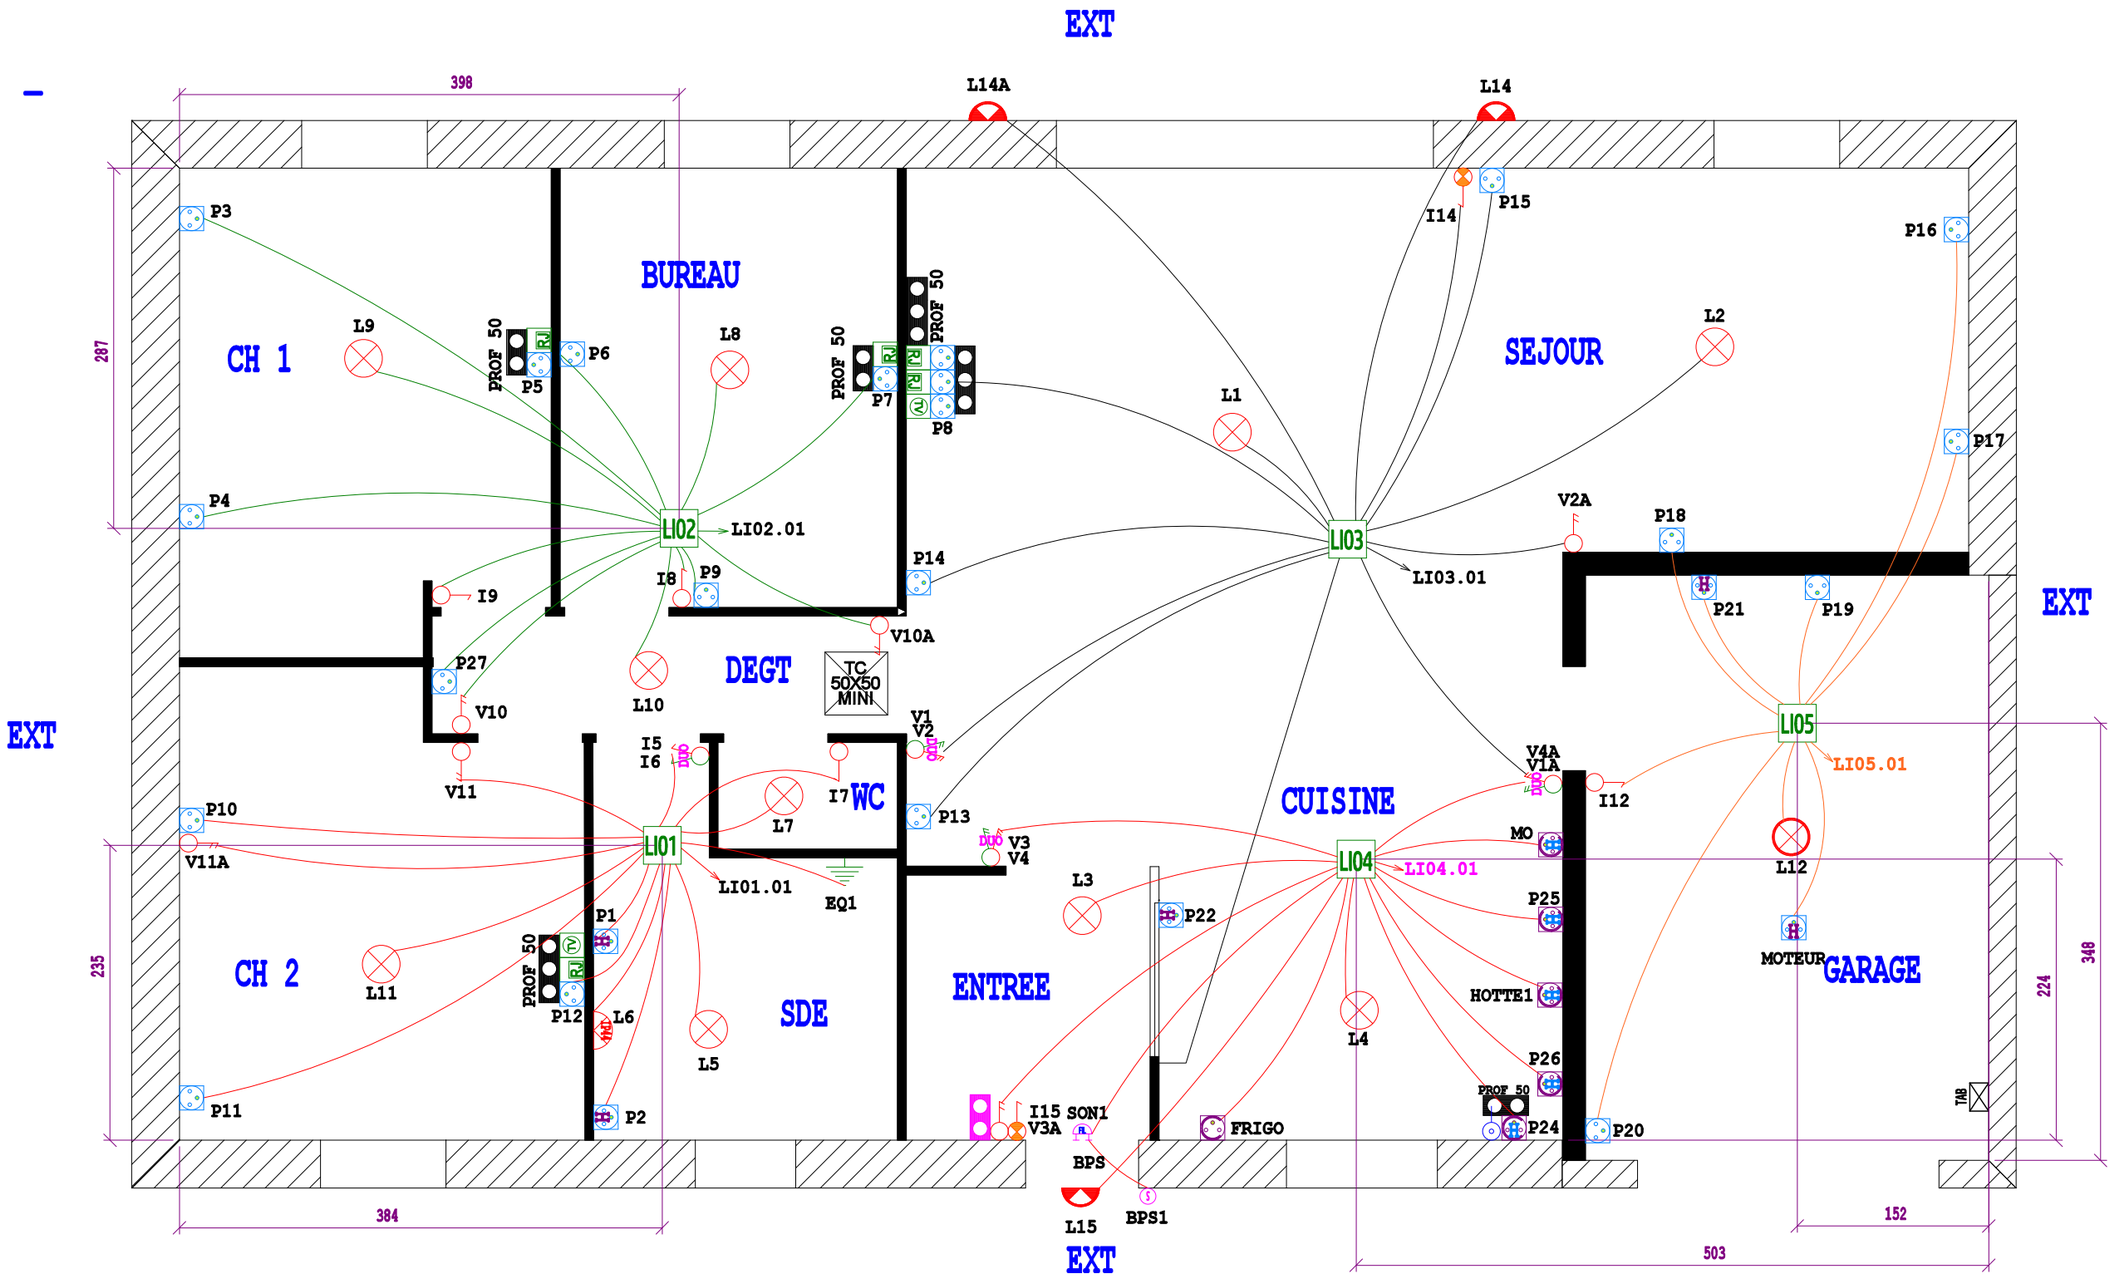


KiTēOHM pour une maison branchée	www.kiteohm.fr	Client	JOYEUX CONSTRUCTIONS
		Chantier	PASQUIER BLIN
		N°	AF26064553

Echelle : 1 / 50
Dess : ACR
Date : 16/09/2026

Les appareillages sont positionnés sur le plan à titre indicatif, ils doivent être installés en fonction des normes en vigueur.
Les hauteurs en cm sont données à titre indicatif, suivre les valeurs indiquées sur le plan .
⚠ Les hauteurs sont données à partir du sol fini ! ⚠

	Boite pavillonnaire
VR	Boite encastrée simple 50
CE SPLIT	Chauffe-eau électrique split
CLIM	Climatisation
750 W	Convecteur de chauffage rayonnant
	Pompe à chaleur unité extérieur
ALIM SEUL	Sèche serviette
HUB	Thermostat
ATTENTE TV EN COMBLE	Antenne TV H comble
RJ	Prise RJ45 H0.30m (PMR H0.40m)
TV	Prise télévision H0.30m (PMR H0.40m)
32A	Sortie de cable 32A
	Détecteur de fumée
	Commande VMC
	Prise de courant H1.20m
SPE	Prise de courant spécialisée H0.30m (PMR H0.40m)
	Tableau d'alimentation générale basse tension
	Tableau de communication
	Prise de terre

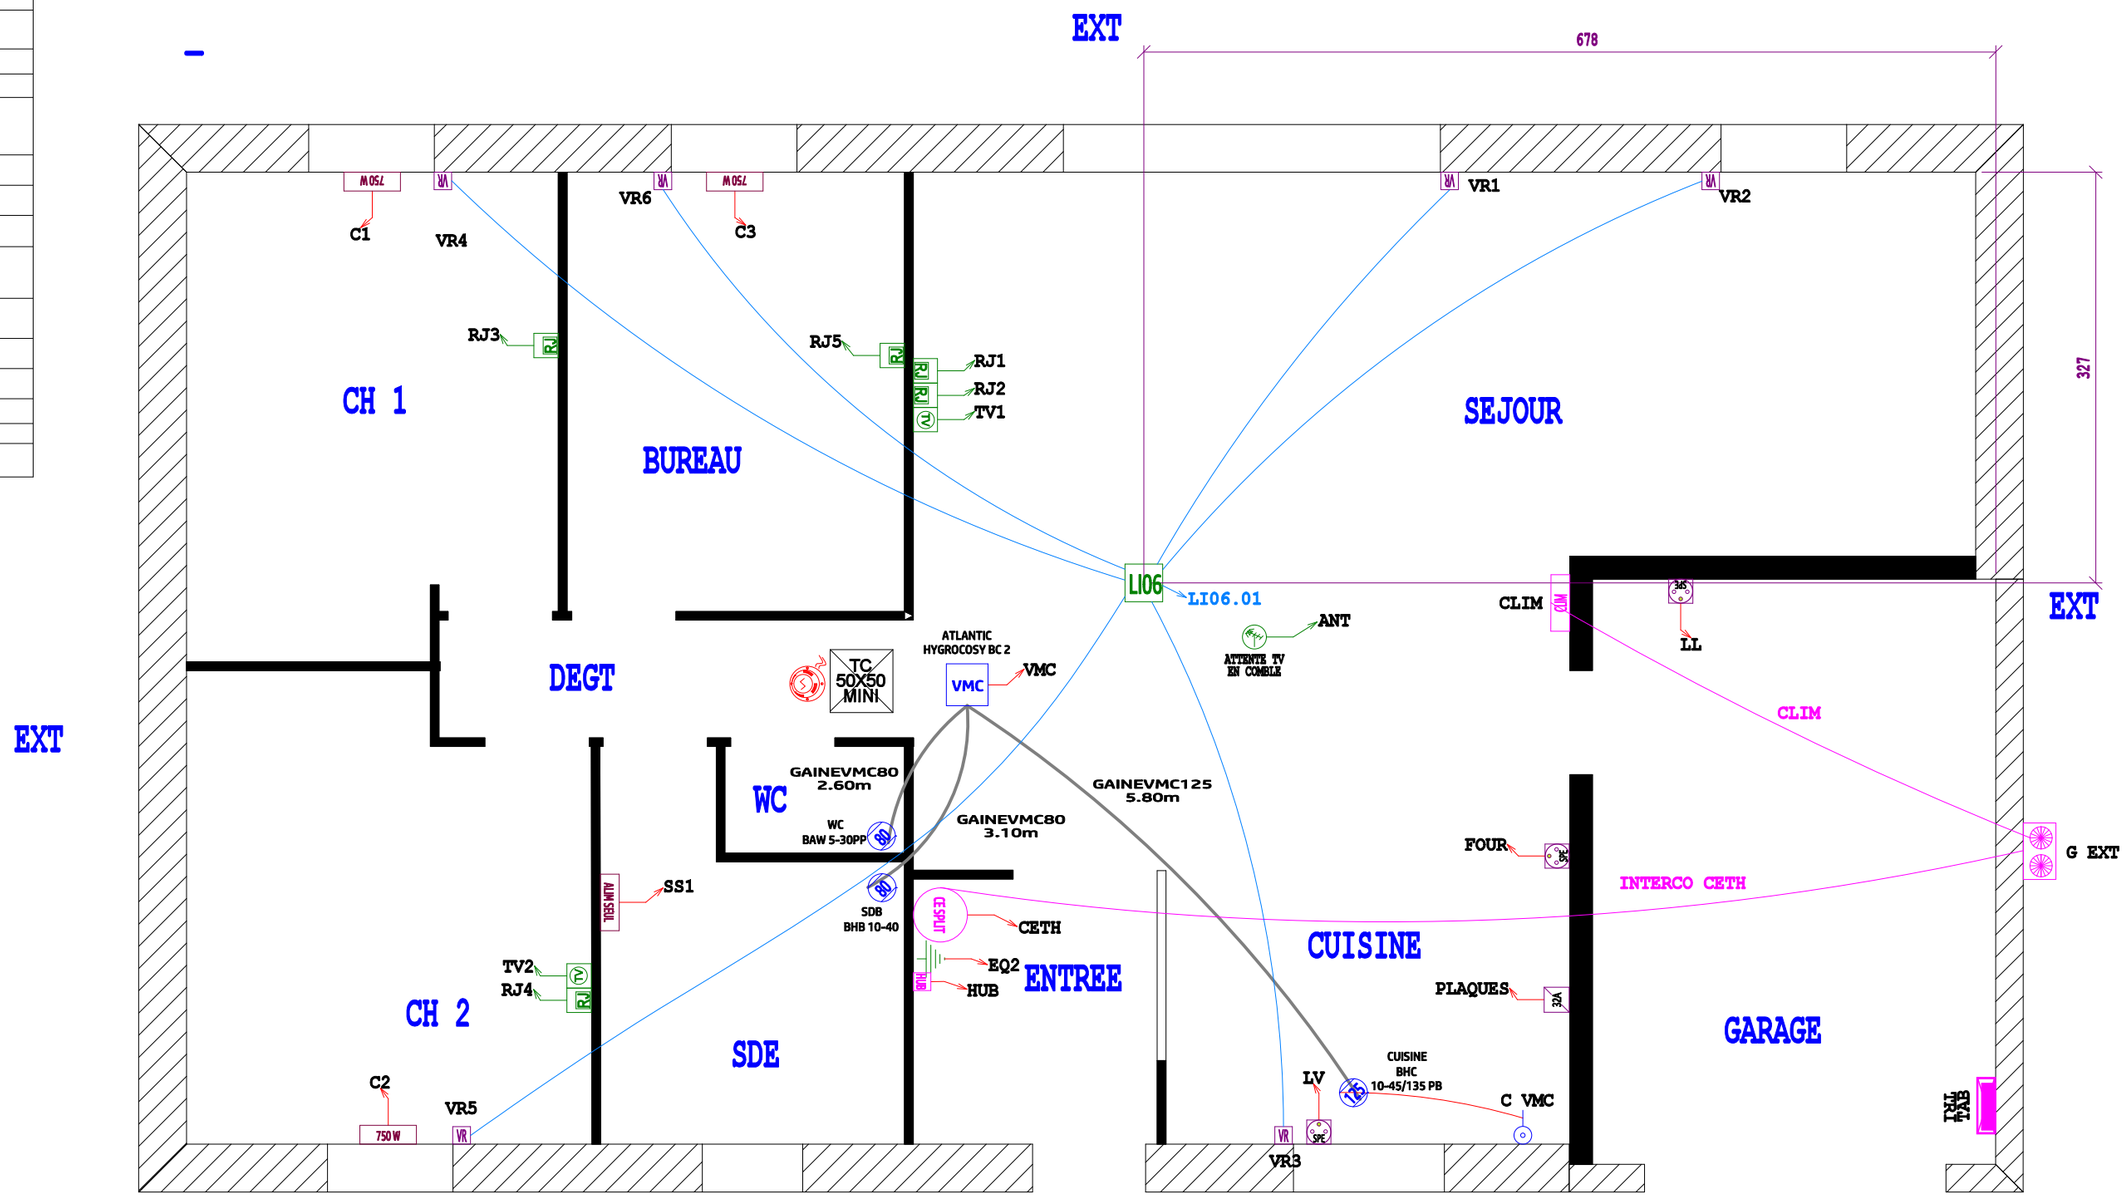


SUPPORT 4 CONNECTEURS RJ45 LEGRAND | -GTL TAB +GOULOTTE TAB | SUPPORT TAB NON ISOLEE | BOUCHONS GAINES 16/20/25

KiTēOHM pour une maison branchée

www.kiteohm.fr

Client	JOYEUX CONSTRUCTIONS	Echelle :	1 / 50
Chantier	PASQUIER BLIN	Dess :	ACR
N°	AF26064553	Date:	16/09/2026

Les appareillages sont positionnés sur le plan à titre indicatif, ils doivent être installés en fonction des normes en vigueur.
Les hauteurs en cm sont données à titre indicatif, suivre les valeurs indiquées sur le plan .
⚠ Les hauteurs sont données à partir du sol fini ! ⚠

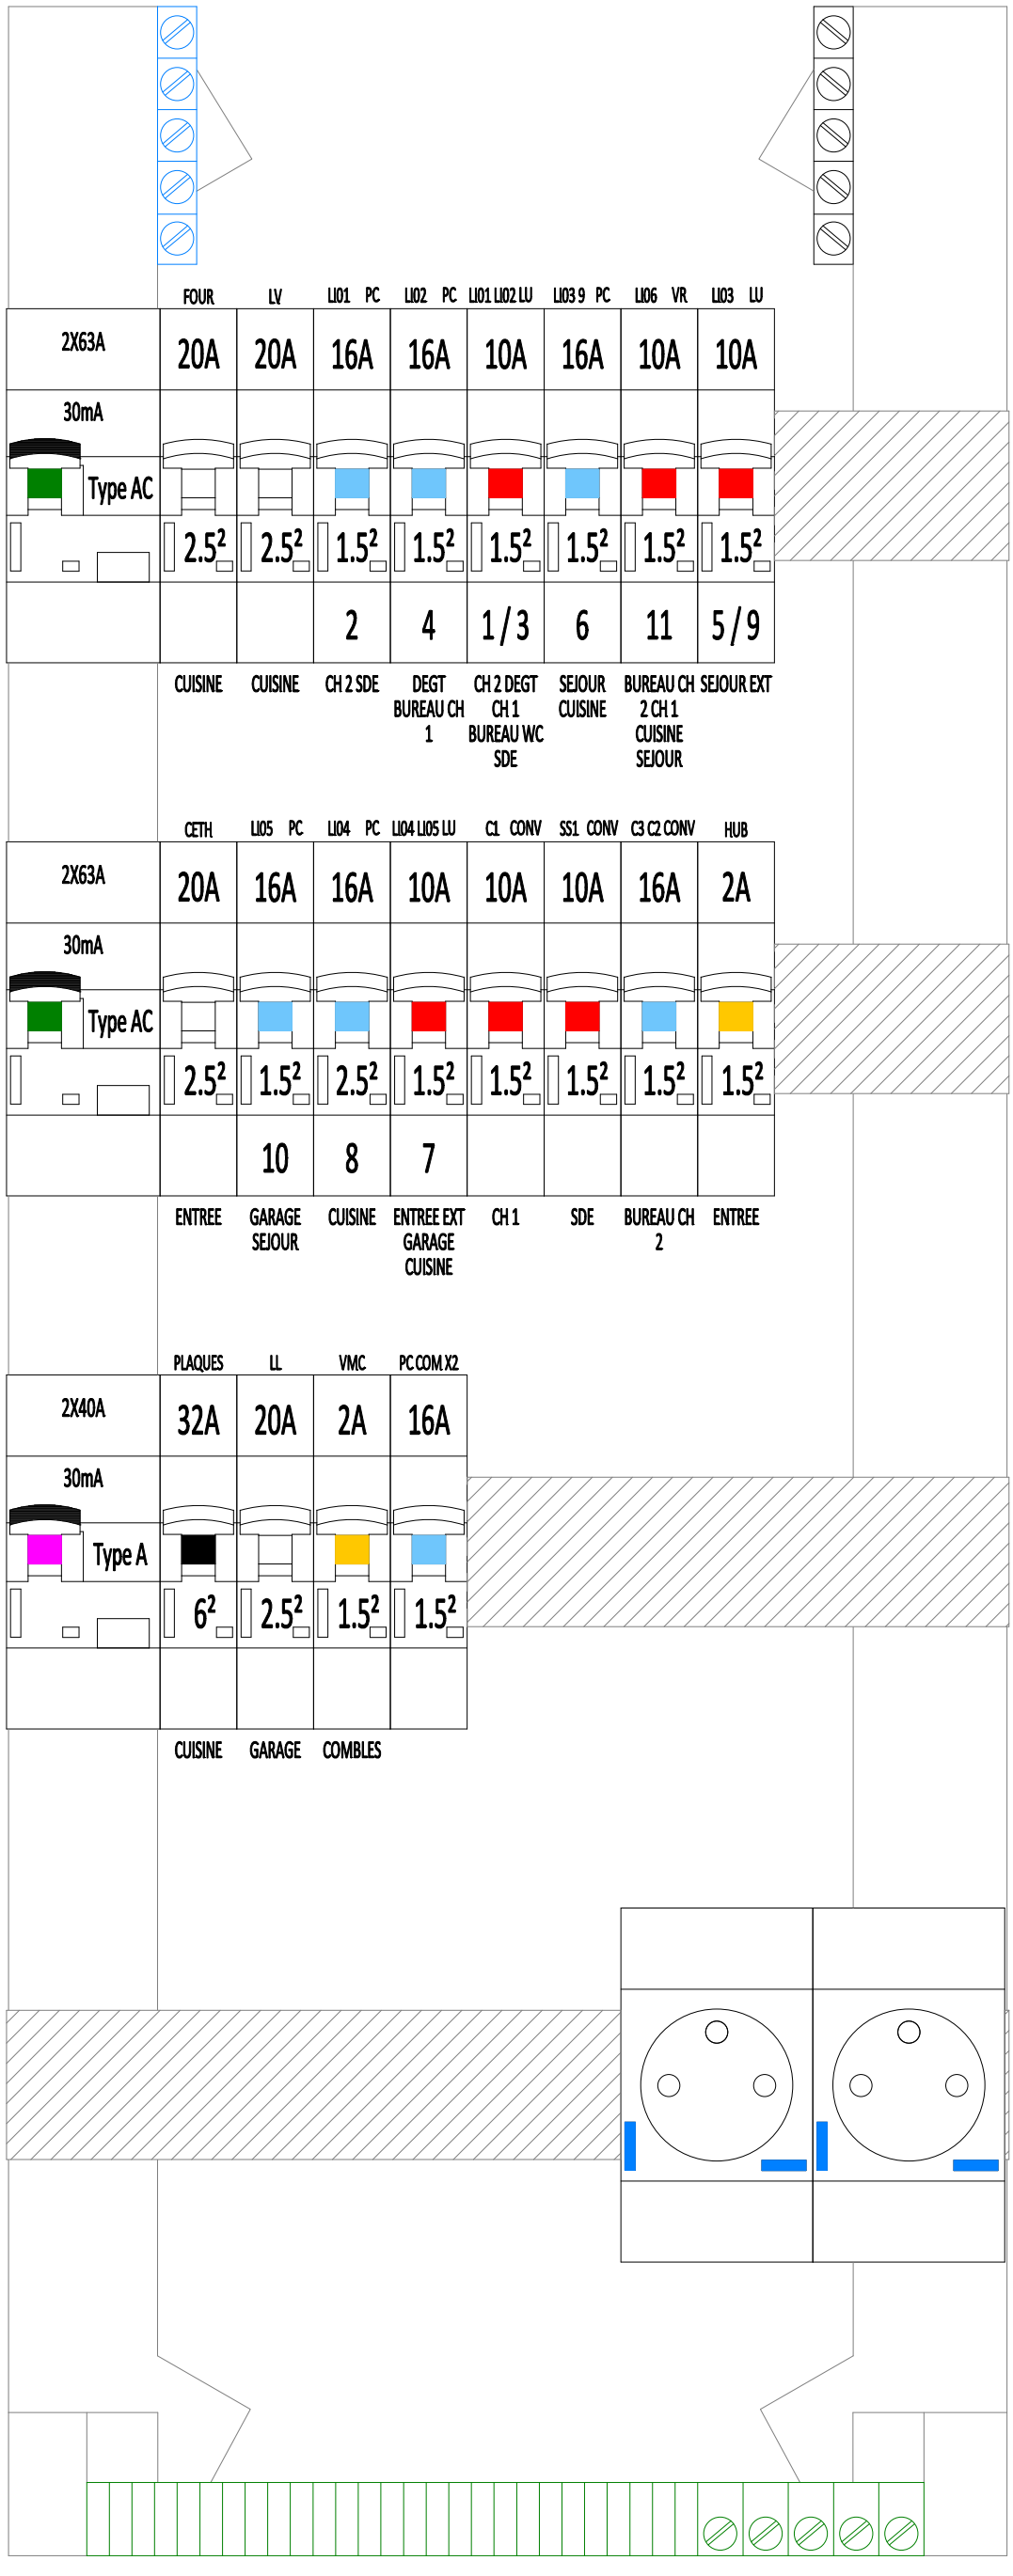

BOUCHON		
15 x16Ø	15 x20Ø	0 x25Ø

REPERE	TYPE D'APPAREIL	PIECE DESERVIE

Champs Perso			
LEGRAND		13 MODULES	
APPAIRAGE PRODUITS CONNEC			
CONNECTEURS / WAGOS			
HAGER		13 MODULES	X
SCHNEIDER		18 MODULES	
LEGRAND	X	MONOPHASE	X
GTL		TRIPHASE	
PORTE		FOND	X
BORNIER DE TERRE SUP			

X

KiTeOHM pour une maison branchée

www.kiteohm.fr

Client	JOYEUX CONSTRUCTIONS
Chantier	PASQUIER BLIN
N°	AF26064553

Echelle : 1 / 1.6
Dess : ACR
Date: 18/09/2026

JOYEUX CONSTRUCTIONS
PASQUIER BLIN
AF26064553

Nb MODULES:

PORTE
REF : _____

CONTACTEUR CE NBRE:

BOUCHON	x16	x20	x25

DMT AVEC WAGGOS

DMT SANS WAGGOS

MONOPHASE

TRIPHASE

DISJONCTEUR
REF : _____

TORES
CH ☐ CE ☐ PC ☐

TYPE CHAUFFAGE

TYPE ECS

REPERE	TYPE D'APPAREIL	PIECE DESERVIE

