SAS JOYEUX CONSTRUCTIONS
150 Av. des Hauts de la Chaume
86280 Saint-Benoît
Tél: 05 49 46 10 71

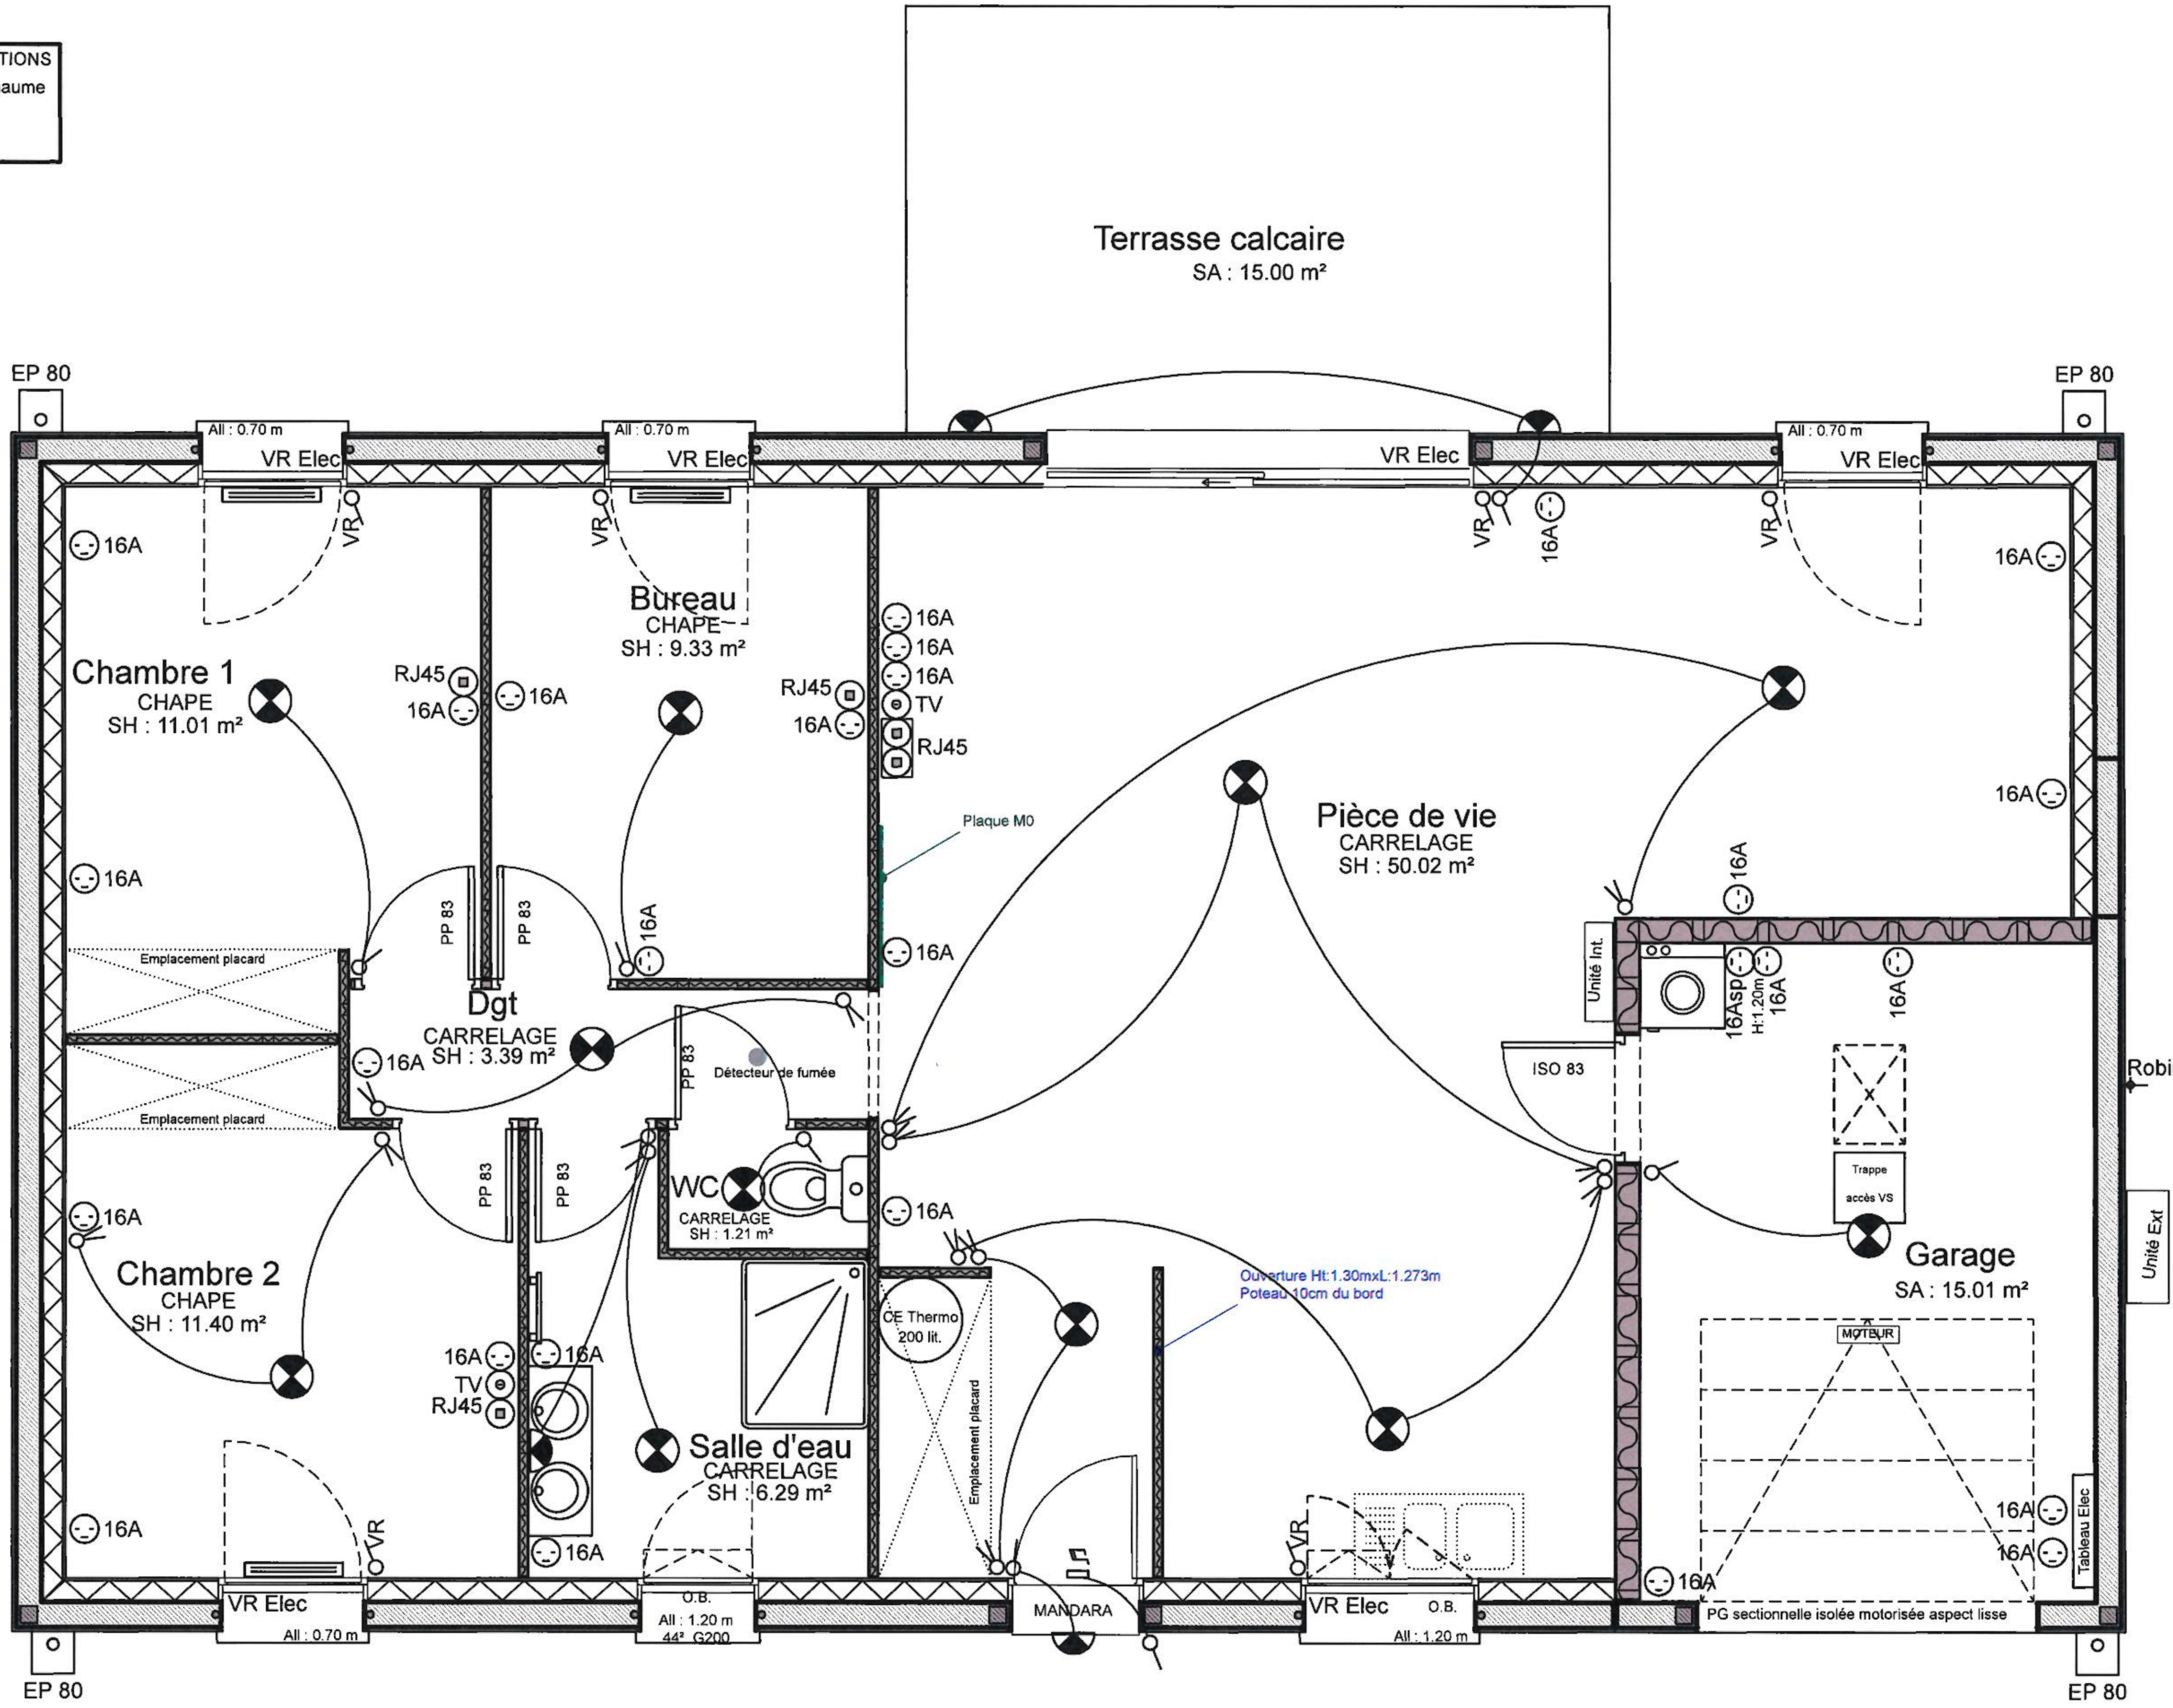

PAC Air Air selon Etude Thermique

M. PASQUIER Mme BLIN
Lotissement "Le Clos des Vignes 3" lot 35
86800 BIGNOUX

Plan Elec DEFINITIF
ECH.: 1/50
Dossier N°2192
dessiné par : PA
le : 10 06 2026

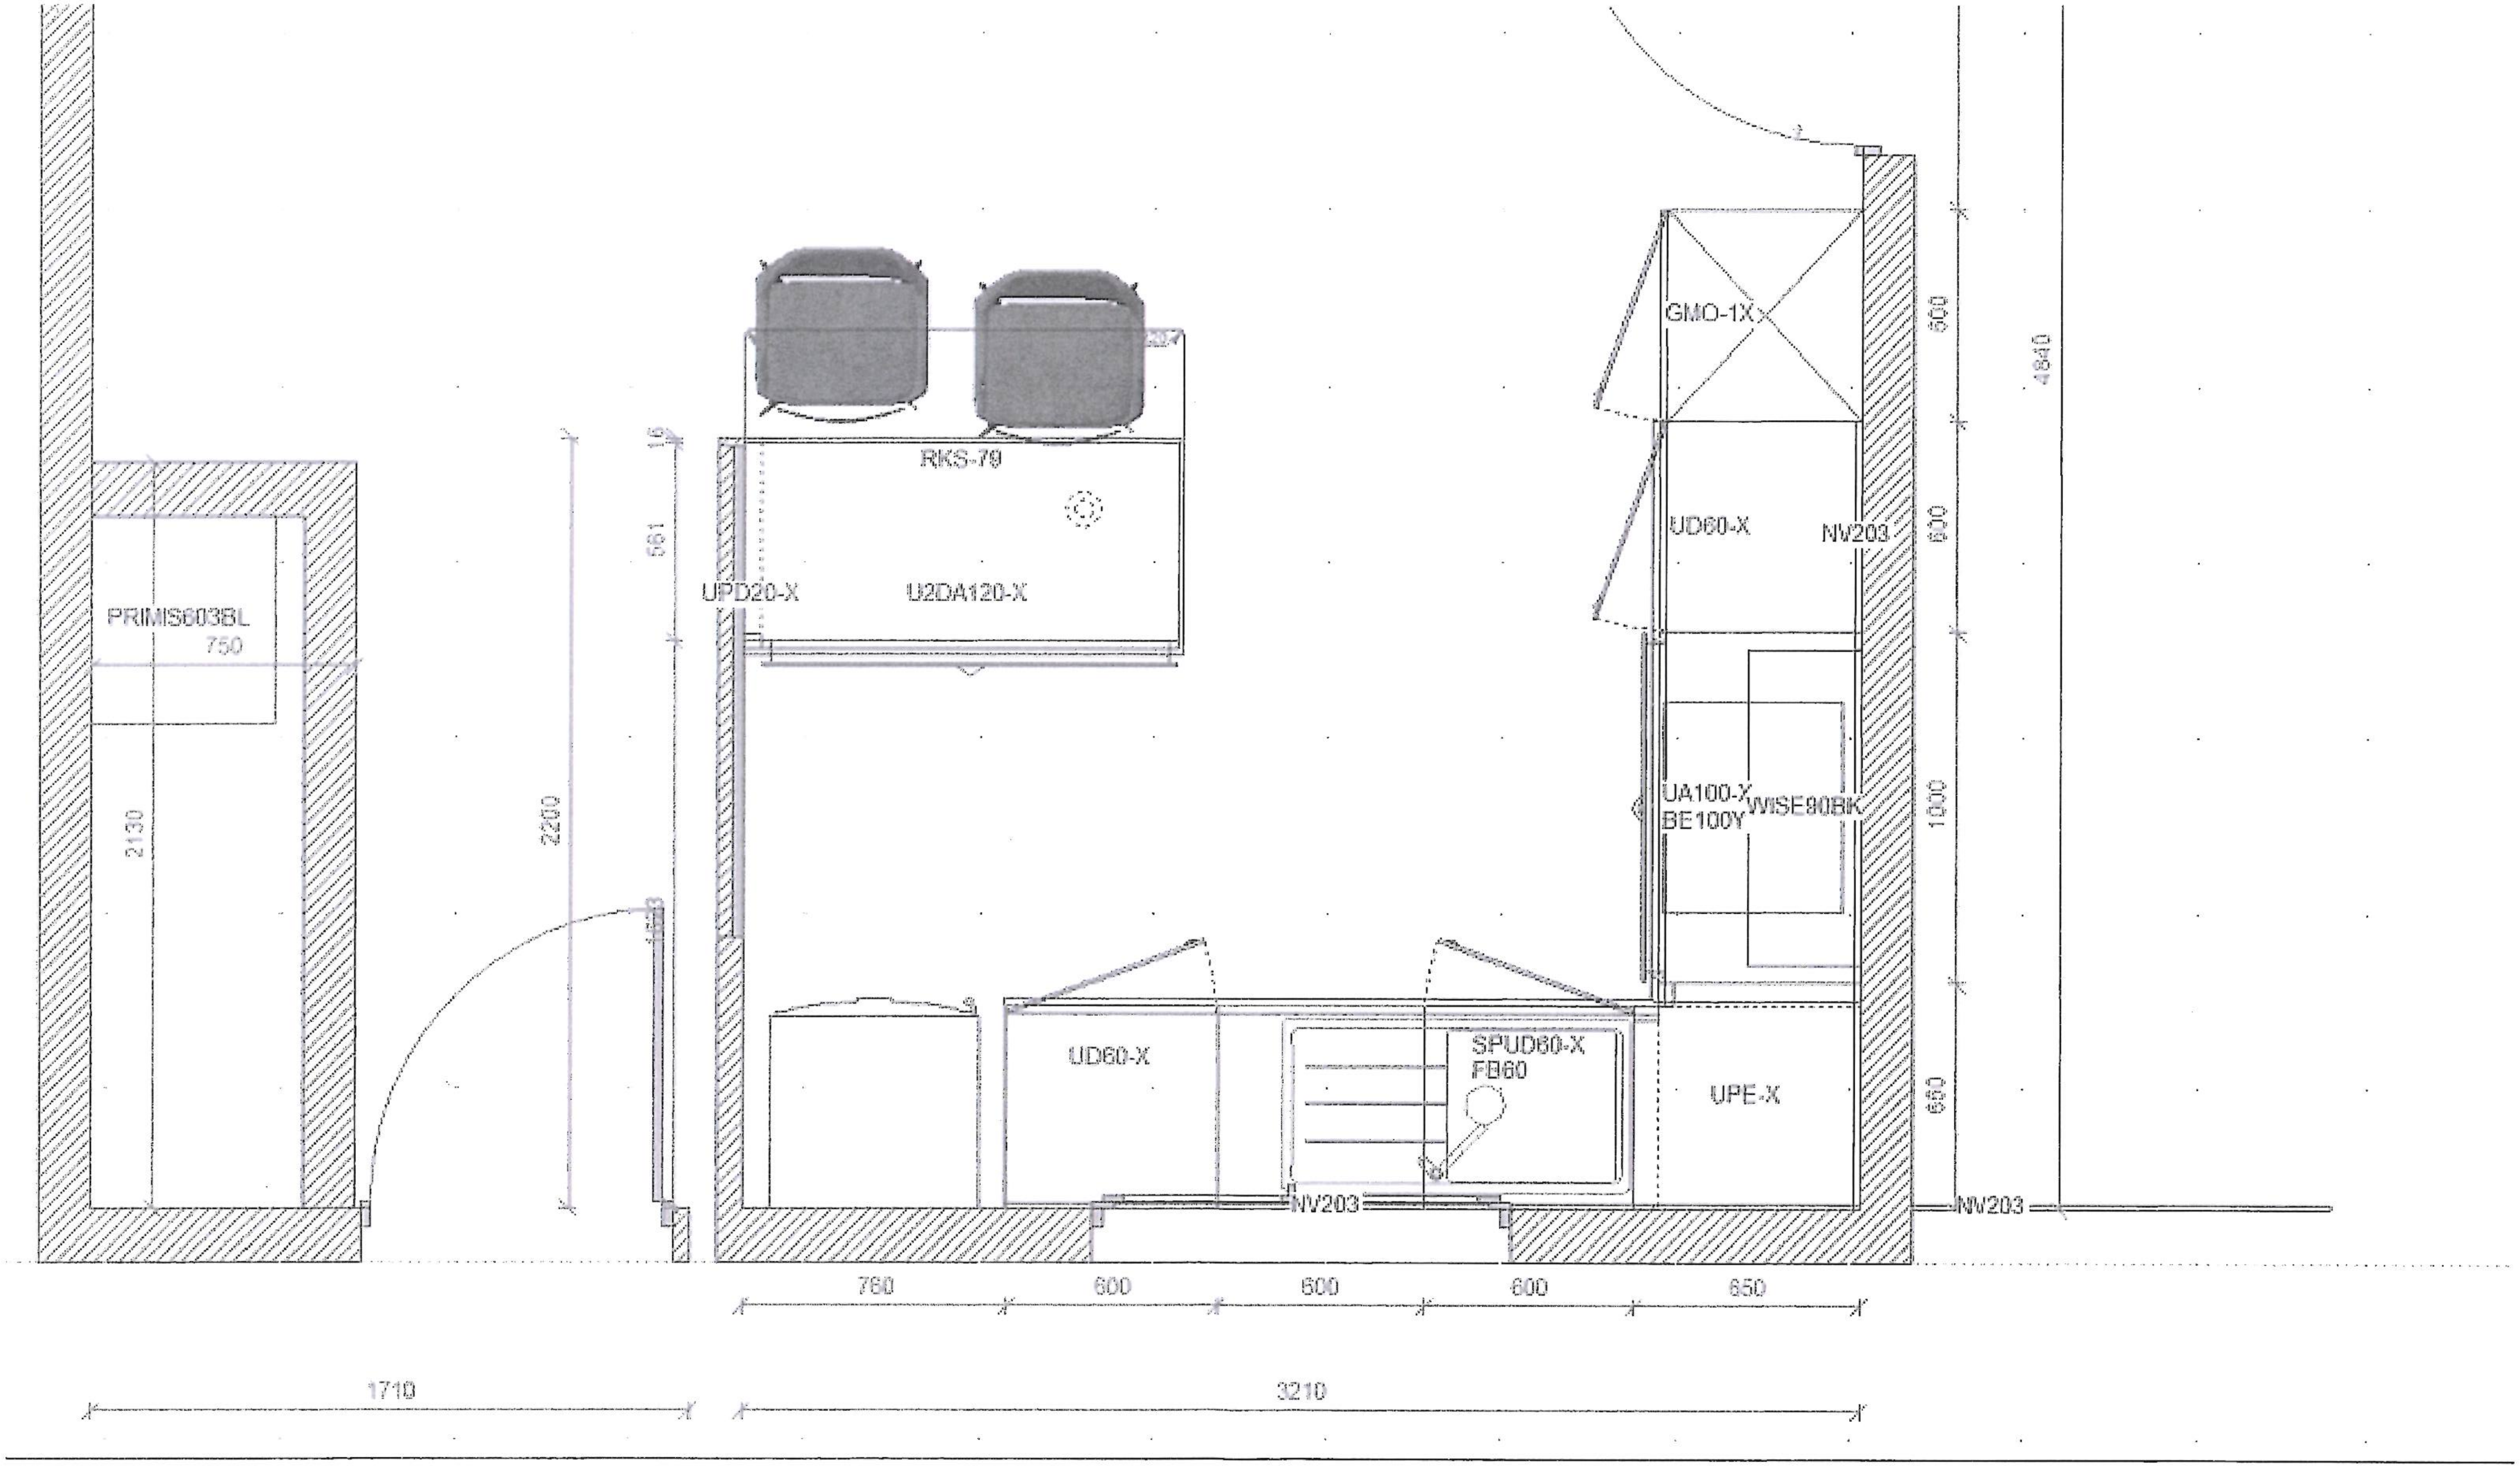
PRIMIS603BL
750
2130
2200
16
561
RKS-79
UPD20-X
U2DA120-X
GMO-1X
UD60-X
NV203
UA100-X
BE100Y
WISE90BK
UD60-X
SPUD60-X
FB60
UPE-X
NV203
NV203
600
600
1000
650
4840
760
600
600
600
650
1710
3210

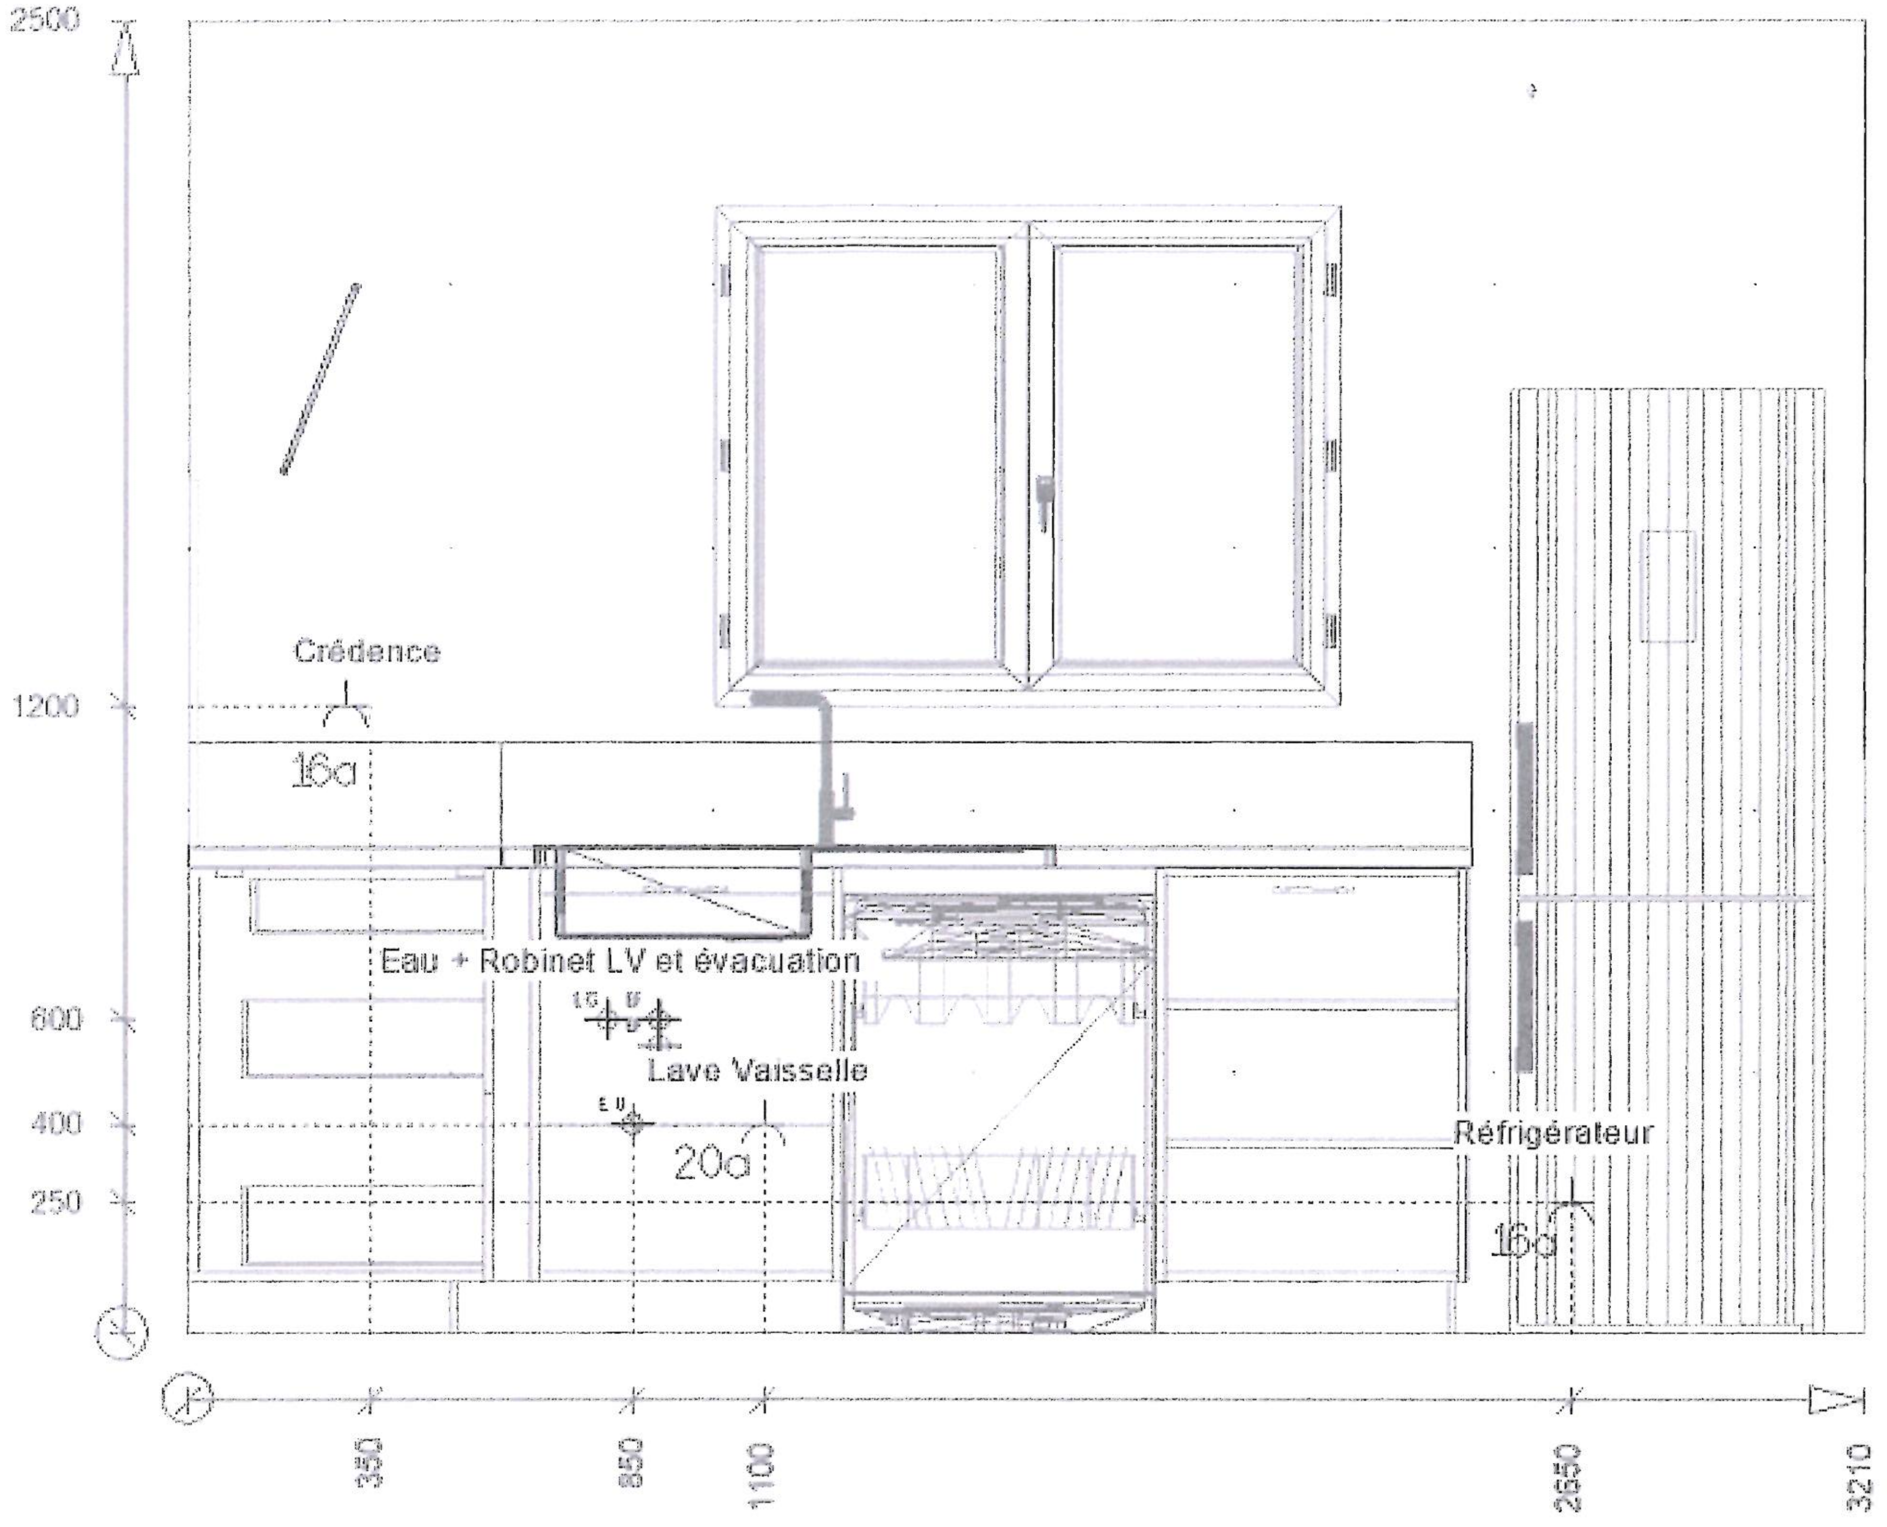
Crédence
Eau + Robinet LV et évacuation
EC
EF
Lave Vaisselle
EU
Réfrigérateur

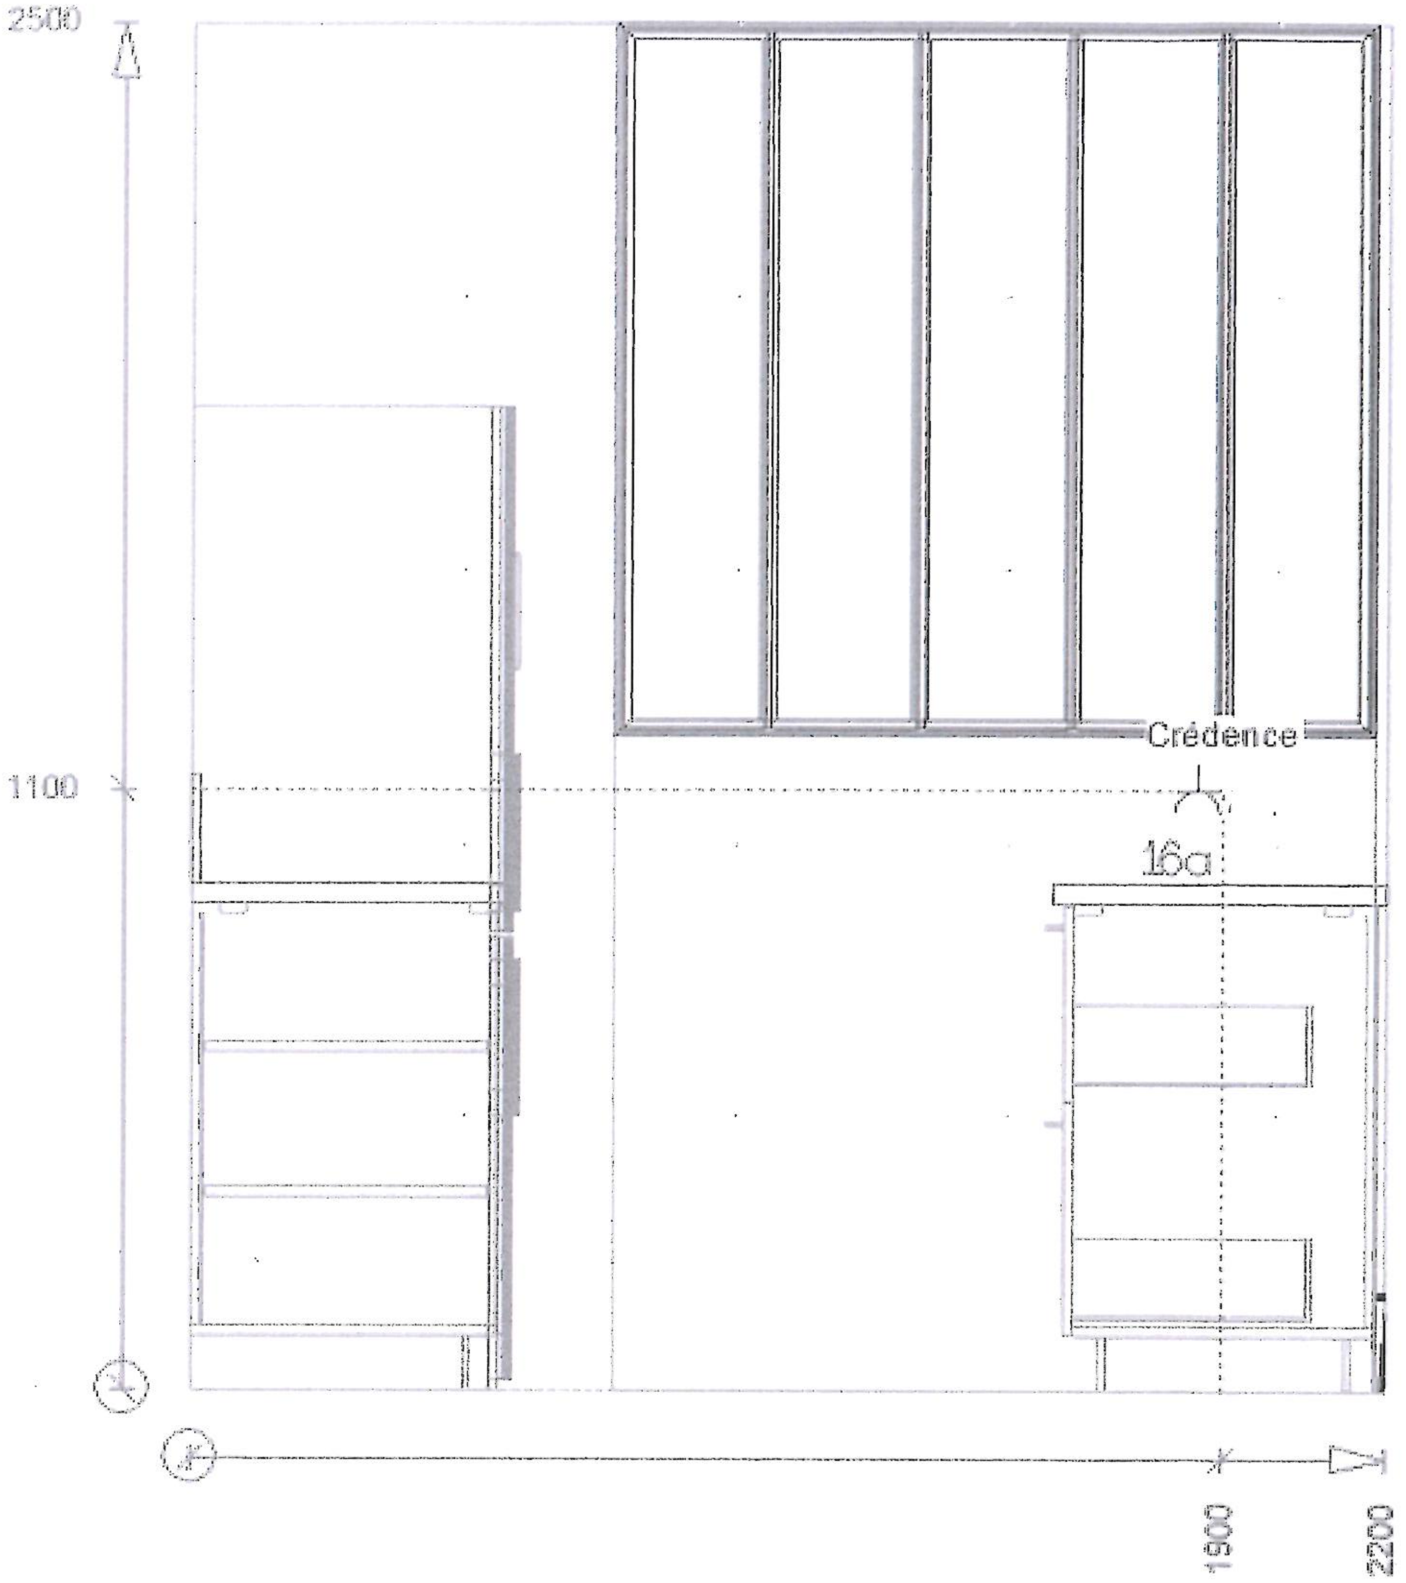
Crédence
1900

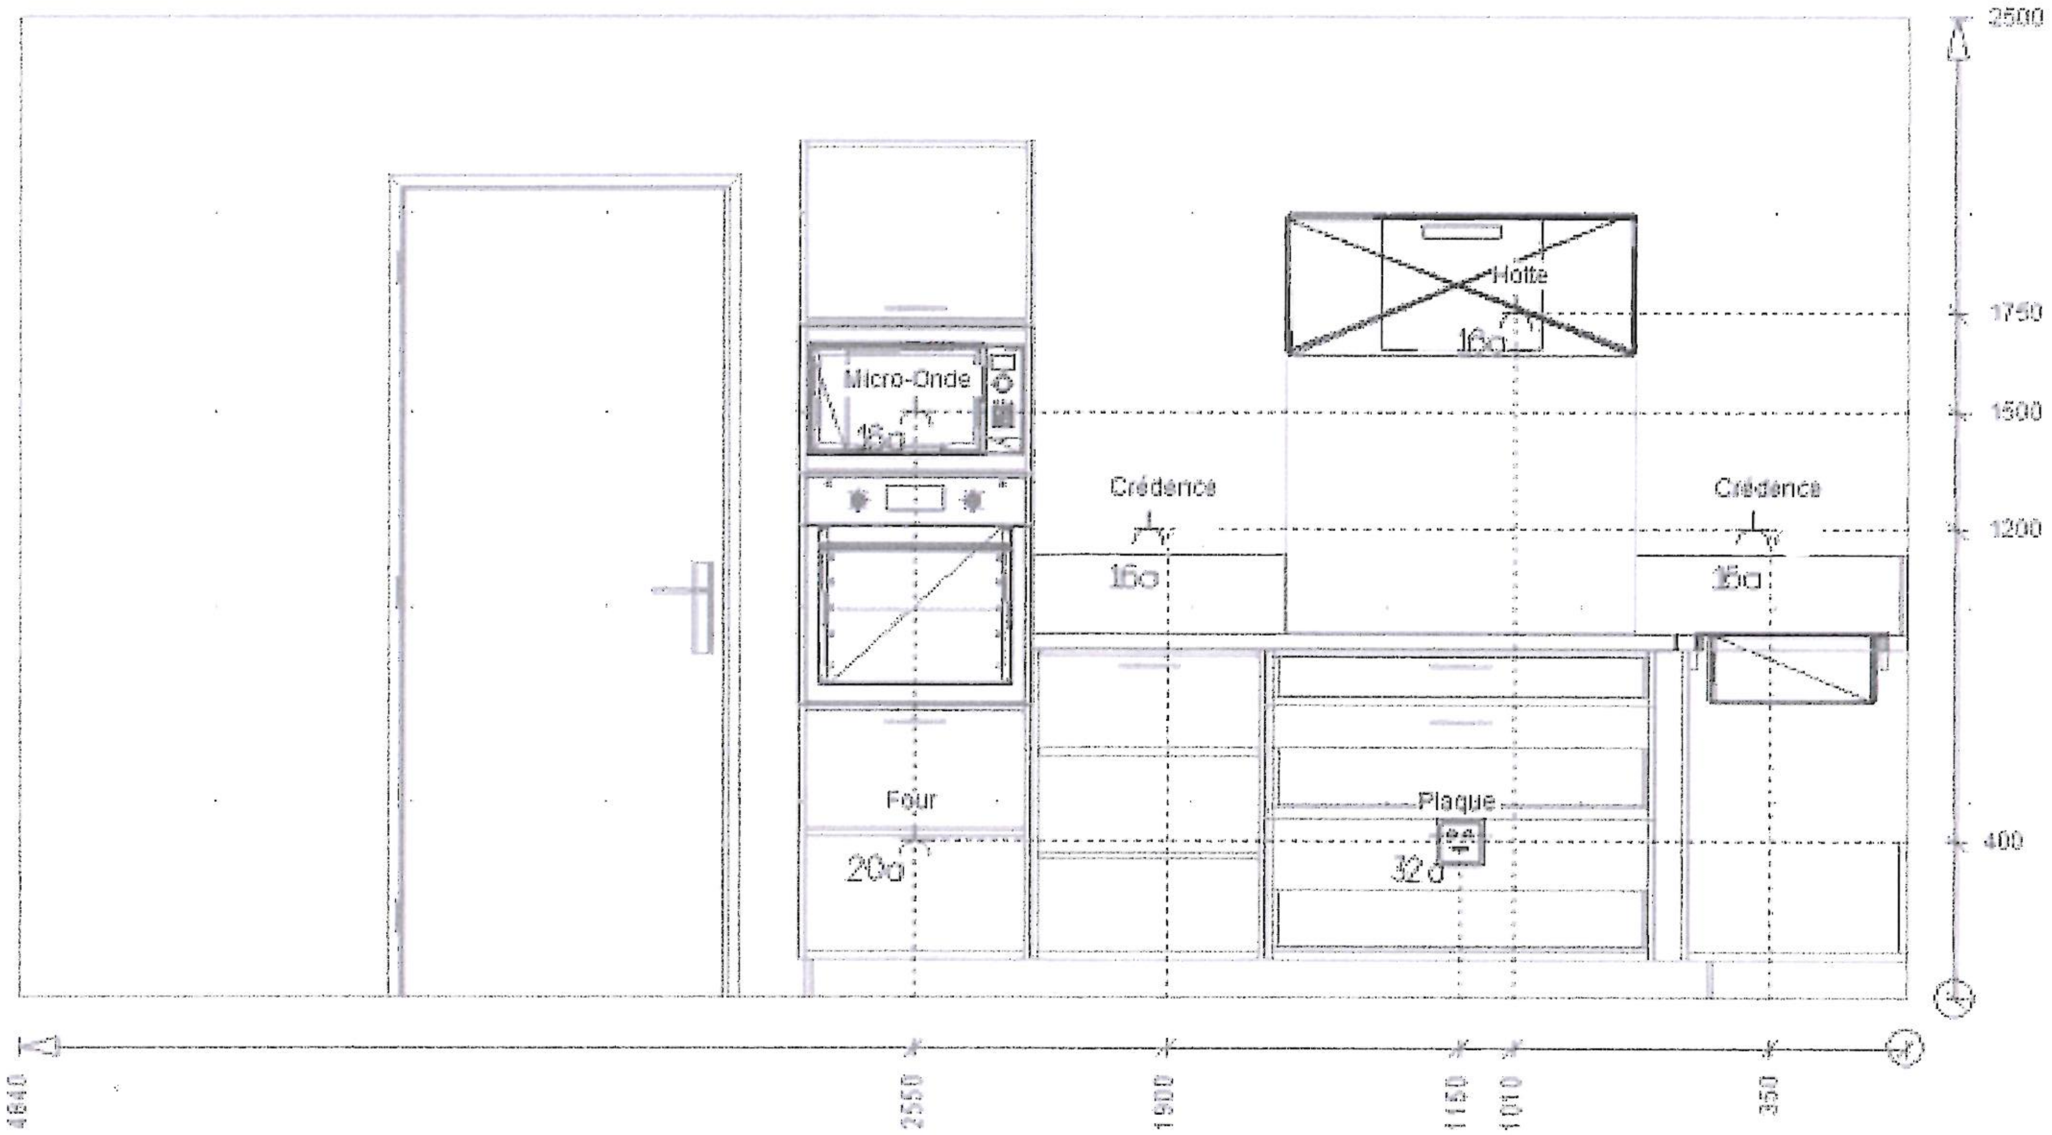
1750
1500
Hotte
Micro-Onde
Crédence
Crédence
Four
Plaque
1900