
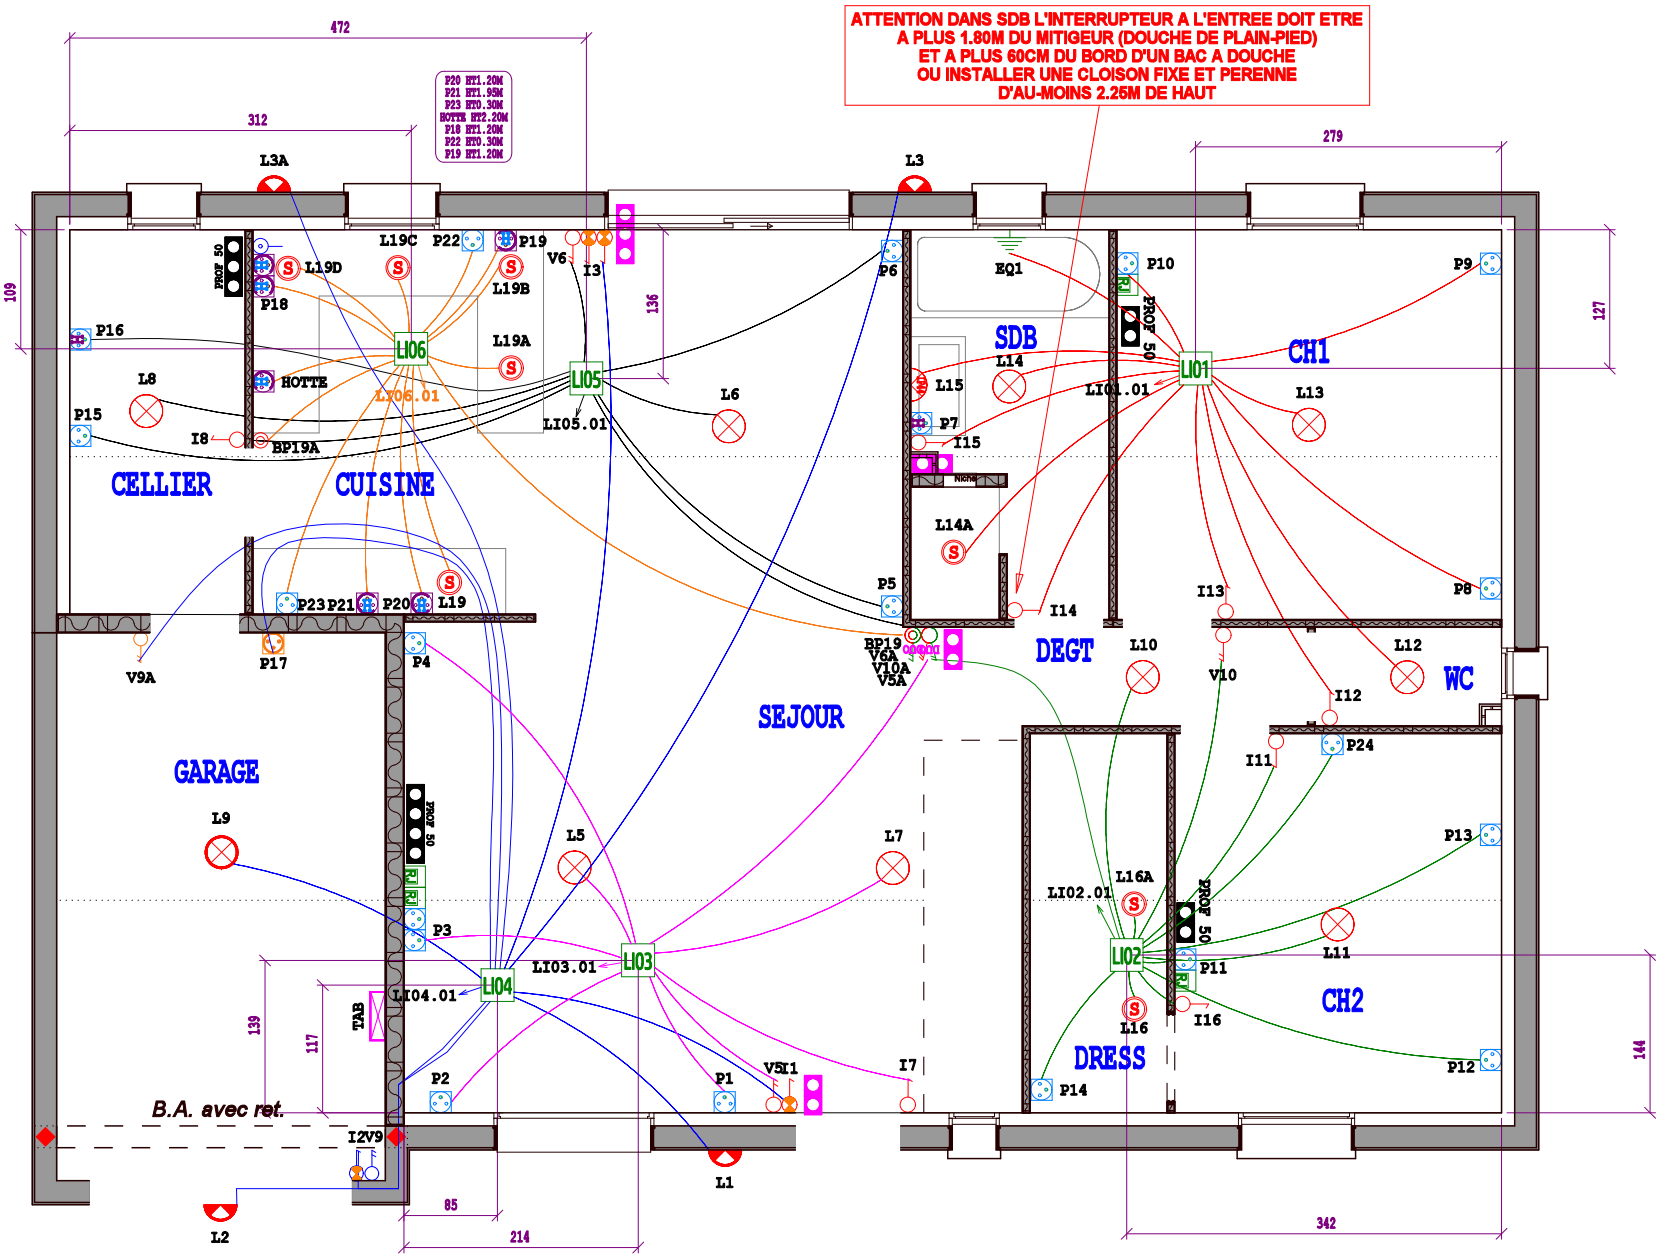


LES BOÎTES SE TROUVENT DANS LES RAMPANTS DES COMBLES AMÉNAGEABLES

KiTēOHM pour une maison branchée	www.kiteohm.fr	Client	MENUISERIE ISOLATION DU CENTRE (MIDC)
		Chantier	EVRARD 04949
		N°	AF26074879

Echelle : 1 / 50
Dess : NC
Date : 20/10/2026

Les appareillages sont positionnés sur le plan à titre indicatif, ils doivent être installés en fonction des normes en vigueur.
Les hauteurs en cm sont données à titre indicatif, suivre les valeurs indiquées sur le plan .
⚠ Les hauteurs sont données à partir du sol fini ! ⚠

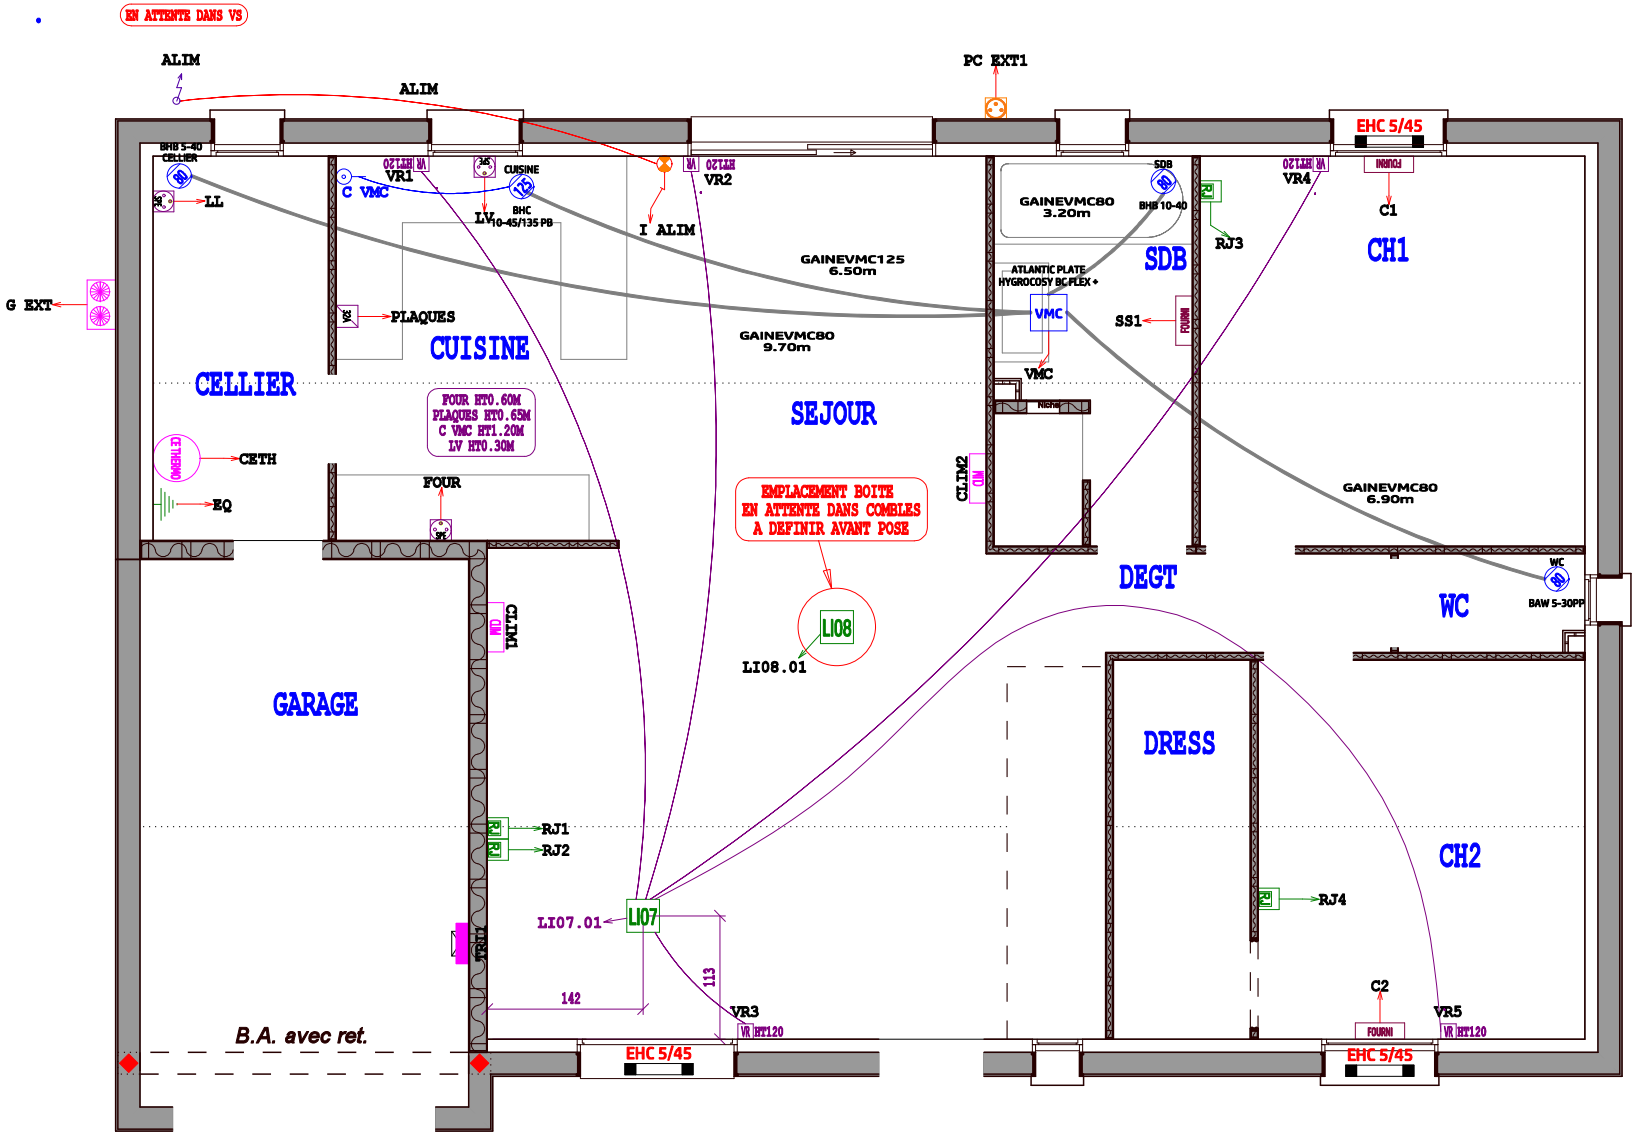


LES BOÎTES SE TROUVENT DANS LES RAMPANTS DES COMBLES AMÉNAGEABLES

BOUCHONS GAINES 16/20/25 | PORTE TRI 1 RANGEE | GAINE Ø125 SPIREO 10ml | GAINE Ø80 SPIREO 10ml

KiTēOHM pour une maison branchée	www.kiteohm.fr	Client	MENUISERIE ISOLATION DU CENTRE (MIDC)
		Chantier	EVRARD 04949
		N°	AF26074879

Echelle : 1 / 50
Dess : NC
Date : 20/10/2026

Les appareillages sont positionnés sur le plan à titre indicatif, ils doivent être installés en fonction des normes en vigueur.
Les hauteurs en cm sont données à titre indicatif, suivre les valeurs indiquées sur le plan .
⚠ Les hauteurs sont données à partir du sol fini ! ⚠

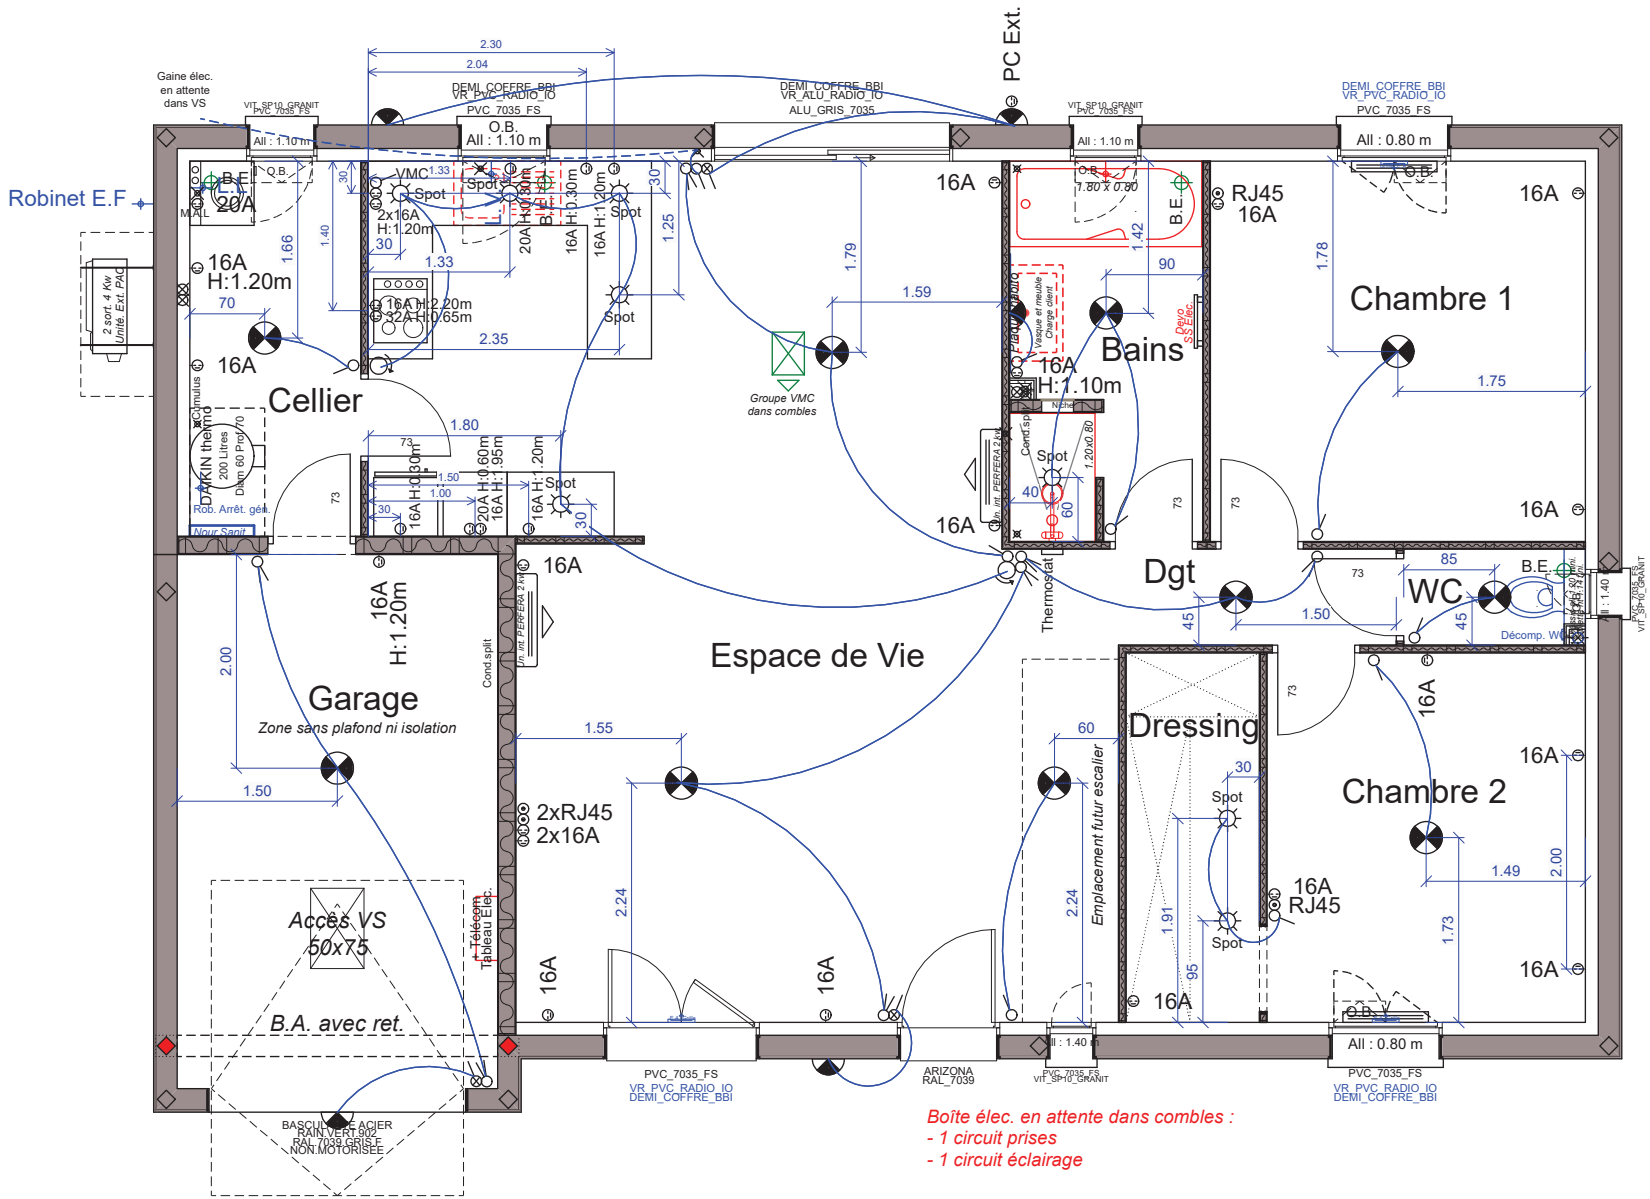

PLAN DEFINITIF

Maisons CPR

M. EVRARD Mme GOUIN . Dossier N° : 04949 Type de plans : EXECUTION	INDICES B	8 - Plan Electrique RDC ECH.: 1/50 Projet N°: 9797 Dessiné par : RR le : 11 06 26