
PLAN DE VENTILATION

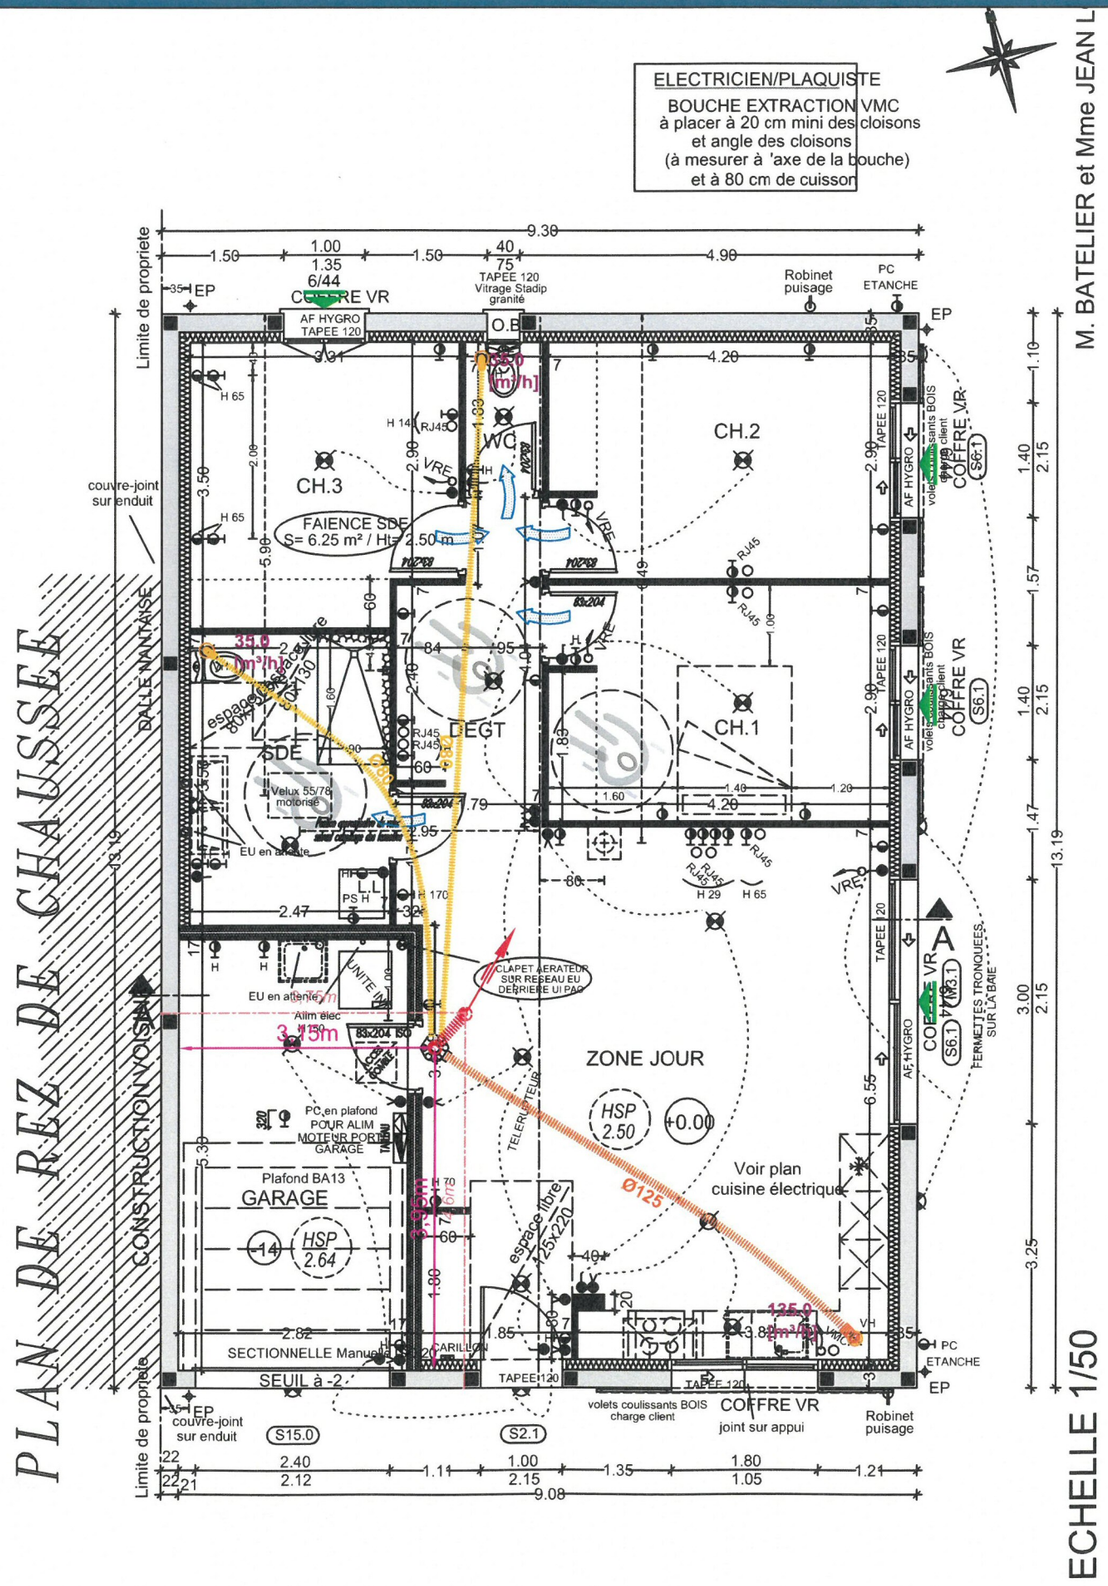

DIMENSIONNEMENT

LEGENDE

BOUCHE EXTRACTION HYGRO 125mm		CONDUIT EXTRACTION 125mm Souple isolé		CONDUIT EXTRACTION 200x60mm Rigide	60x200
BOUCHE EXTRACTION HYGRO 80mm		CONDUIT EXTRACTION 80mm Souple isolé		CONDUIT EXTRACTION 100x40mm Rigide	40x100
ENTREE D'AIR HYGRO *EH 6/44*	6/44	DETALONNAGE GRILLE DE TRANSFERT		REDUCTION 80mm / 125mm	
ENTREE D'AIR AUTO *EA*	30 45	DEBIT EXTRACTION MAX	45[m³/h]	REJET TOITURE 160mm	
CAISSON VMC		CONDUIT REJET 160mm Souple isolé			

DIMENSIONNEMENT - VMC SIMPLE FLUX HYGRO DE TYPE B

Bouche	Ref. Bouche	Diam. Bouche	Débit m3/h	Diam. Conduit	Longueur (m) gaine souple	Nbre Coude souple 45°	Nbre Coude souple 90°	Longueur (m) gaine rigide	Nbre Coude rigide 45°	Nbre Coude rigide 90°	P. de Ch (Pa)
Cuisine	C51	125,0	151,2	125,0	6,98	0,0	1	0,0	0,0	0,0	124,3
Sdb WC 1	BW51	80	39	80	6,82	0,0	1	0,0	0,0	0,0	123,4
WC 1	W16	80	34	80	9,25	0,0	1	0,0	0,0	0,0	123,3

CAISSON

REFERENCE : **ALDES EASYHOME PREMIUM MP**

CONSOMMATION : **9.5 W-Th-C**

P. DISPONIBLE à Qmax : **164.2 Pa**

P. REQUISE RESEAU DEFAVORABLE : **156.9 Pa**



Image d'illustration

REJET

REFERENCE : **TERREAL Cobra**

LONGUEUR REJET : **1.5 M**

NOMBRE DE COUDE : **1 x 90°**



Image d'illustration

REMARQUES :

- Les entrées d'air et bouches d'extraction sont certifiées CSTEat-35 et de marque compatible avec le caisson d'extra ction.
- Les conduits d'extraction cheminant hors volume chauffé sont isolés
- Les entrées d'air sont à installer en partie haute en regard de passages d'air ménagés sur les menuiseries, les coffres de volets roulants ou sur les murs selon les instructions du fabriquant
- Détalonnage : La circulation d'air d'une pièce à l'autre est assurée par un réhaussement des bloc-portes de manière à ménager un passage d'air en partie basse de l'ouvrant - Détalonnage 1 cm minimum Sauf pour les Cuisines fermées 2 cm.
- Rejet : doit être fait directement sur l'extérieur par le biais d'un terminal conforme aux normes en vigueur et placé sur le tiers supérieur de la toiture.
- Il est recommandé d'indiquer que le rejet doit être positionné de telle sorte à ne pas avoir d'obstacle perturbant à moins de 2m.
- Une protection électrique exclusivement dédiée au caisson doit être installée sur le tableau électrique de type disjoncteur divisionnaire 2A.
- En présence d'une PAC Air/Air Gainable, son avis technique devra etre compatble avec l'avis technique de la présente VMC.

NORMES :

- NF DTU 68.3 "Travaux de bâtiment Installations de ventilation mécanique"
- CPT "Systèmes de ventilation mécanique contrôlée simple flux hygroréglable"
- CSTBat-35 "Ventilation Hygroréglable"
- NF EN 13180 "Réseau de conduits"
- Avis techniques en vigueur
- Nouvelle réglementation acoustique NRA
- Protocole VMC RE2020
- NF C15-100
- Conformité C.E.

MAITRE D'OUVRAGE

BATELIER Cyprien et JEAN LOUIS Anaïs

PROJET - *REF 25101002*

Construction d'une maison individuelle
Lotissemnt "Villa Dulci"
17230 Villedoux

DOCUMENT


DIMENSIONNEMENT VENTILATION

Réalisé le : 31 / 08 / 26 **Par : DE** **Echelle : 1 /75e** **Page : 1 / 1**

effinéo
BUREAU D'ÉTUDES THERMIQUES & FLUIDES
50 Rue des Couvreurs
85800 ST GILLES CROIX DE VIE
Tel : 02.28.10.96.43

Maisons LARA
72 Avenue Edmond Grasset
17442 AYTRE CEDEX
Tél. : 05.46.44.27.58

Les appareillages sont positionnés sur le plan à titre indicatif, ils doivent être installés en fonction des normes en vigueur.
Les hauteurs en cm sont données à titre indicatif, suivre les valeurs indiquées sur le plan .
⚠ Les hauteurs sont données à partir du sol fini ! ⚠

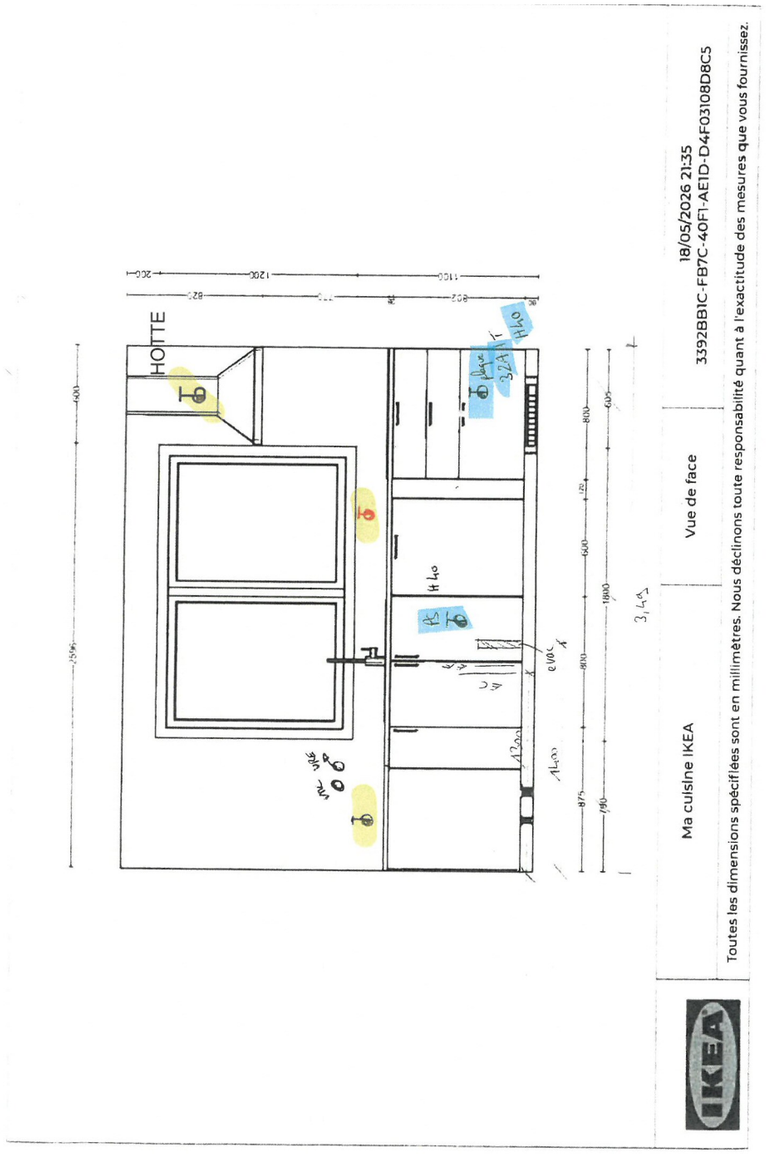


Vue de face

18/05/2026 21:35
3392BB1C-FB7C-40F1-AE1D-D4F03108D8C5

Toutes les dimensions spécifiées sont en millimètres. Nous déclinons toute responsabilité quant à l'exactitude des mesures que vous fournissez.

Ma cuisine IKEA

BATELIER

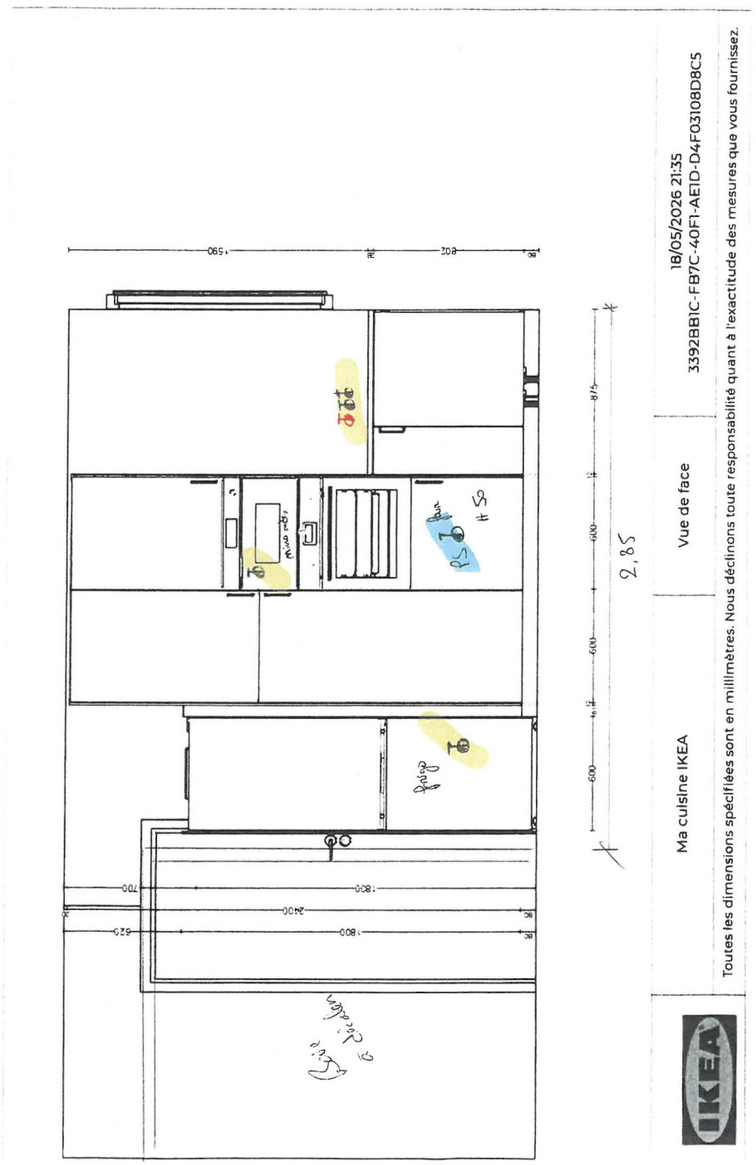

Vue de face

18/05/2026 21:35
3392BB1C-FB7C-40F1-AE1D-D4F03108D8C5

Toutes les dimensions spécifiées sont en millimètres. Nous déclinons toute responsabilité quant à l'exactitude des mesures que vous fournissez.


Ma cuisine IKEA

BATELIER

KiTēOHM pour une maison branchée	www.kiteohm.fr	Client	MAISONS LARA
		Chantier	BATELIER JEAN LOUIS L51S078C
		N°	AF26064644

Echelle : 1 / 1
Dess : mlaurent
Date : 07/10/2026

Les appareillages sont positionnés sur le plan à titre indicatif, ils doivent être installés en fonction des normes en vigueur.
Les hauteurs en cm sont données à titre indicatif, suivre les valeurs indiquées sur le plan .
⚠ Les hauteurs sont données à partir du sol fini ! ⚠

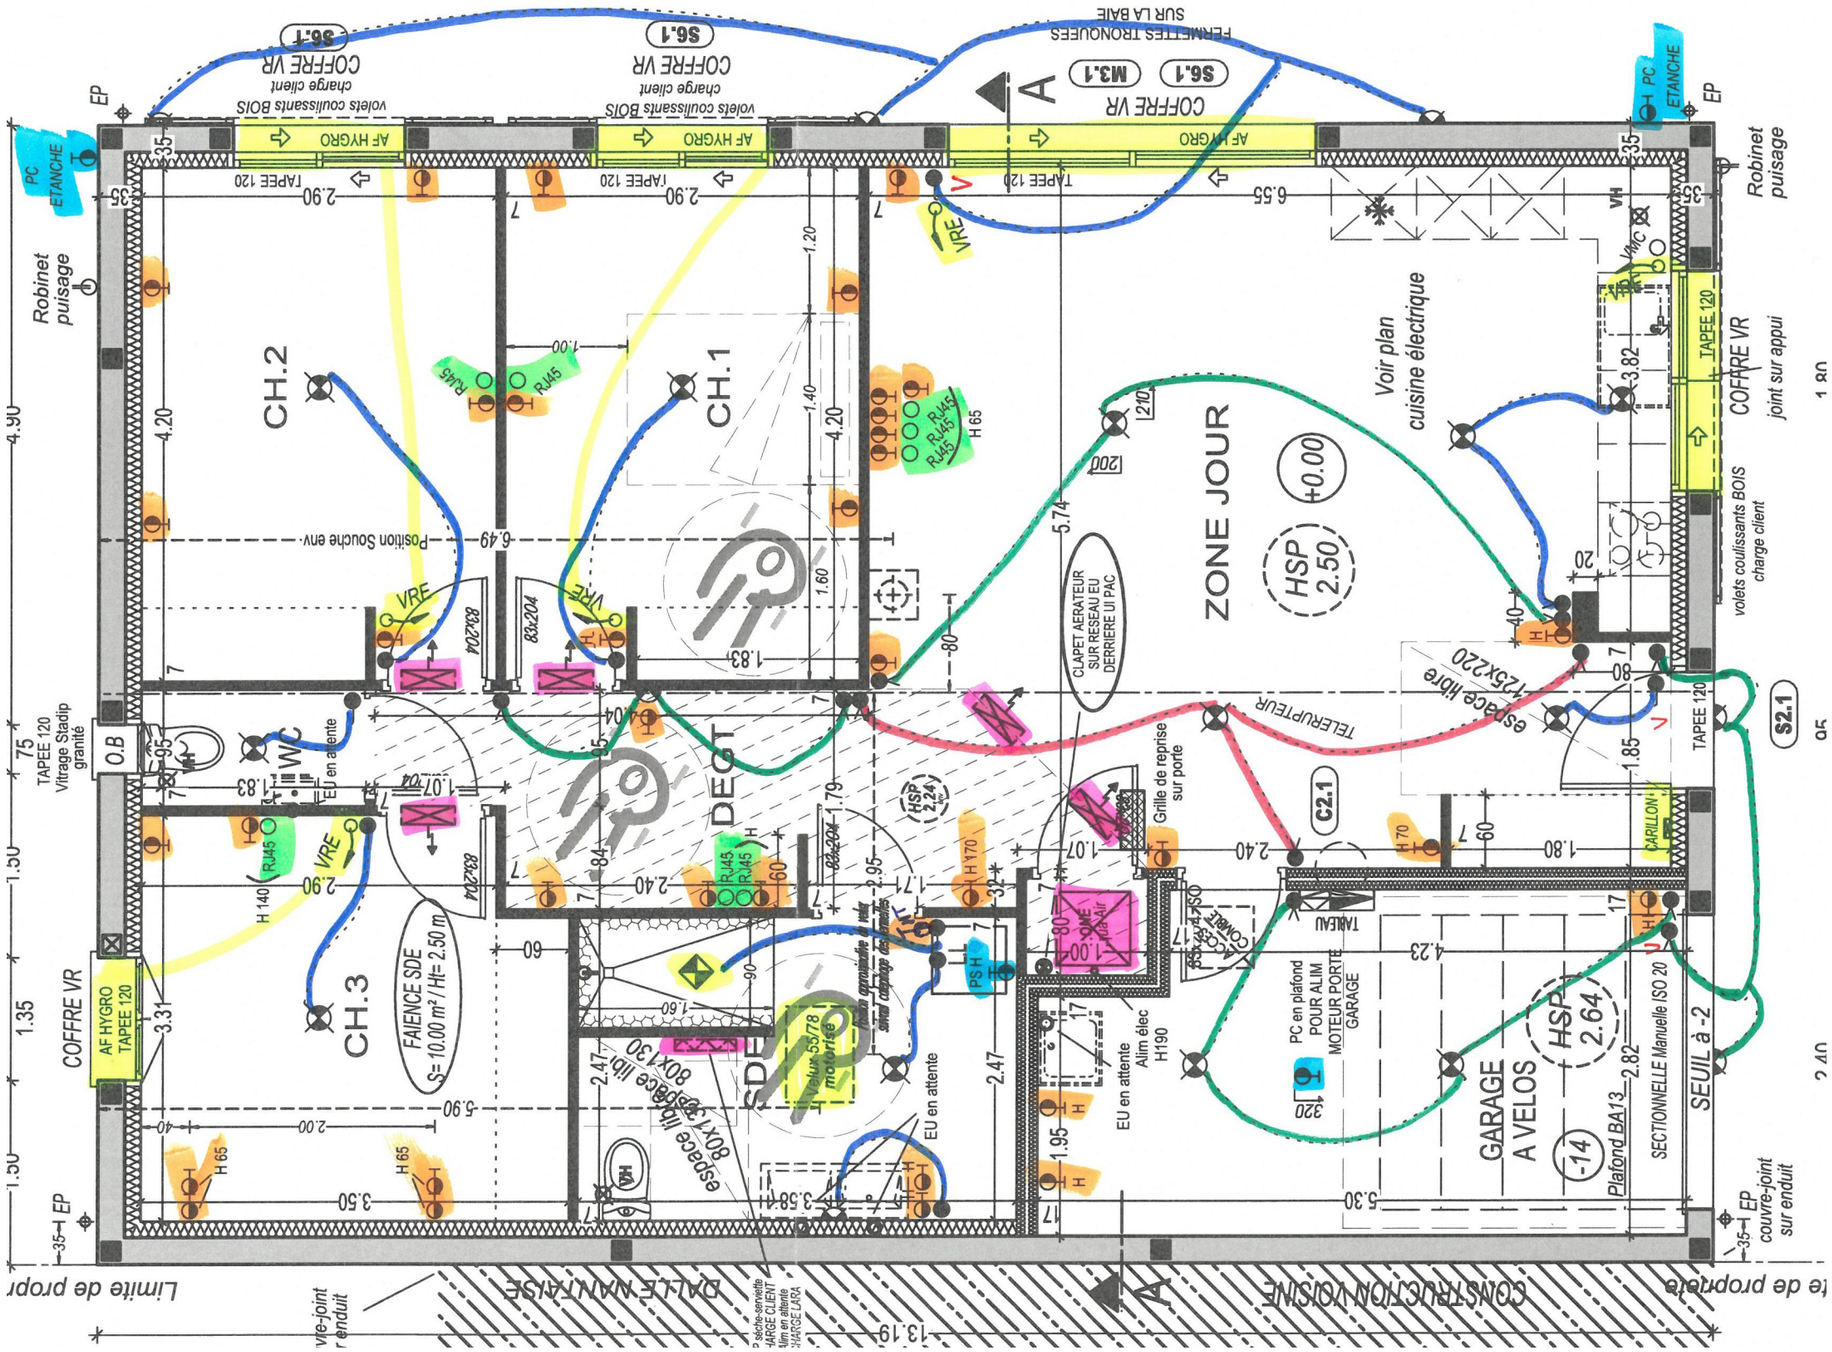

KiTēOHM pour une maison branchée	www.kiteohm.fr	Client	MAISONS LARA
		Chantier	BATELIER JEAN LOUIS L51S078C
		N°	AF26064644

Echelle : 1 / 1
Dess : mlaurent
Date : 07/10/2026


Les appareillages sont positionnés sur le plan à titre indicatif, ils doivent être installés en fonction des normes en vigueur.
Les hauteurs en cm sont données à titre indicatif, suivre les valeurs indiquées sur le plan .
⚠ Les hauteurs sont données à partir du sol fini ! ⚠


	Boite pavillonnaire
	Bouton poussoir
DB6	Interrupteur double allumage
	Interrupteur simple allumage
	Interrupteur simple allumage lumineux
DB3	Interrupteur simple allumage + Va-et-Vient


	Interrupteur Va-et-Vient
DB6	Interrupteur Va-et-Vient + Bouton poussoir
	Interrupteur Va-et-Vient lumineux
	Plaque double Horizontale
	Plaque double Verticale
	Plaque quadruple Horizontale

	Plaque triple Horizontale
	Plaque triple Verticale
	Applique étanche
TPH	Applique murale salle de bain
S	Spot lumineux
	Applique murale

	Point lumineux
	Prise de courant H0.30m (PMR H0.40m)
H	Prise de courant H1.20m
	Prise de courant Hotte
	Carillon sans fil
	Tableau d'alimentation générale basse tension
	Liaison équipotentielle

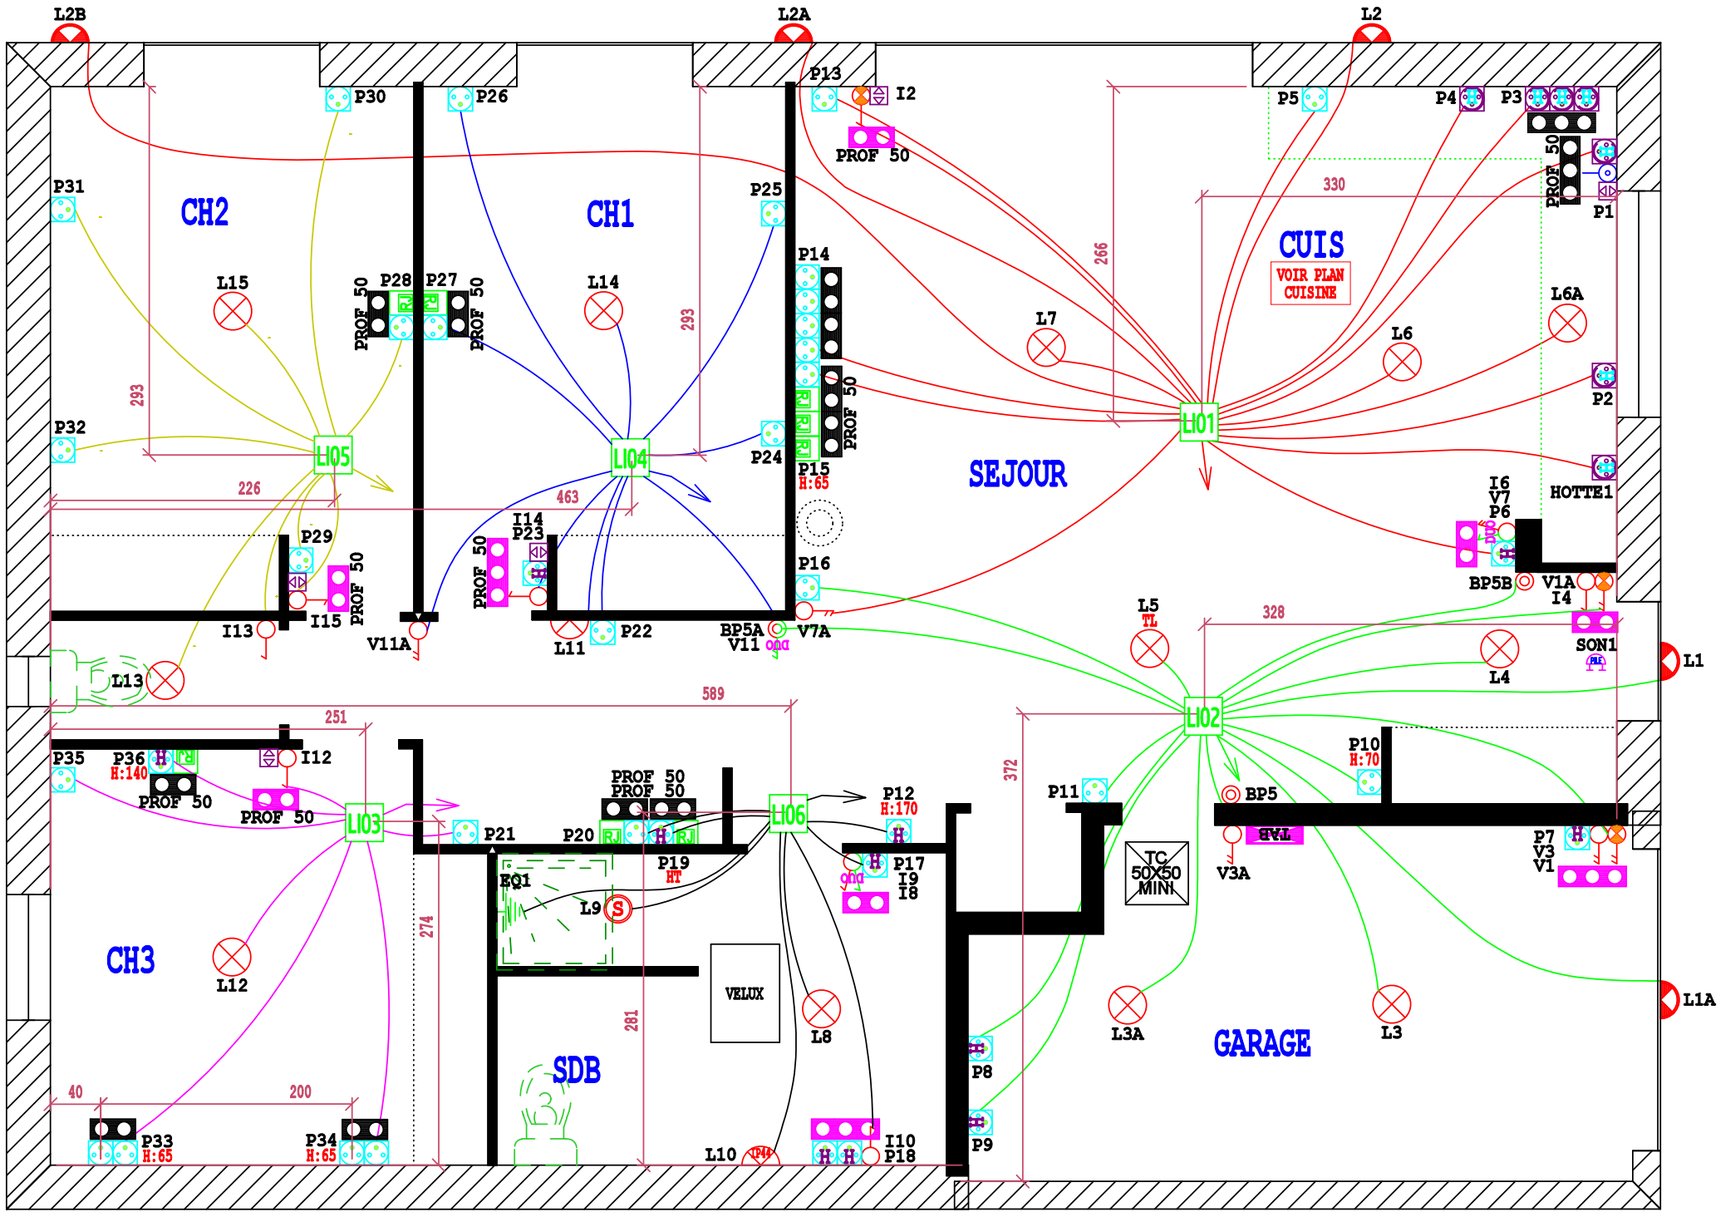

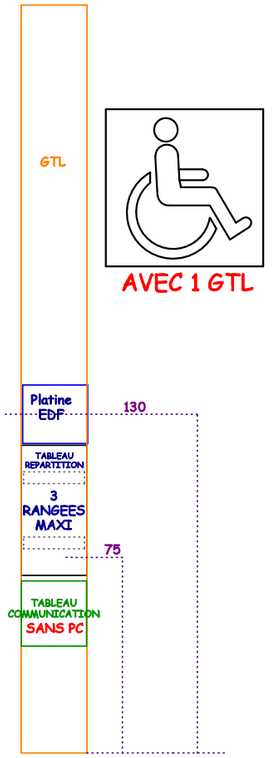

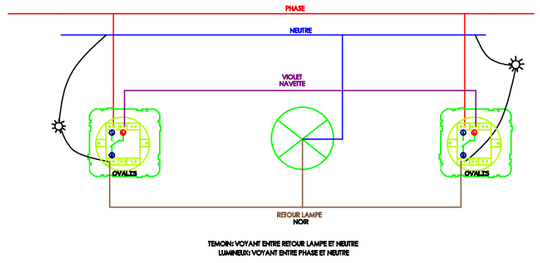

KiTēOHM pour une maison branchée

www.kiteohm.fr


Client	MAISONS LARA
Chantier	BATELIER JEAN LOUIS L51S078C
N°	AF26064644


Echelle : 1 / 50
Dess : mlaurent
Date : 07/10/2026

Les appareillages sont positionnés sur le plan à titre indicatif, ils doivent être installés en fonction des normes en vigueur.
Les hauteurs en cm sont données à titre indicatif, suivre les valeurs indiquées sur le plan .
⚠ Les hauteurs sont données à partir du sol fini ! ⚠

DFUM1 — TYWELL PRO +CONTROL — CONNECTEUR RJ45 — CONNECTEUR RJ45 — SUPPORT 4 CONNECTEURS RJ45 LEGRAND

CONNECT D'EPANOUISSEMENT — TRI GEN — CONNECTEUR RJ45 — CONNECTEUR RJ45

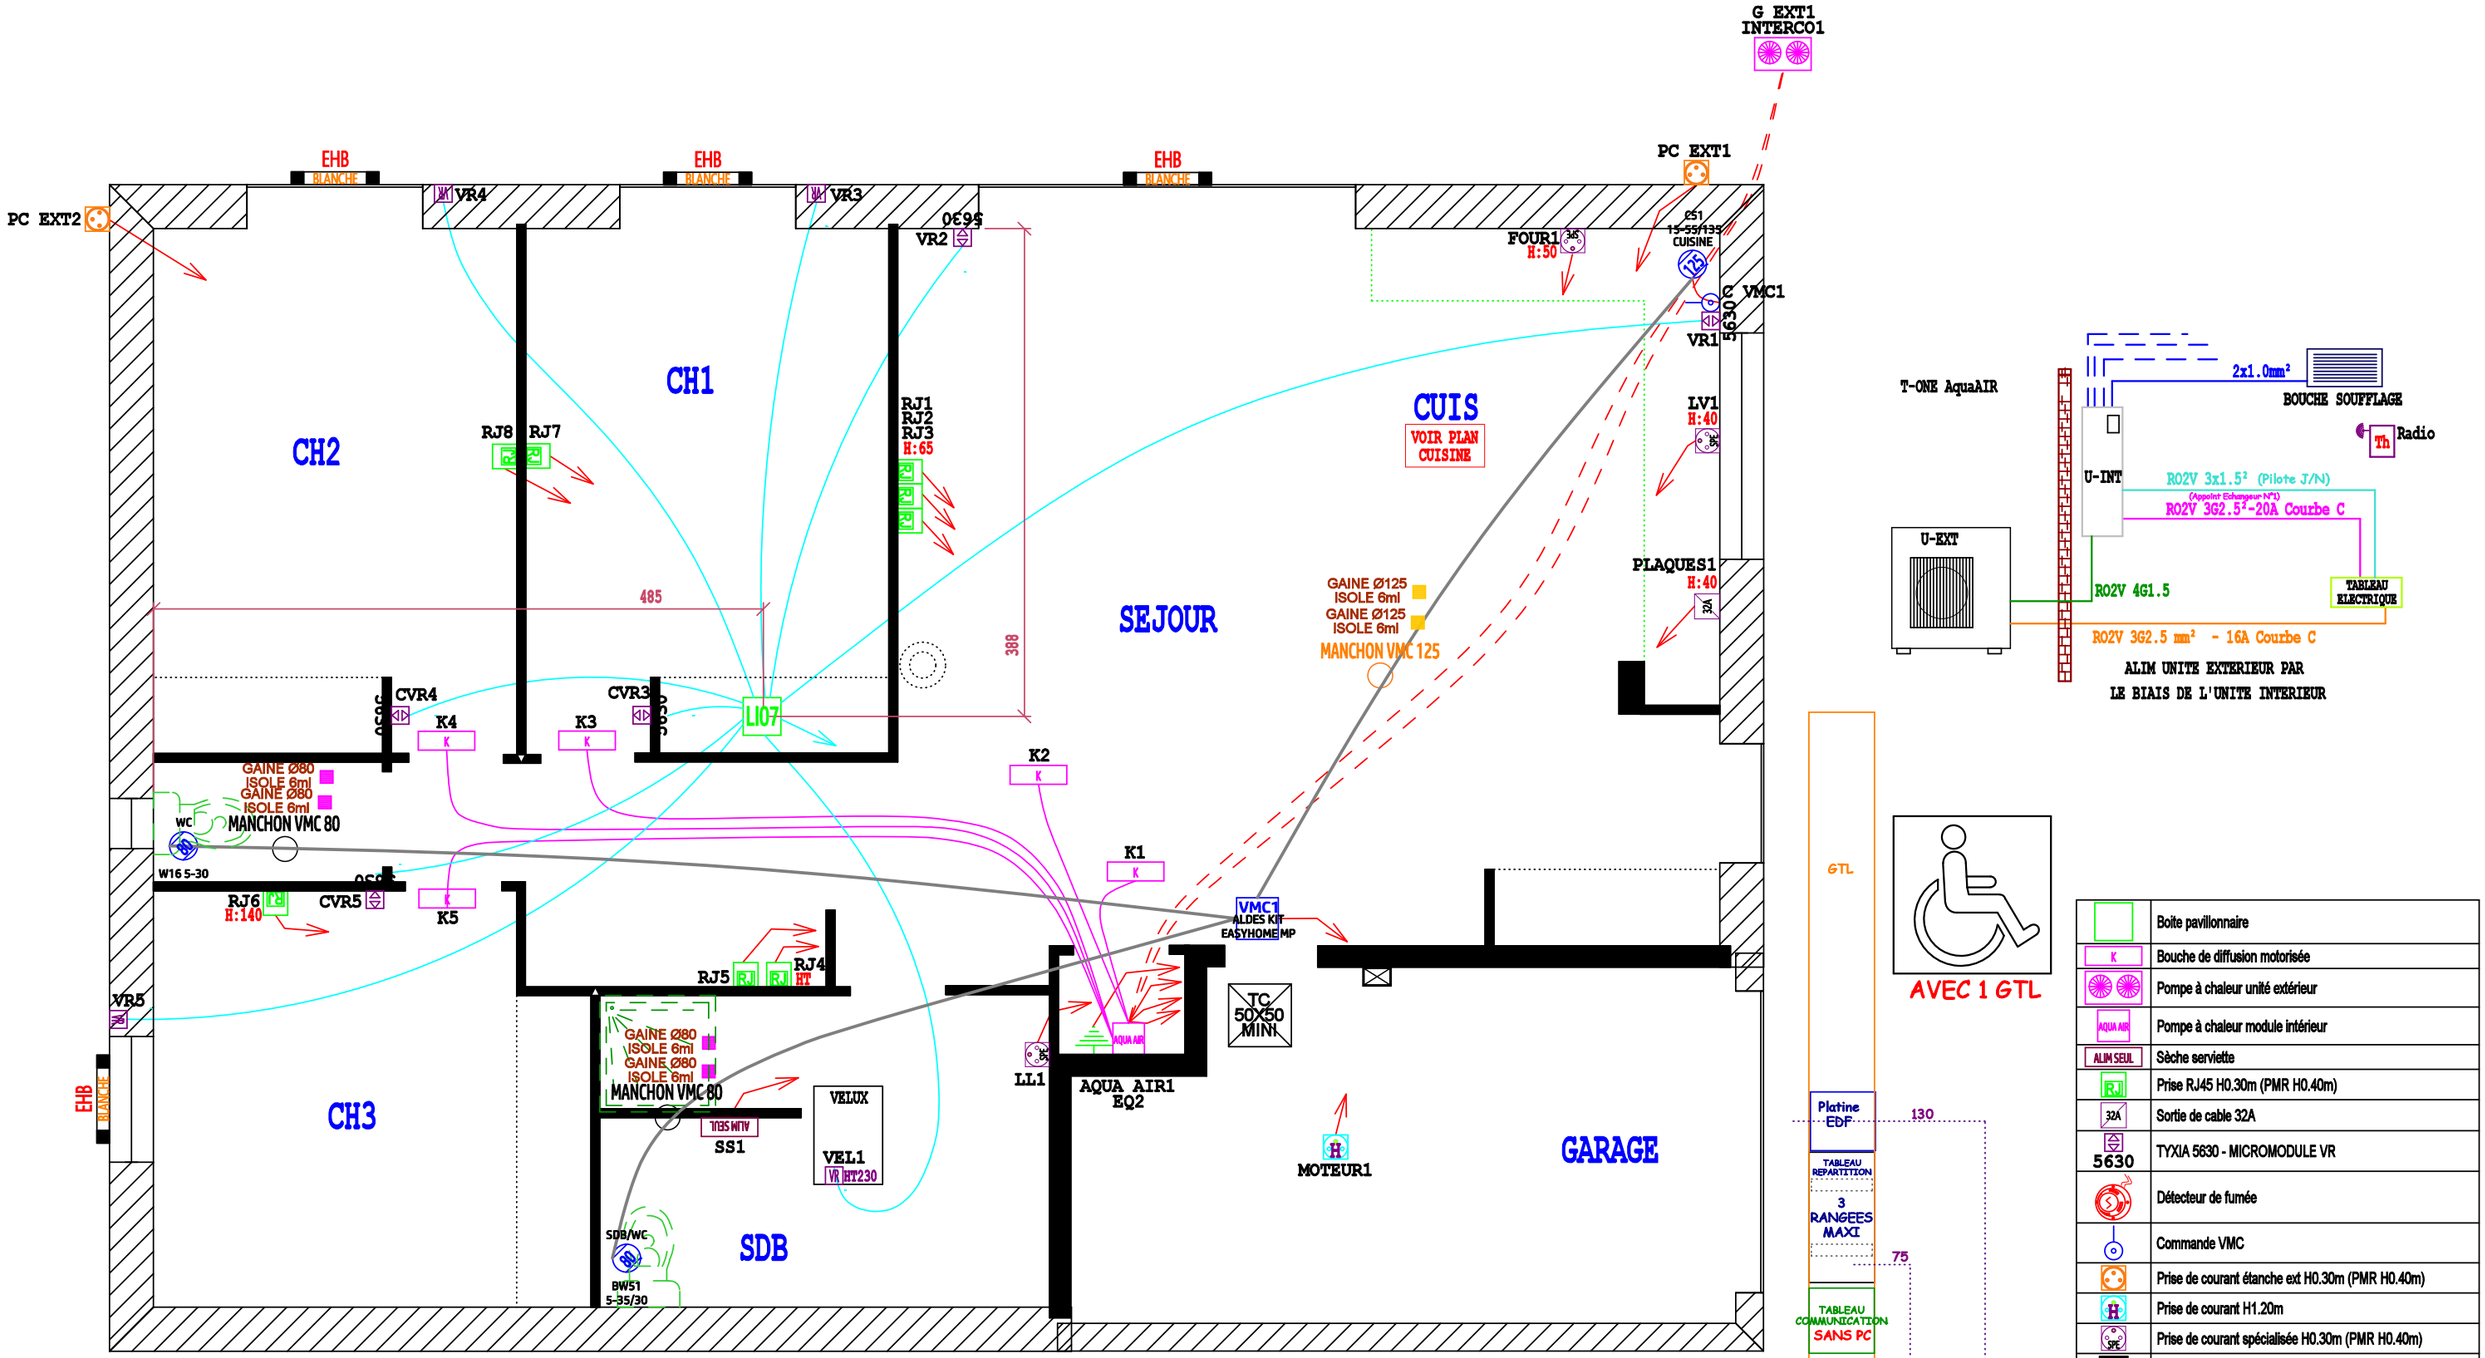

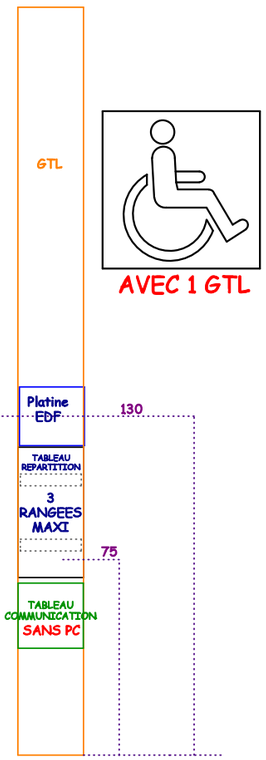

AVEC 1 GTL

	Boite pavillonnaire
K	Bouche de diffusion motorisée
	Pompe à chaleur unité extérieur
AQUA AIR	Pompe à chaleur module intérieur
ALIM SEUL	Sèche serviette
RJ	Prise RJ45 H0.30m (PMR H0.40m)
32A	Sortie de cable 32A
5630	TYXIA 5630 - MICROMODULE VR
	Détecteur de fumée
	Commande VMC
	Prise de courant étanche ext H0.30m (PMR H0.40m)
H	Prise de courant H1.20m
SPE	Prise de courant spécialisée H0.30m (PMR H0.40m)
	Renvoi de tableau
	Tableau de communication
	Prise de terre
VR	Obturateur


KiTéOHM pour une maison branchée


www.kiteohm.fr


Client	MAISONS LARA
Chantier	BATELIER JEAN LOUIS L51S078C
N°	AF26064644

Echelle : 1 / 50
Dess : mlaurent
Date : 07/10/2026

Les appareillages sont positionnés sur le plan à titre indicatif, ils doivent être installés en fonction des normes en vigueur.
Les hauteurs en cm sont données à titre indicatif, suivre les valeurs indiquées sur le plan .
⚠ Les hauteurs sont données à partir du sol fini ! ⚠

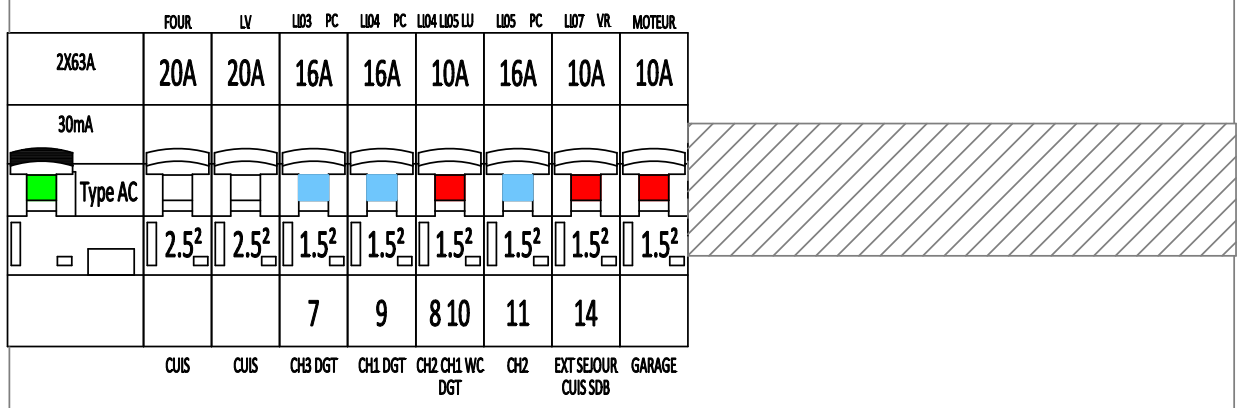

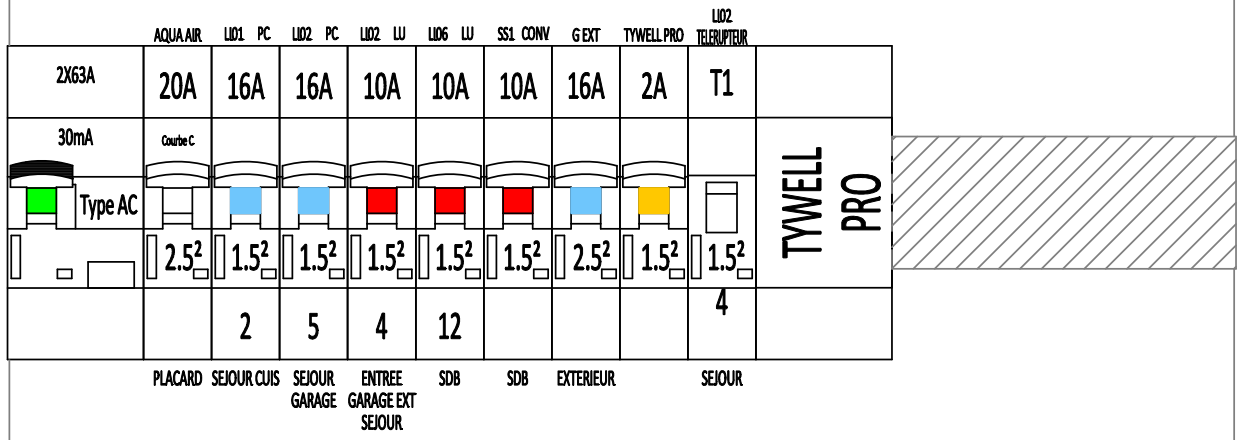

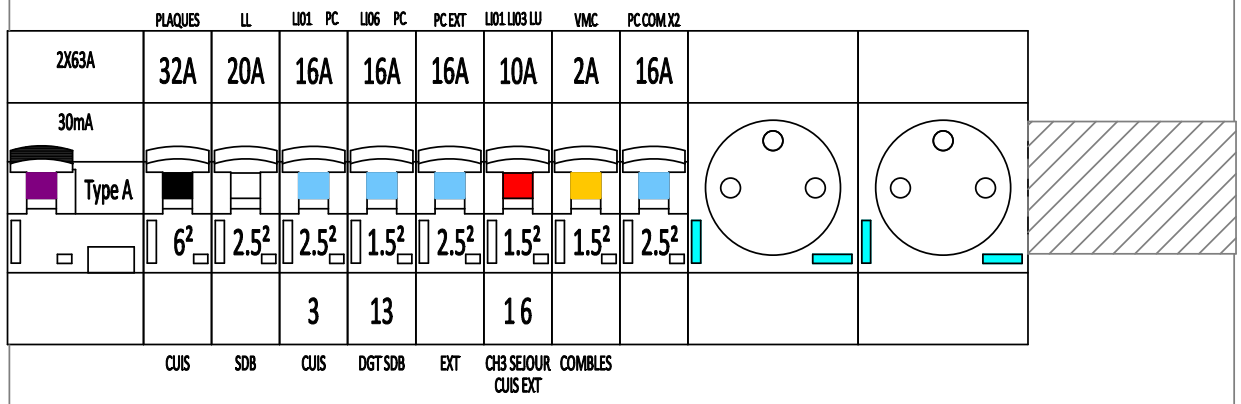

BOUCHON		
x16	x20	x25

TORES
CH ☐ CE ☐ PC ☐

TYPE CHAUFFAGE

TYPE ECS

CHAUFFAGE ELECTRIQUE

REPERE	TYPE D'APPAREIL	PIECE DESERVIE
CVR3	5630	CH1
CVR4	5630	CH2
CVR5	5630	CH3
VR1	5630	CUIS
VR2	5630	SEJOUR

FOND

KiTēOHM pour une maison branchée

www.kiteohm.fr

Client	MAISONS LARA	Echelle :	1 / 2
Chantier	BATELIER JEAN LOUIS L51S078C	Dess :	mlaurent
N°	AF26064644	Date:	07/10/2026

PROG TABLEAU/CHANTIER	X		
CONNECTEURS / WAGOS			
LEGRAND		18 MODULES	
		MONOPHASE	X
GTL	X	TRIPHASE	
PORTE		FOND	
BORNIER DE TERRE SUP			

MAISONS LARA
BATELIER JEAN LOUIS L51S078C
AF26064644

Nb MODULES:

PORTE	
REF : _____	
CONTACTEUR CE NBRE:	
BOUCHON x16 x20 x25	
DMT AVEC WAGGOS	
DMT SANS WAGGOS	
MONOPHASE	
TRIPHASE	
DISJONCTEUR REF : _____	

TORES
CH ☐ CE ☐ PC ☐

TYPE CHAUFFAGE

TYPE ECS

REPERE	TYPE D'APPAREIL	PIECE DESERVIE

