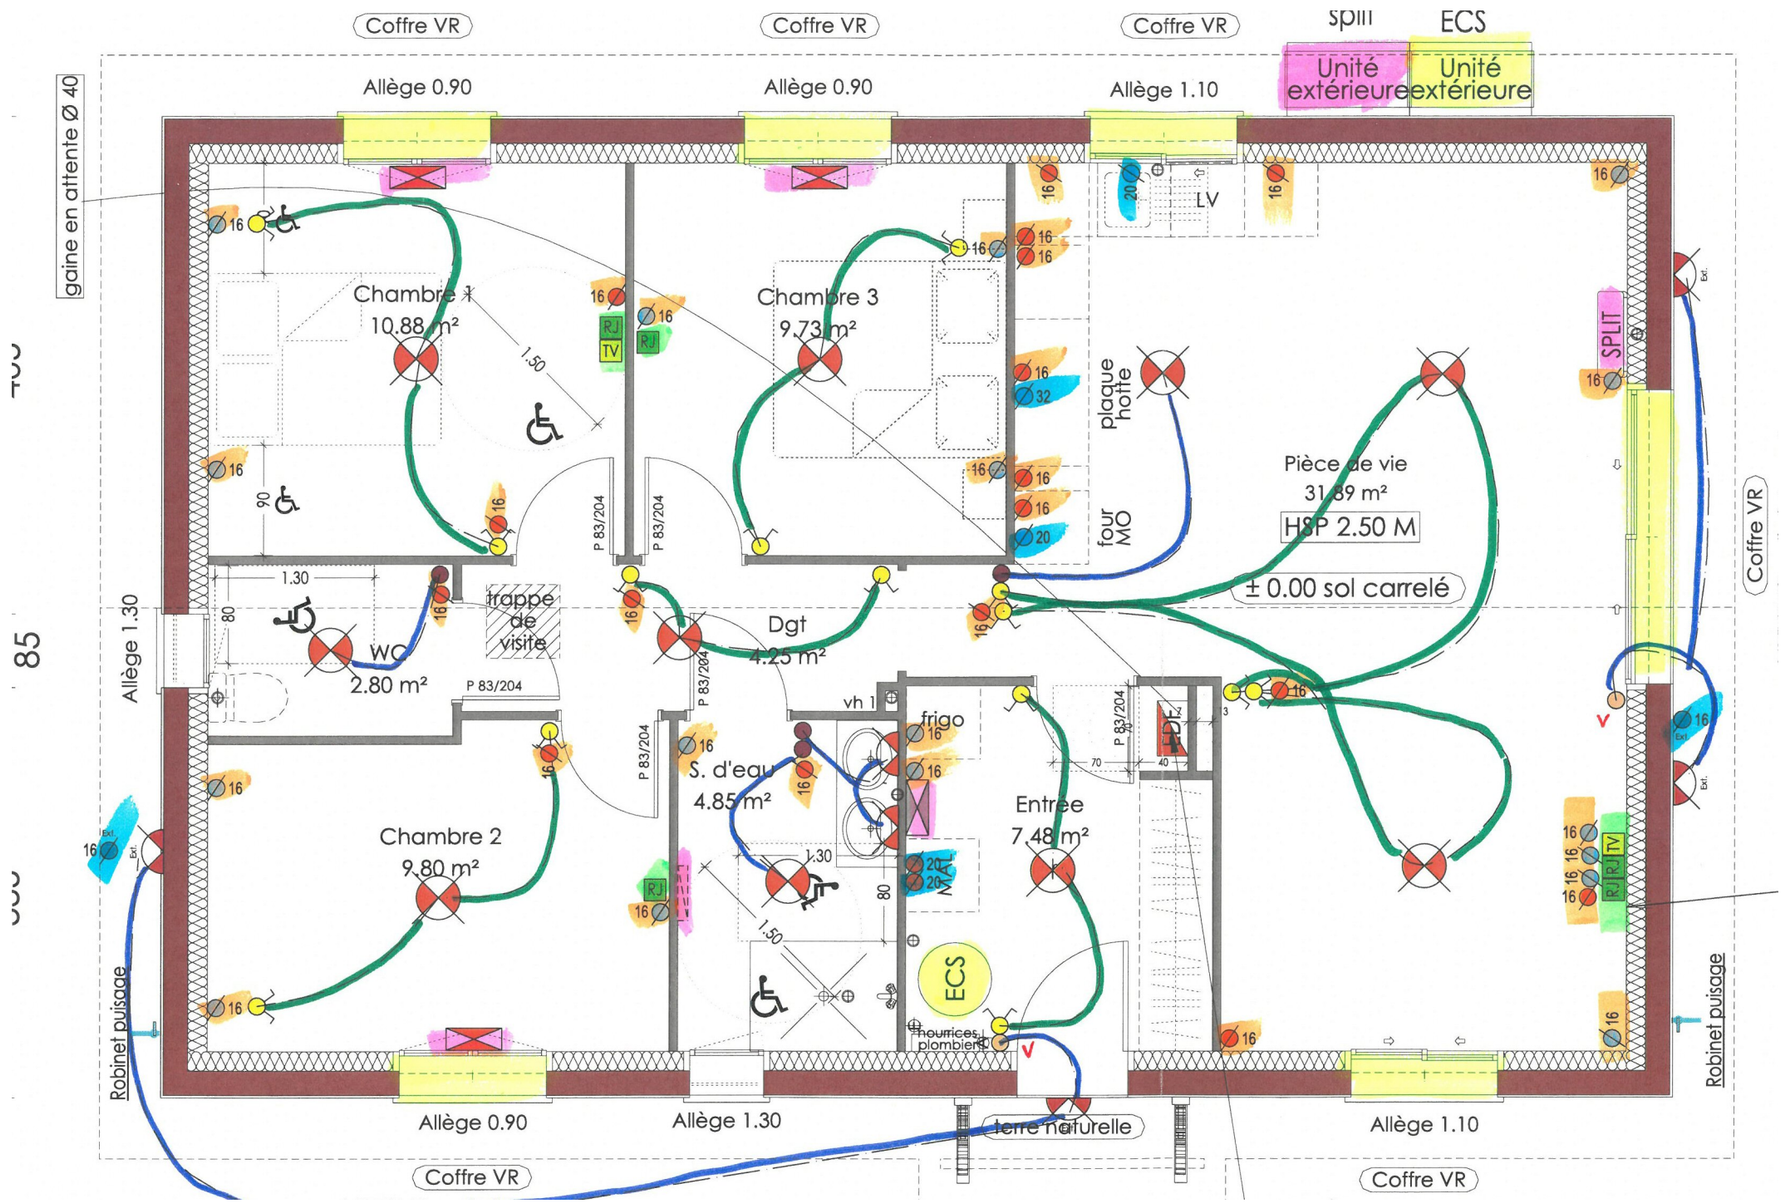



KiTēOHM pour une maison branchée	www.kiteohm.fr	Client	IMMO CONSTRUCTION	Echelle : 1 / 1
		Chantier	DUCOURNEAU	Dess : mlaurent
		N°	AF26075150	Date : 16/10/2026


Les appareillages sont positionnés sur le plan à titre indicatif, ils doivent être installés en fonction des normes en vigueur.
Les hauteurs en cm sont données à titre indicatif, suivre les valeurs indiquées sur le plan .
⚠ Les hauteurs sont données à partir du sol fini ! ⚠

	Boite pavillonnaire
	Alimentation
	Interrupteur double allumage
	Interrupteur double Va-et-Vient
	Interrupteur simple allumage
	Interrupteur simple allumage lumineux
	Interrupteur Va-et-Vient
	Plaque double Horizontale

	Plaque double Verticale
	Plaque triple Horizontale
	Plaque triple Verticale
	Applique étanche
	Applique murale salle de bain
	Point lumineux
	Prise de courant H0.30m (PMR H0.40m)
	Prise de courant 2.5² H1.20m
	Prise de courant H1.20m

	Prise de courant Hotte
	Tableau d'alimentation générale basse tension
	Liaison équipotentielle

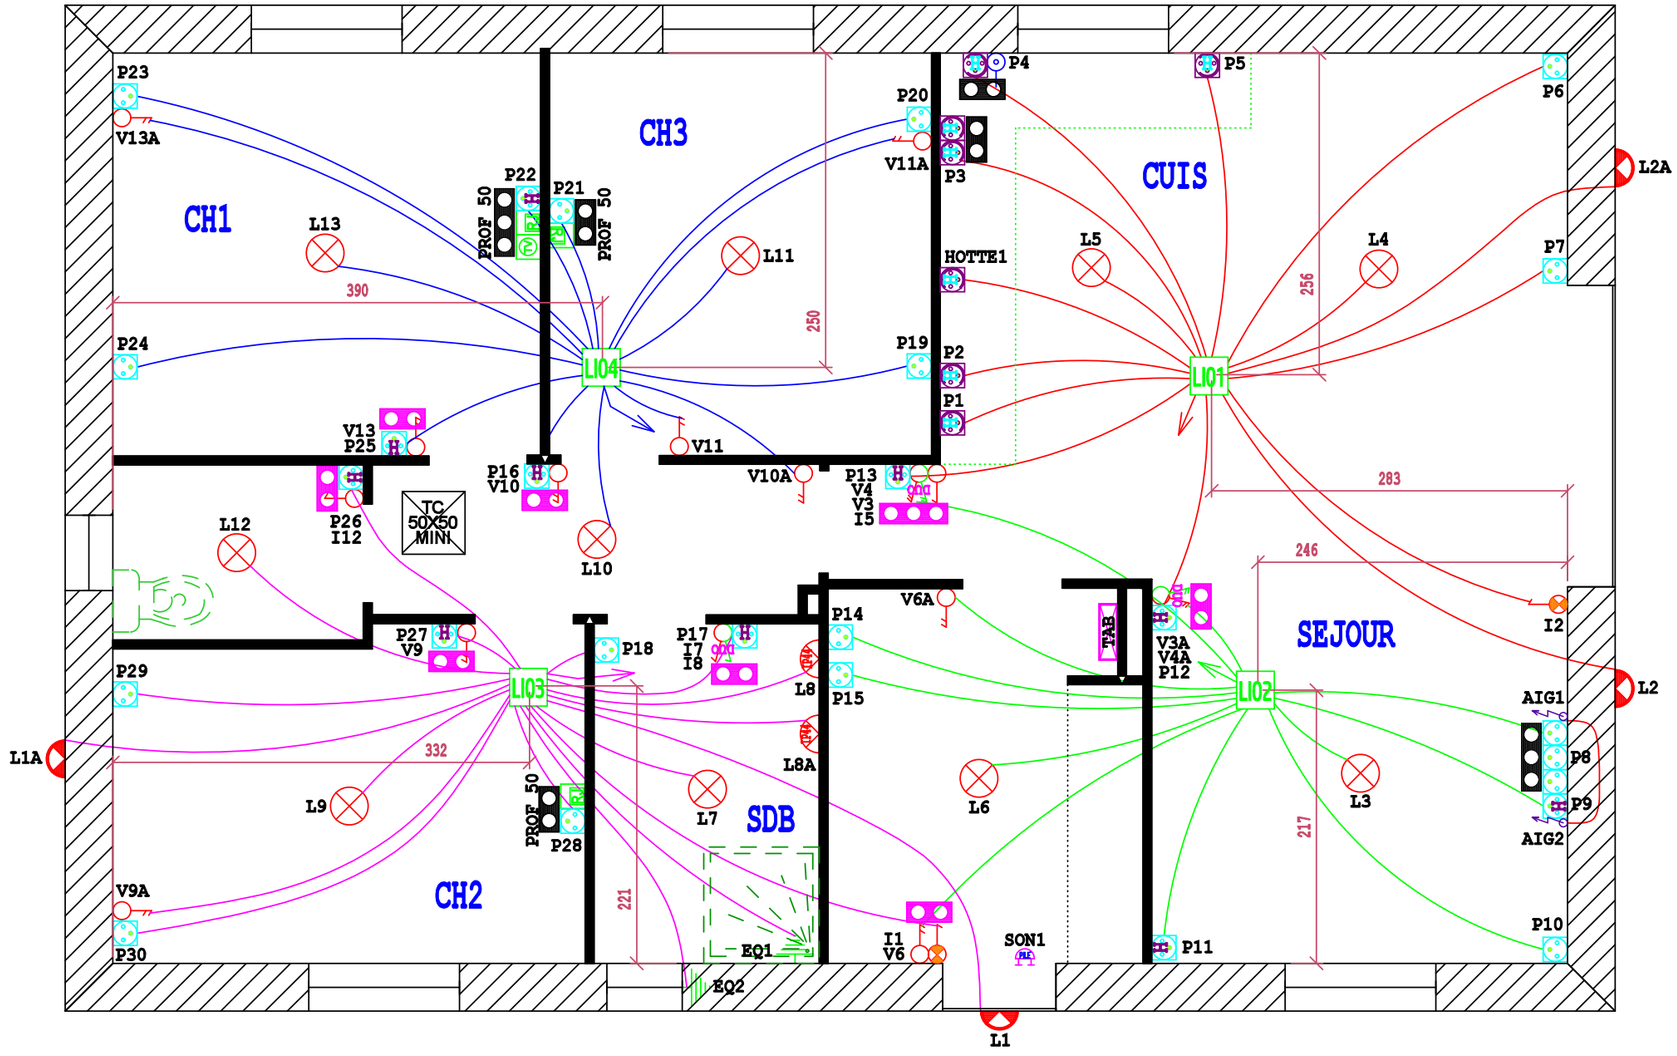

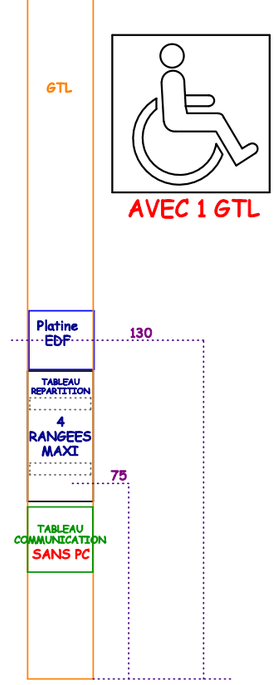

KiTēOHM pour une maison branchée

www.kiteohm.fr

Client	IMMO CONSTRUCTION
Chantier	DUCOURNEAU
N°	AF26075150

Echelle : 1 / 50

Dess : mlaurent

Date : 16/10/2026

Les appareillages sont positionnés sur le plan à titre indicatif, ils doivent être installés en fonction des normes en vigueur.
Les hauteurs en cm sont données à titre indicatif, suivre les valeurs indiquées sur le plan .
⚠ Les hauteurs sont données à partir du sol fini ! ⚠

DFUM1

CONNECT D'EVACUATION


TRI GEN


REPARTITEUR TV 2 SORTIES

CABLETTE1

TYWELL PRO +CONTROL

	Boite pavillonnaire		Piquette de terre 1ml
CE SPLIT	Chauffe-eau électrique split		Prise de terre
CLIM	Climatisation	VR HT230	Obturateur
ALIM SEUL	Convecteur de chauffage rayonnant		
	Pompe à chaleur unité extérieur		
ALIM SEUL	Sèche serviette		
ATTENTE TV EN COMBLE	Antenne TV H comble		
RJ	Prise RJ45 H0.30m (PMR H0.40m)		
TV	Prise télévision H0.30m (PMR H0.40m)		
32A	Sortie de cable 32A		
	Détecteur de fumée		
	Commande VMC		
	Plaque double Horizontale		
	Plaque triple Horizontale		
	Prise de courant étanche ext H0.30m (PMR H0.40m)		
SPE	Prise de courant spécialisée H0.30m (PMR H0.40m)		
	Renvoi de tableau		
	Tableau de communication		

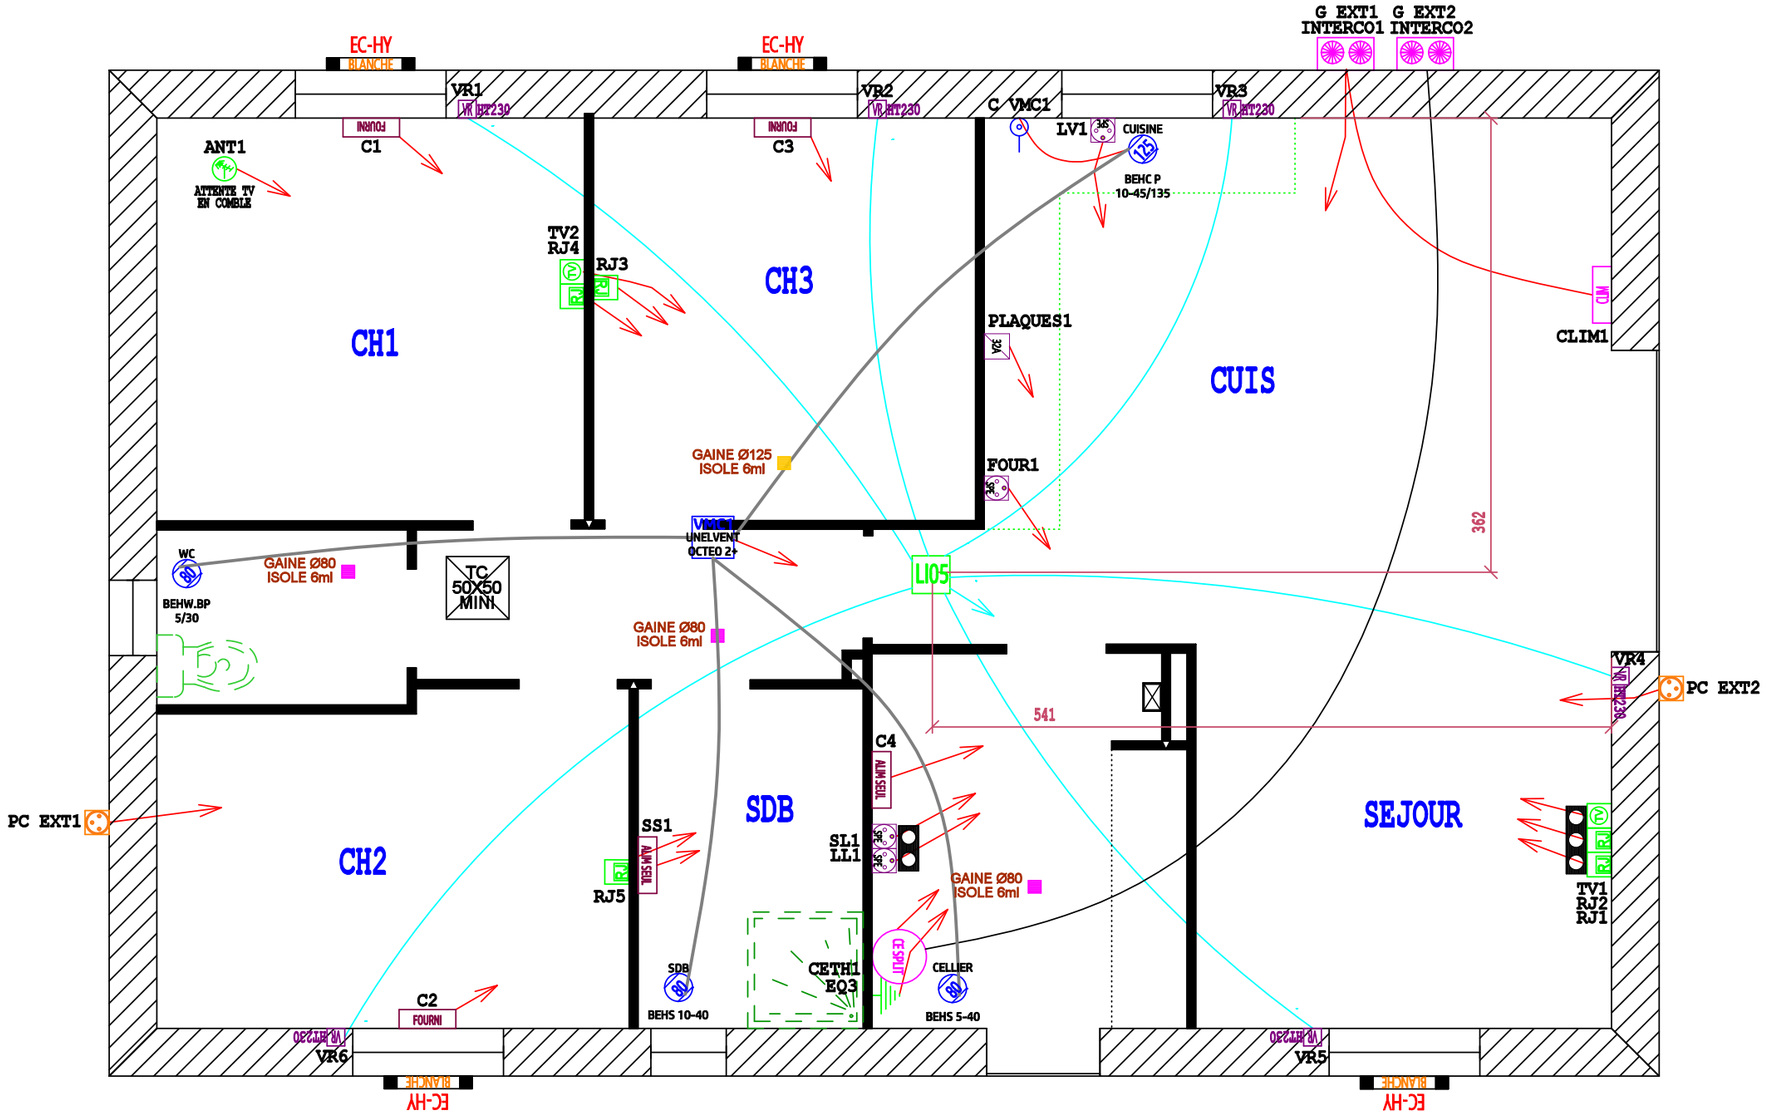

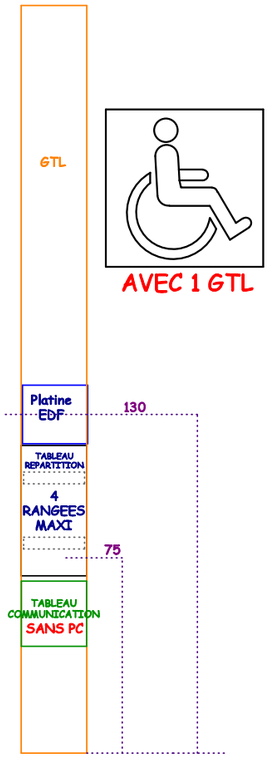


KiTēOHM pour une maison branchée	www.kiteohm.fr	Client	IMMO CONSTRUCTION
		Chantier	DUCOURNEAU
		N°	AF26075150

Echelle : 1 / 50

Dess : mlaurent

Date : 16/10/2026

Les appareillages sont positionnés sur le plan à titre indicatif, ils doivent être installés en fonction des normes en vigueur.
Les hauteurs en cm sont données à titre indicatif, suivre les valeurs indiquées sur le plan .
⚠ Les hauteurs sont données à partir du sol fini ! ⚠

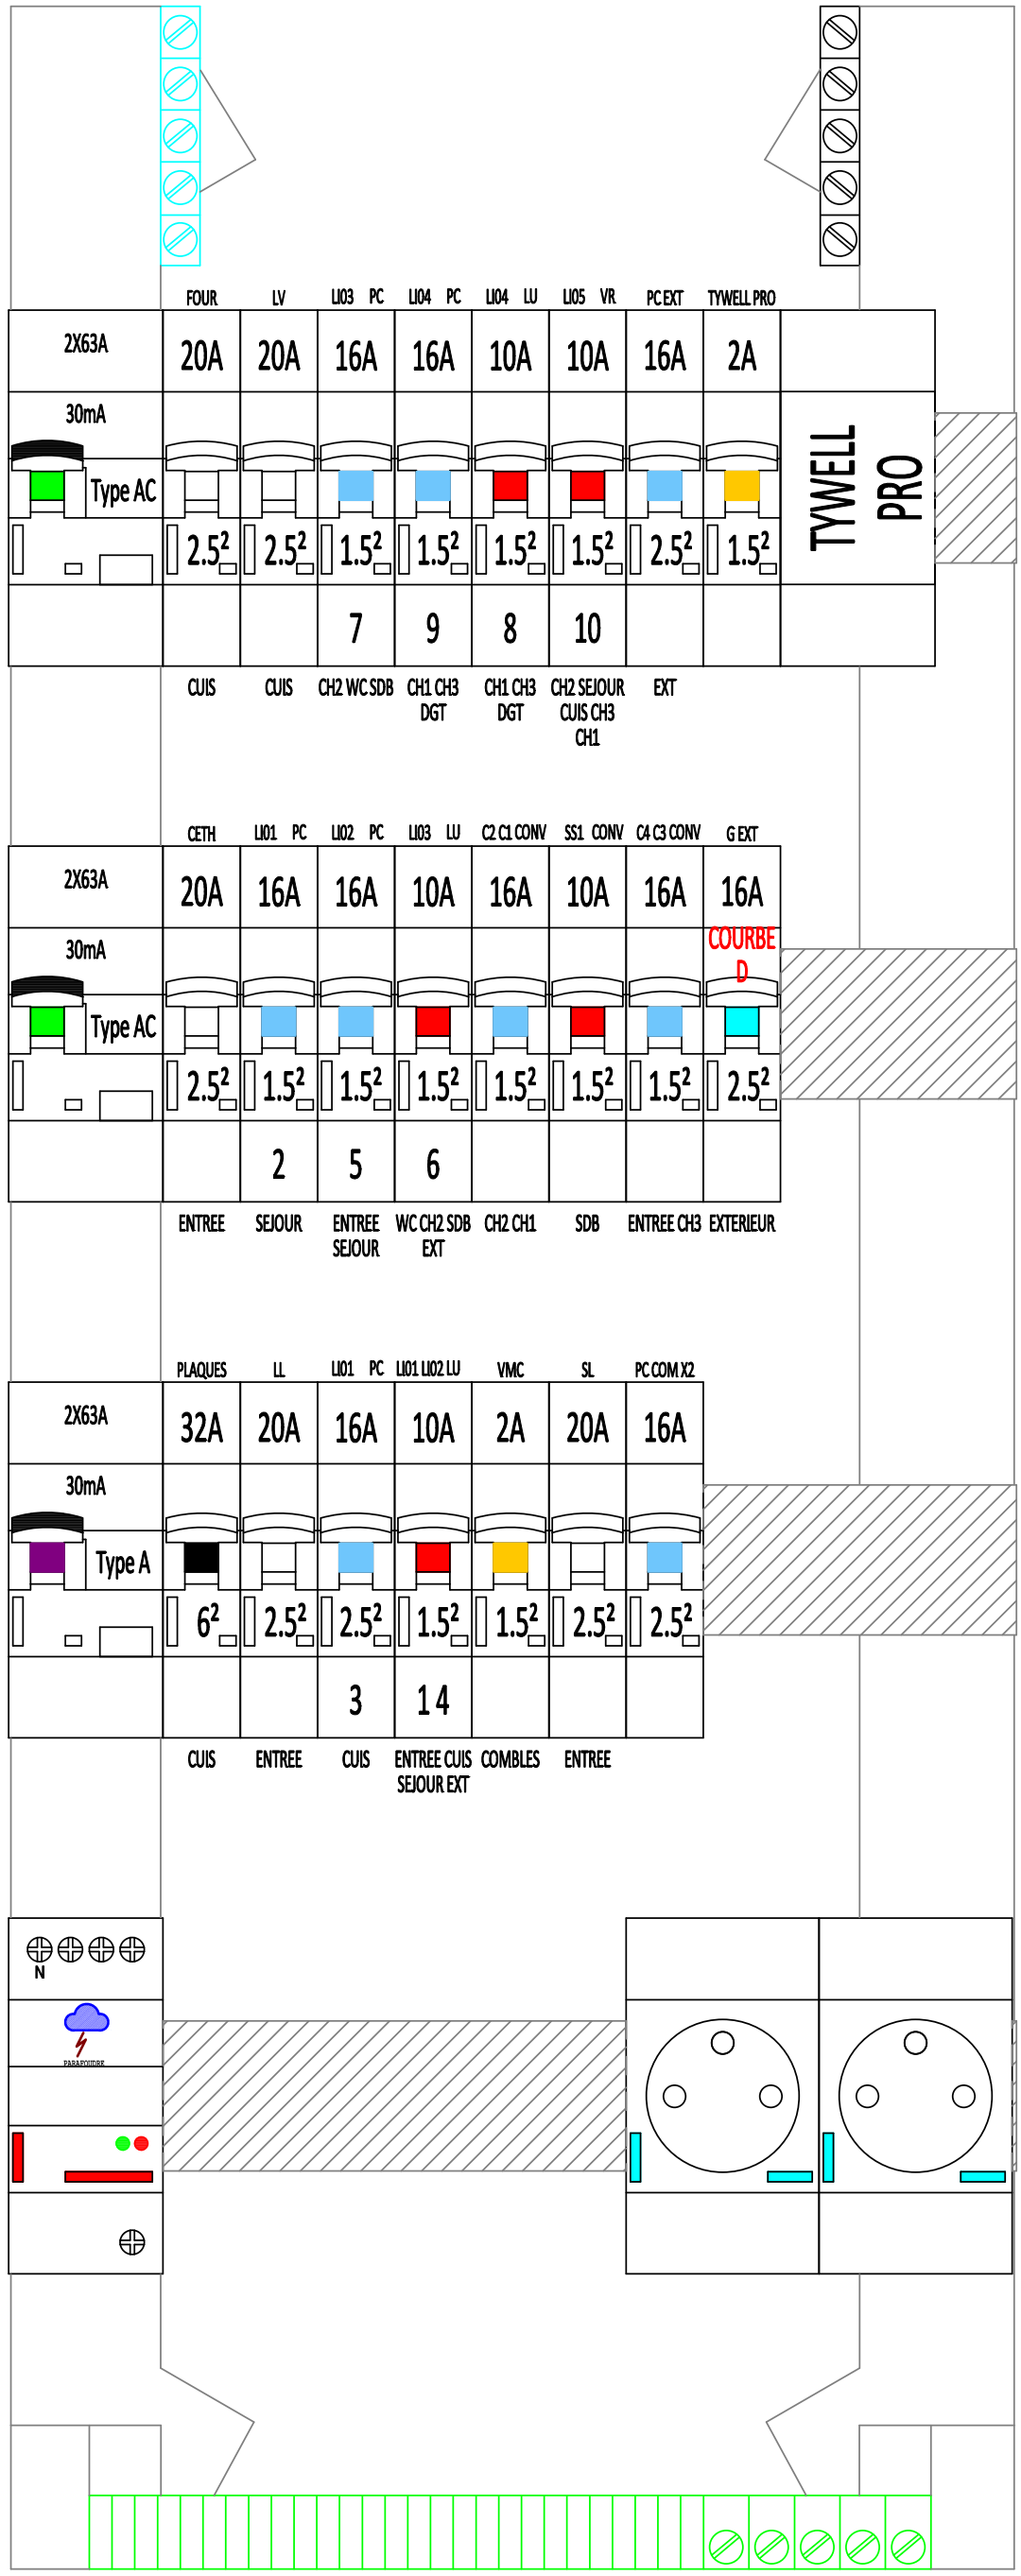

BOUCHON		
x16	x20	x25

TORES
CH ☐ CE ☐ PC ☐

TYPE CHAUFFAGE

TYPE ECS

CHAUFFAGE ELECTRIQUE

REPERE	TYPE D'APPAREIL	PIECE DESERVIE

PROG TABLEAU/CHANTIER			X
CONNECTEURS / WAGOS			
SCHNEIDER		13 MODULES	
		MONOPHASE	X
GTL	X	TRIPHASE	
PORTE		FOND	
BORNIER DE TERRE SUP			

KiTēOHM pour une maison branchée

www.kiteohm.fr

FOND

Client	IMMO CONSTRUCTION
Chantier	DUCOURNEAU
N°	AF26075150

Echelle : 1 / 1.6
Dess : mlaurent
Date: 16/10/2026

IMMO CONSTRUCTION DUCOURNEAU
AF26075150

Nb MODULES:

PORTE	
REF : _____	
CONTACTEUR CE NBRE:	
BOUCHON x16 x20 x25	
DMT AVEC WAGGOS	
DMT SANS WAGGOS	
MONOPHASE	
TRIPHASE	
DISJONCTEUR REF : _____	

TORES
CH ☐ CE ☐ PC ☐

TYPE CHAUFFAGE

TYPE ECS

REPERE	TYPE D'APPAREIL	PIECE DESSERVIE

