
	Boite pavillonnaire		Interrupteur simple allumage lumineux		Plaque double Verticale		Prise de courant 2.5² H1.20m
	Bouton poussoir		Interrupteur Va-et-Vient		Plaque triple Horizontale		Prise de courant étanche H0.30m (PMR H0.40m)
DUO	Interrupteur double allumage	DUO	Interrupteur Va-et-Vient + Bouton poussoir		Applique étanche		Prise de courant H1.20m
	Interrupteur simple allumage		Interrupteur Va-et-Vient lumineux		Applique murale		Prise de courant Hotte
DUO	Interrupteur simple allumage + Bouton poussoir		Plaque double Horizontale		Point lumineux		Tableau d'alimentation générale basse tension
					Prise de courant H0.30m (PMR H0.40m)		Liaison équipotentielle
					Prise de courant 2.5² H0.30m (PMR H0.40m)		

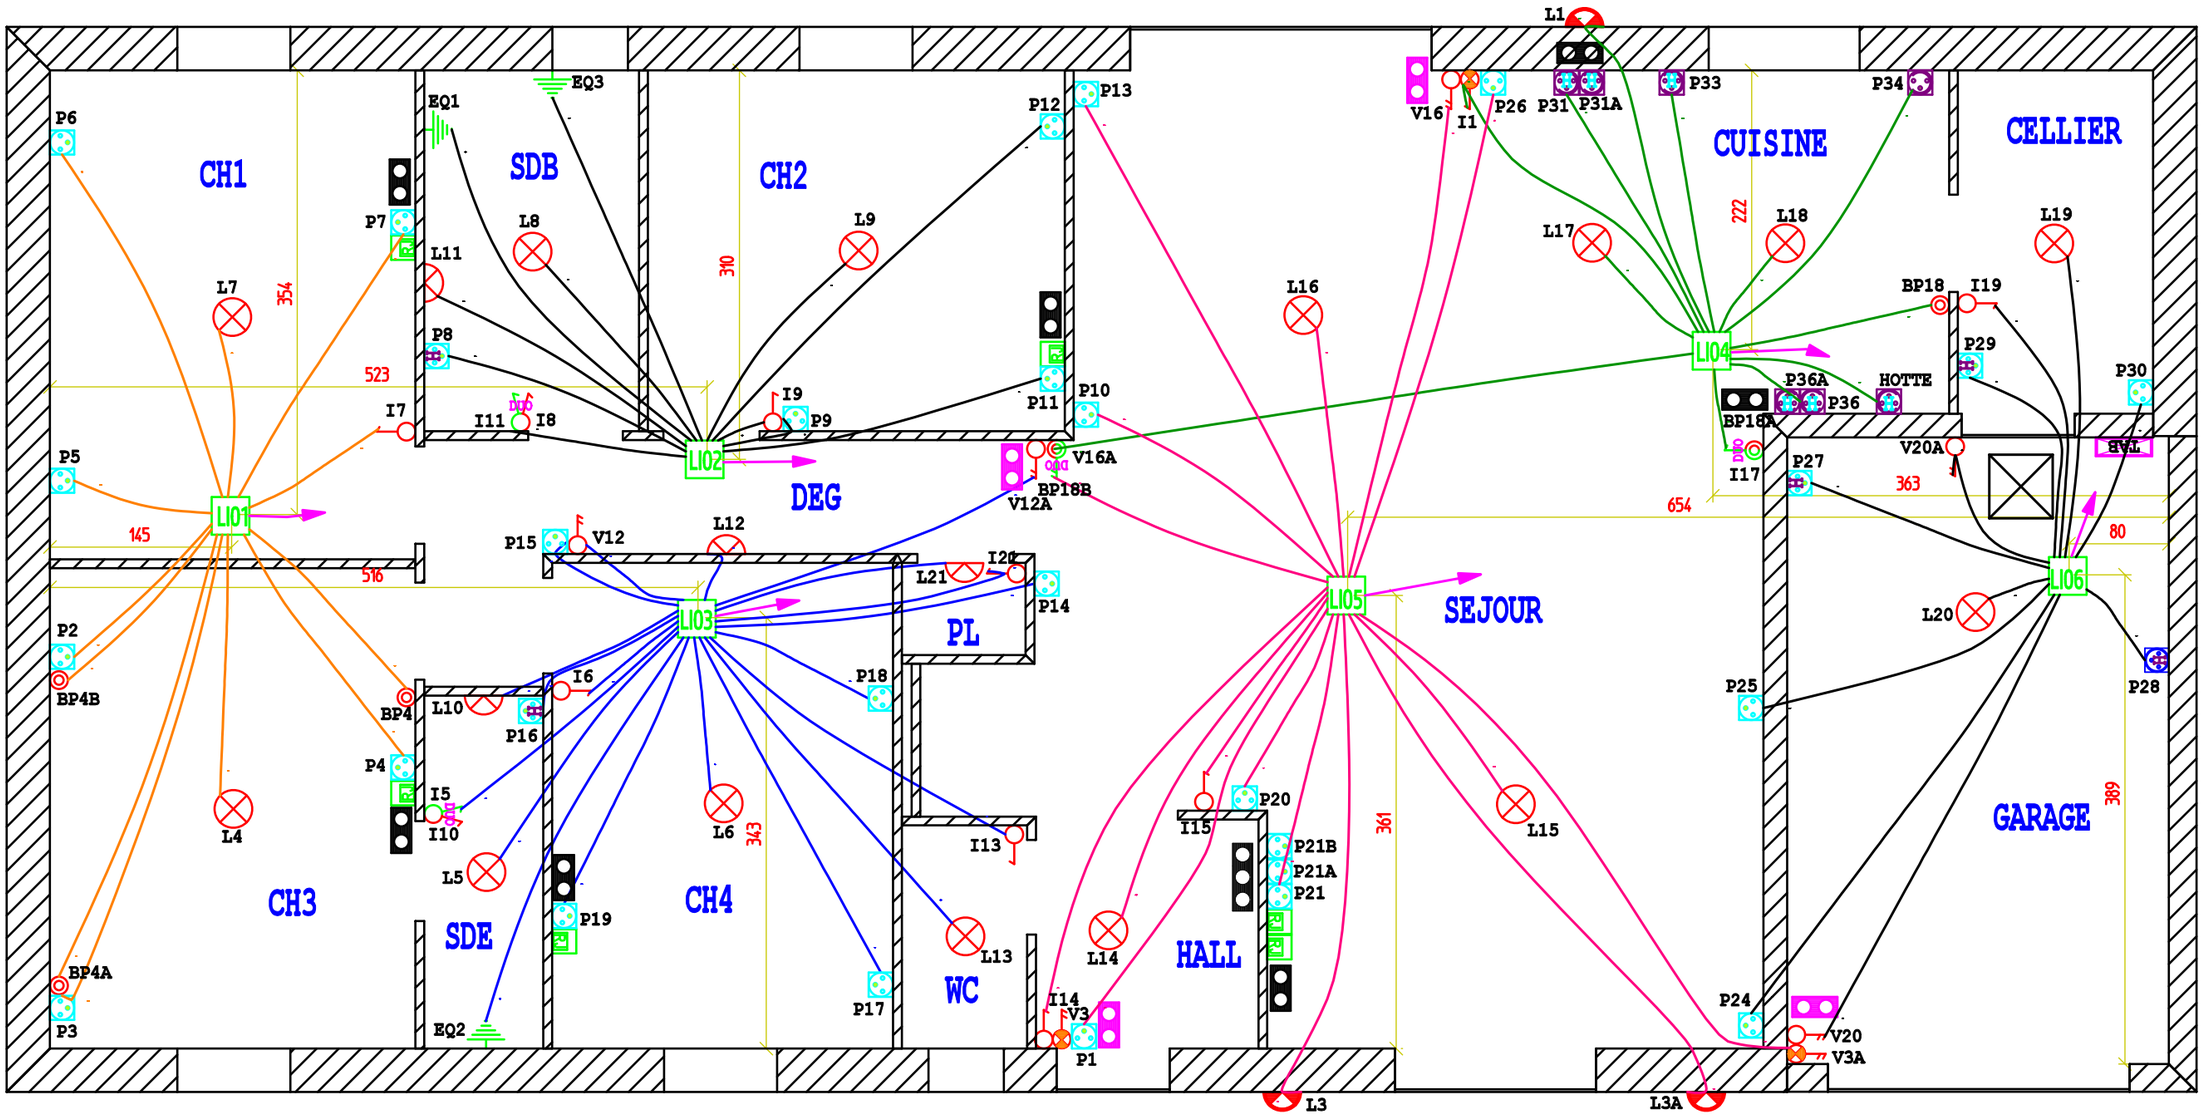



KiTēOHM pour une maison branchée	www.kiteohm.fr	Client	ALPHA CONSTRUCTIONS	Echelle : 1 / 50
		Chantier	FALGUA E6390	Dess : s.tarnaud
		N°	AF26064297	Date : 06/07/2026

Les appareillages sont positionnés sur le plan à titre indicatif, ils doivent être installés en fonction des normes en vigueur.
Les hauteurs en cm sont données à titre indicatif, suivre les valeurs indiquées sur le plan .
⚠ Les hauteurs sont données à partir du sol fini ! ⚠

	Boite pavillonnaire
K	Bouche de diffusion motorisée
	Pompe à chaleur unité extérieur
AQUA AIR	Pompe à chaleur module intérieur
FOURNI	Sèche serviette
RJ	Prise RJ45 H0.30m (PMR H0.40m)
32A	Sortie de cable 32A

	Interrupteur volet roulant connecté
	Commande VMC
	Prise de courant étanche ext H0.30m (PMR H0.40m)
	Prise de courant H1.20m
SPE	Prise de courant spécialisée H0.30m (PMR H0.40m)
	Renvoi de tableau
	Prise de terre

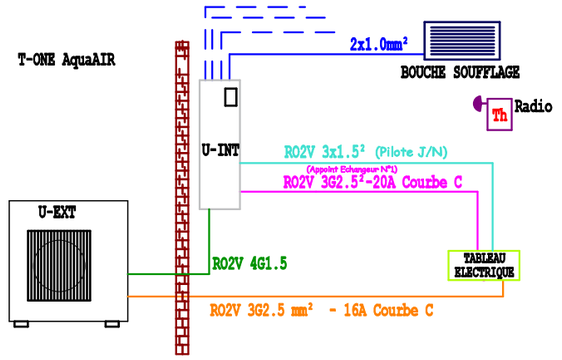


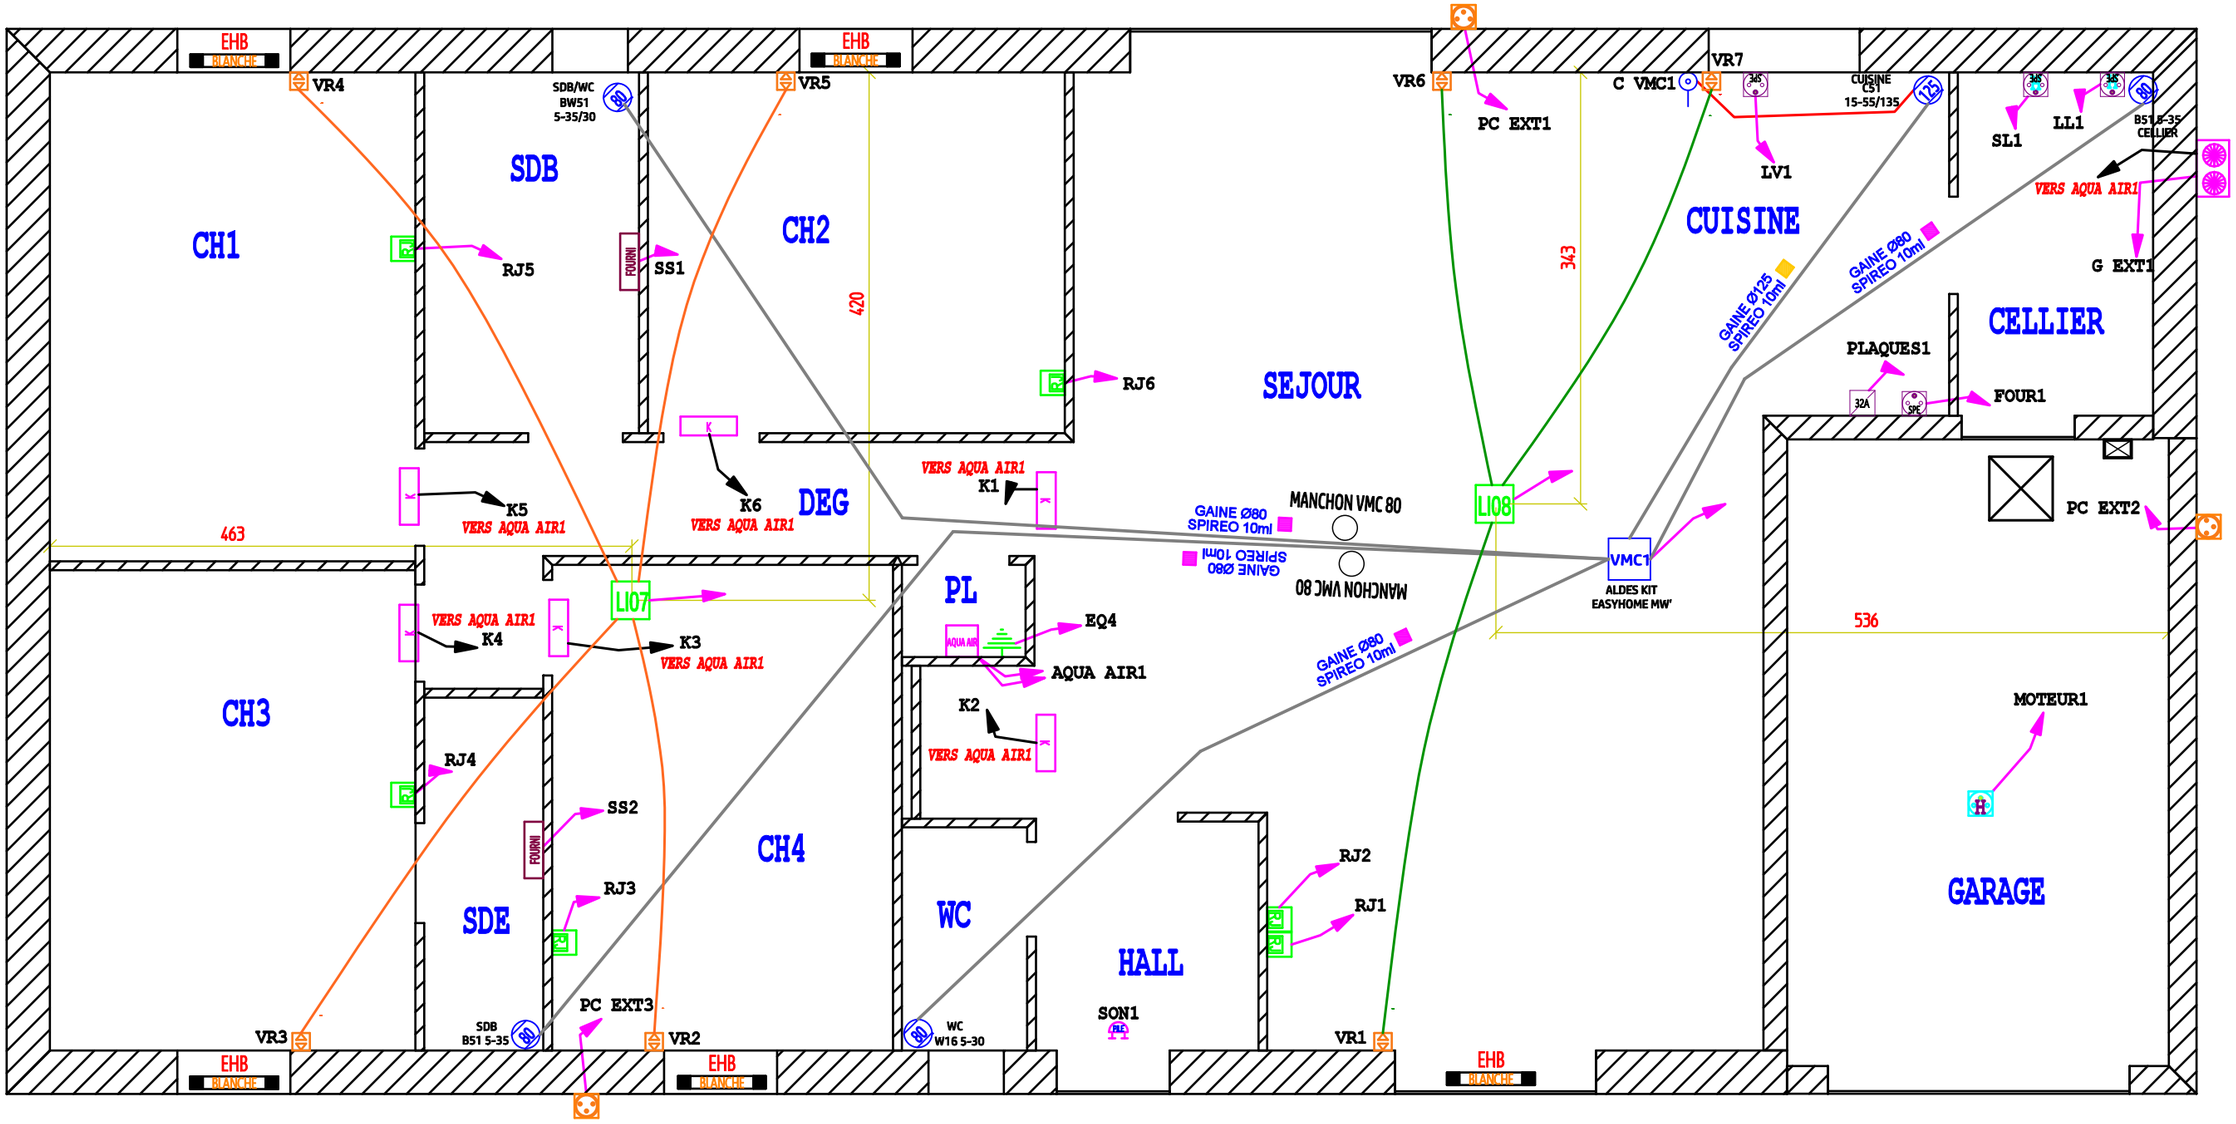



KiTēOHM pour une maison branchée	www.kiteohm.fr	Client	ALPHA CONSTRUCTIONS
		Chantier	FALGUA E6390
		N°	AF26064297

Echelle : 1 / 50
Dess : s.tarnaud
Date : 06/07/2026

Les appareillages sont positionnés sur le plan à titre indicatif, ils doivent être installés en fonction des normes en vigueur.
Les hauteurs en cm sont données à titre indicatif, suivre les valeurs indiquées sur le plan .
⚠ Les hauteurs sont données à partir du sol fini ! ⚠

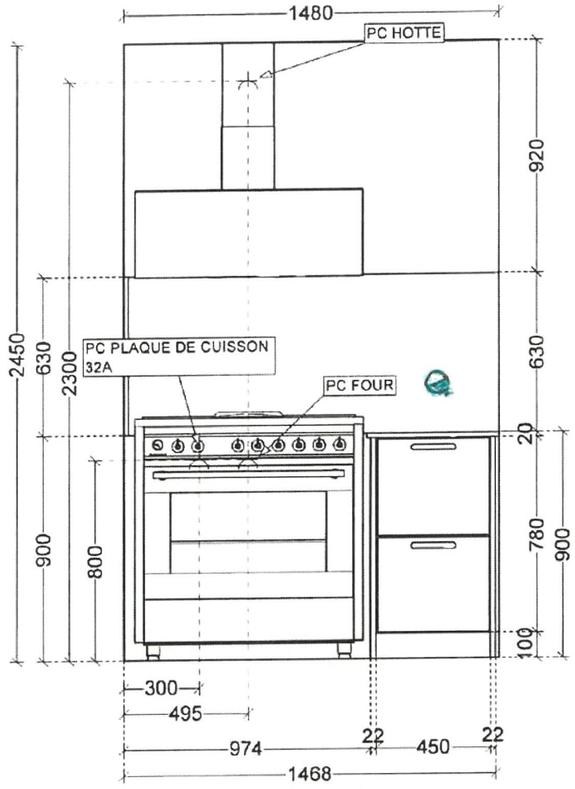

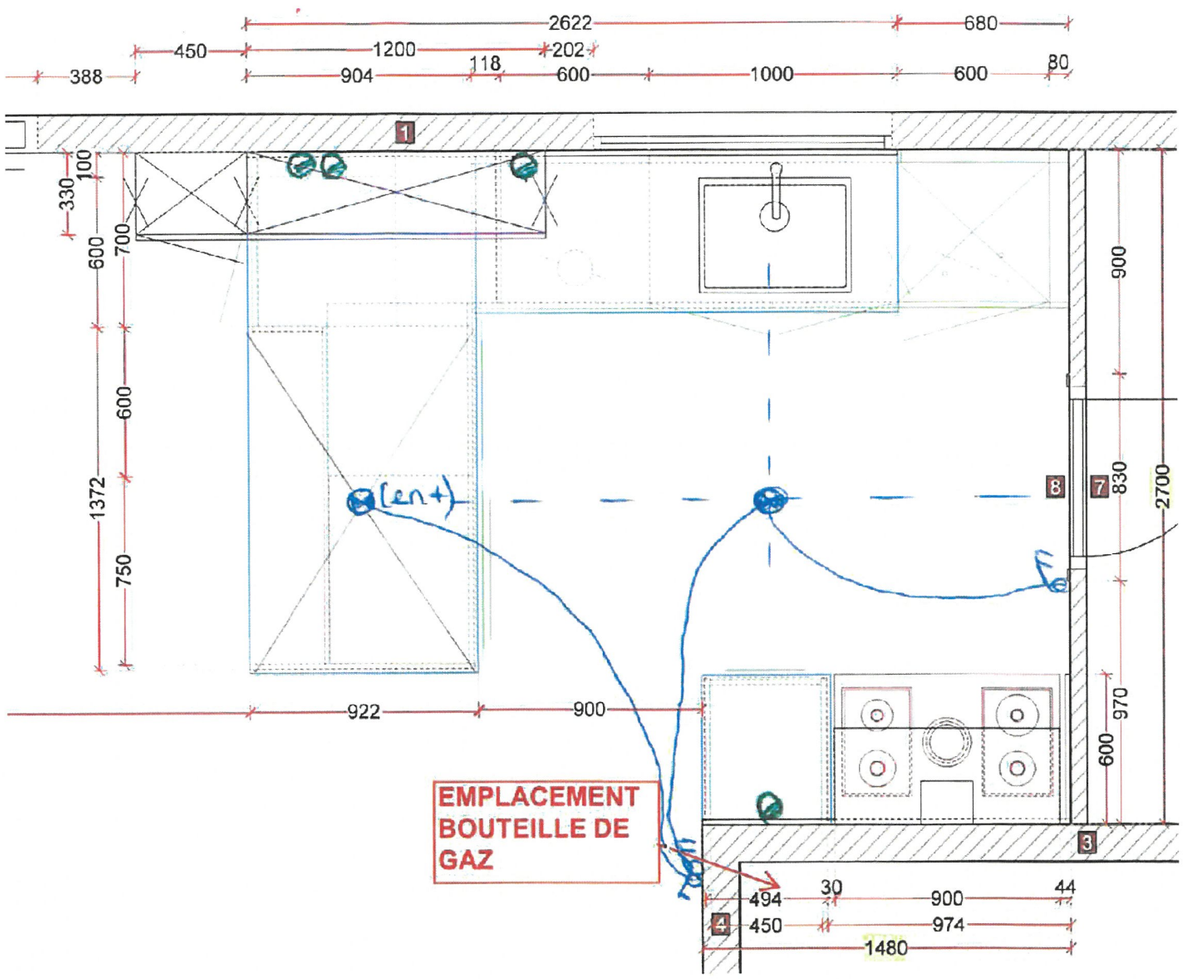

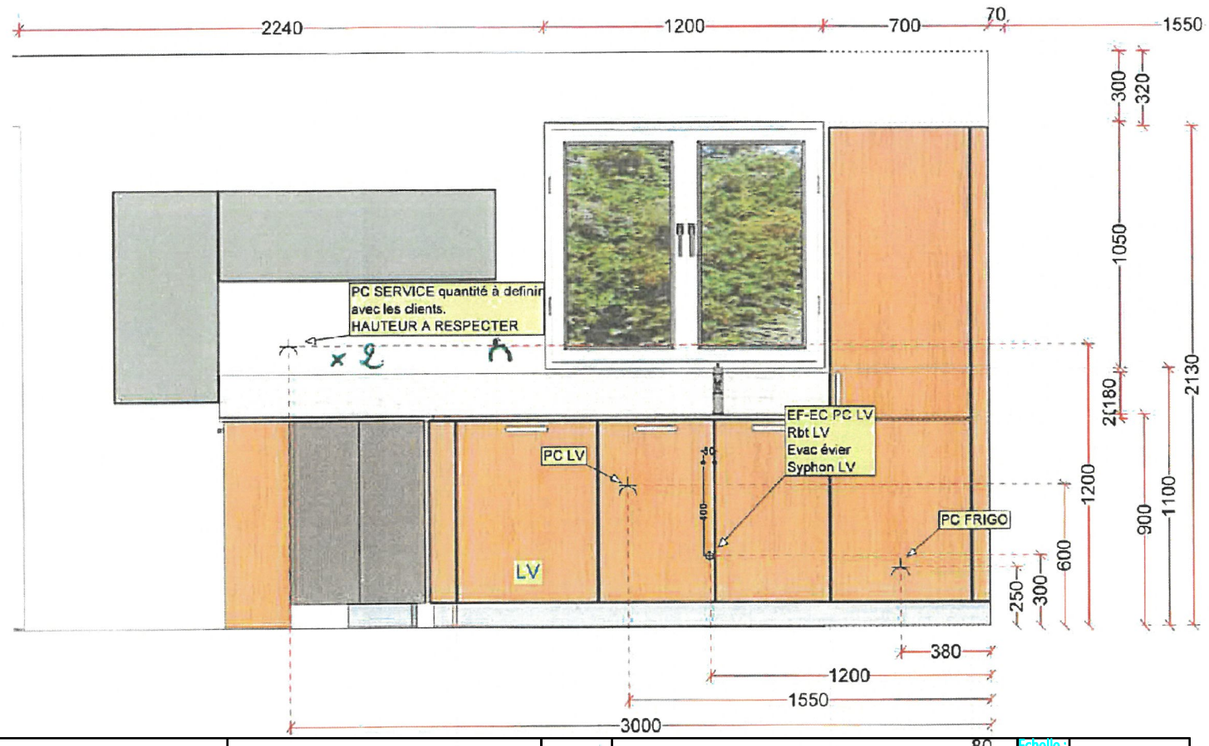

388 450 1022 600 3752 100 80

KiTeOHM pour une maison branchée

www.kiteohm.fr

Client	ALPHA CONSTRUCTIONS
Chantier	FALGUA E6390
N°	AF26064297

Echelle : 1 / 50
Dess : s.tarnaud
Date : 06/07/2026

CONSTRUCTION D'UNE MAISON INDIVIDUELLE

Maitre d'Ouvrage : M. & Mme FALGUA

PLAN de CUISINE

Echelle :

Date : 13/04/2026

09.1 TVX

E6390

RE 2020


Adresse Chantier : LOT 1 - ROUTE DE JEAN DE L'OUILLE - 33590 TALAIS

Les appareillages sont positionnés sur le plan à titre indicatif, ils doivent être installés en fonction des normes en vigueur.
Les hauteurs en cm sont données à titre indicatif, suivre les valeurs indiquées sur le plan .
⚠ Les hauteurs sont données à partir du sol fini ! ⚠

WISER
FIL NEUTRE

LEGENDE ELECTRIQUE

ALIM ELEC VR		ALIM HOTTE	
INTER SA		SONNETTE	
INTER VV		TABLEAU EDF	EDF
TELERUPTEUR		CARILLON	
PC 16A		APPLIQUE	
PC 20A		POINT CENTRAL	
PC 32A		ALIM CHAUFFAGE	
P TV			
P RJ45			

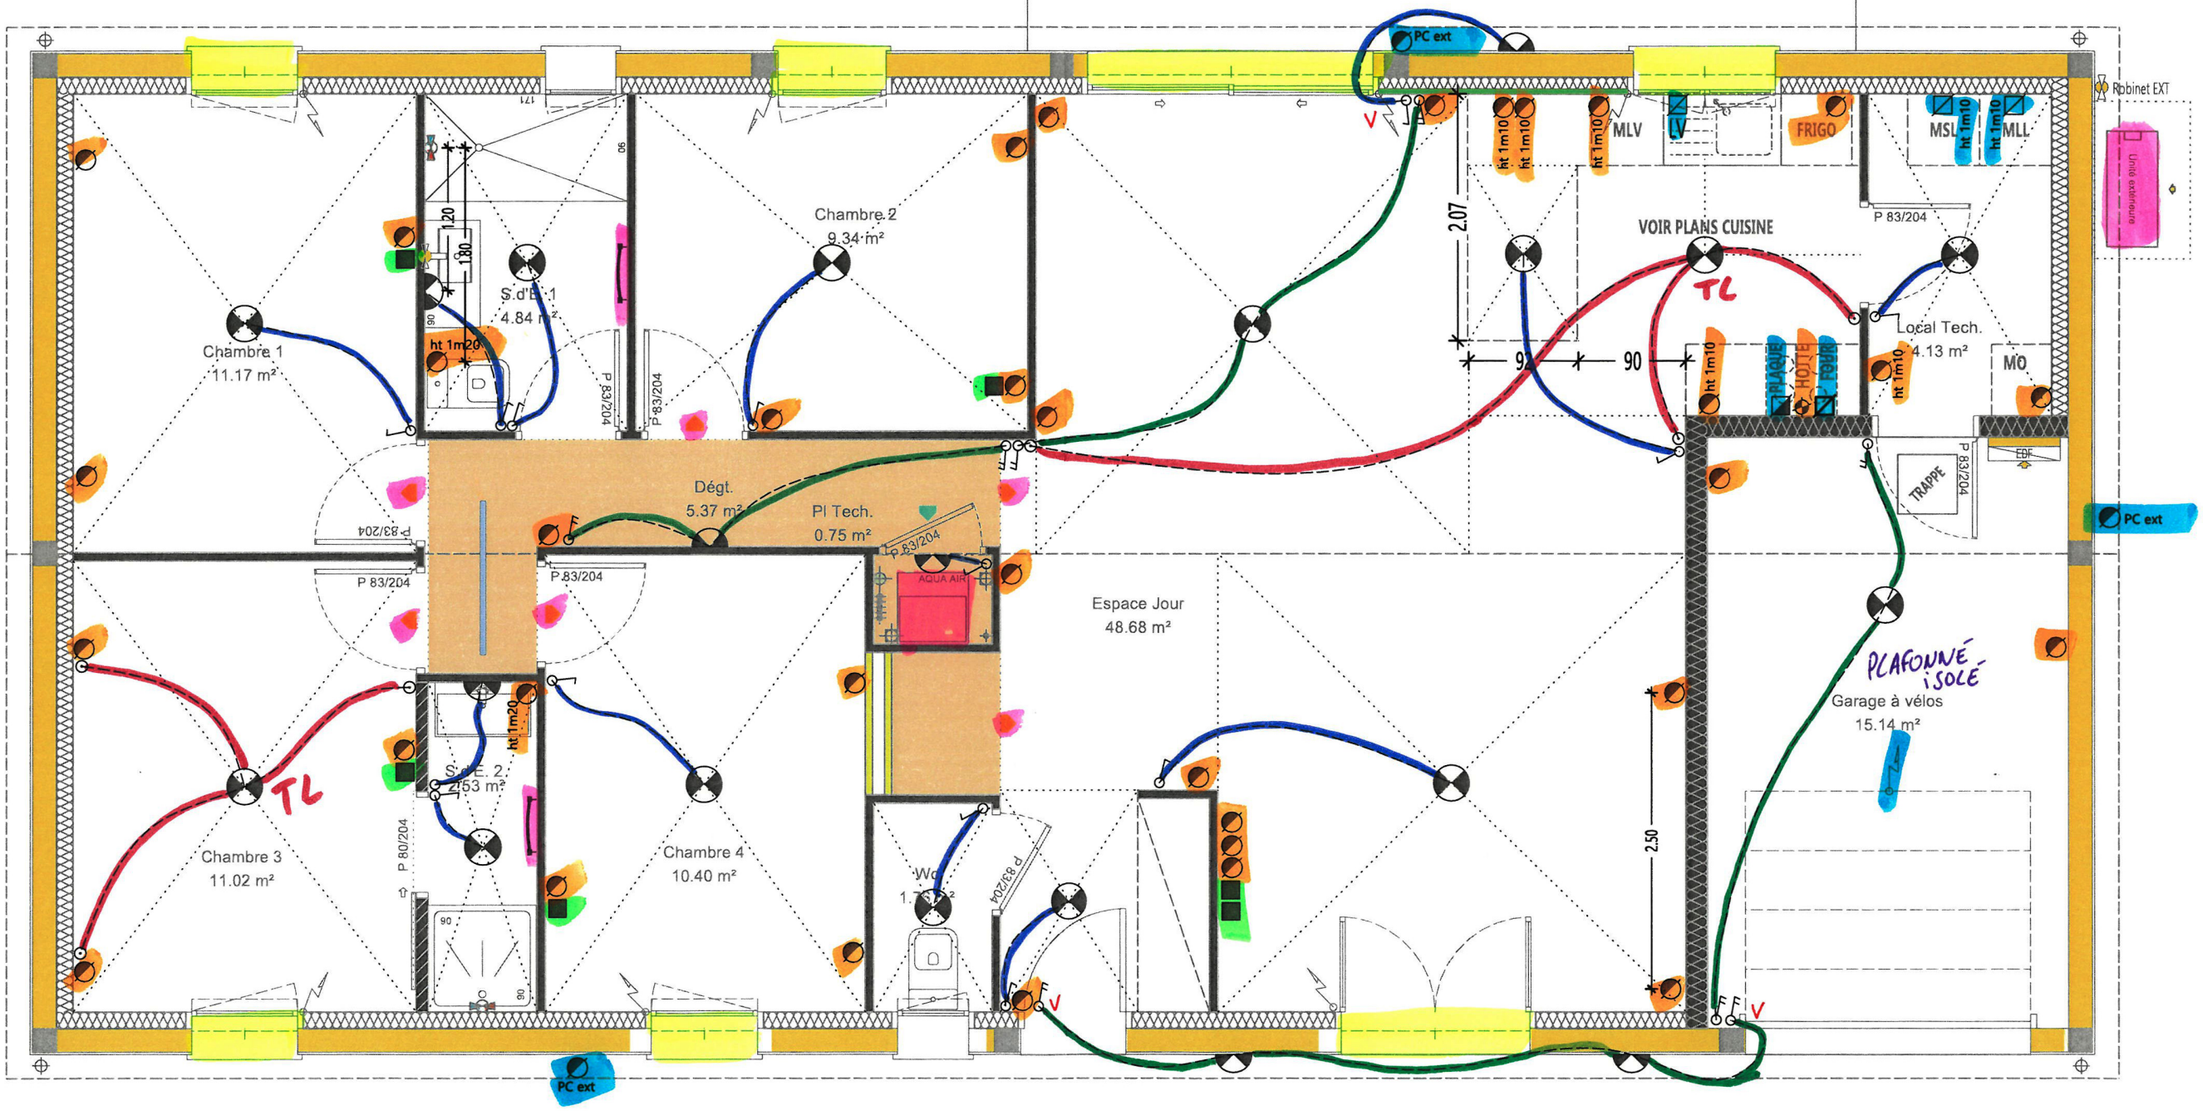

KiTēOHM pour une maison branchée	www.kiteohm.fr	Client	ALPHA CONSTRUCTIONS
		Chantier	FALGUA E6390
		N°	AF26064297

Echelle : 1 / 50
Dess. : s.tarnaud
Date : 06/07/2026

RE 2020 — E6390

CONSTRUCTION D'UNE MAISON INDIVIDUELLE

Maître d'Ouvrage : M. & Mme FALGUA


PLAN ELECTRIQUE RdC

Echelle : 1 / 50 °
Date : 13/04/2026

06.1 / TVX

Adresse Chantier : LOT 1 ROUTE DE JEAN DE L'OUILLE 33390 TALAIS

Les appareillages sont positionnés sur le plan à titre indicatif, ils doivent être installés en fonction des normes en vigueur.
Les hauteurs en cm sont données à titre indicatif, suivre les valeurs indiquées sur le plan .
⚠ Les hauteurs sont données à partir du sol fini ! ⚠

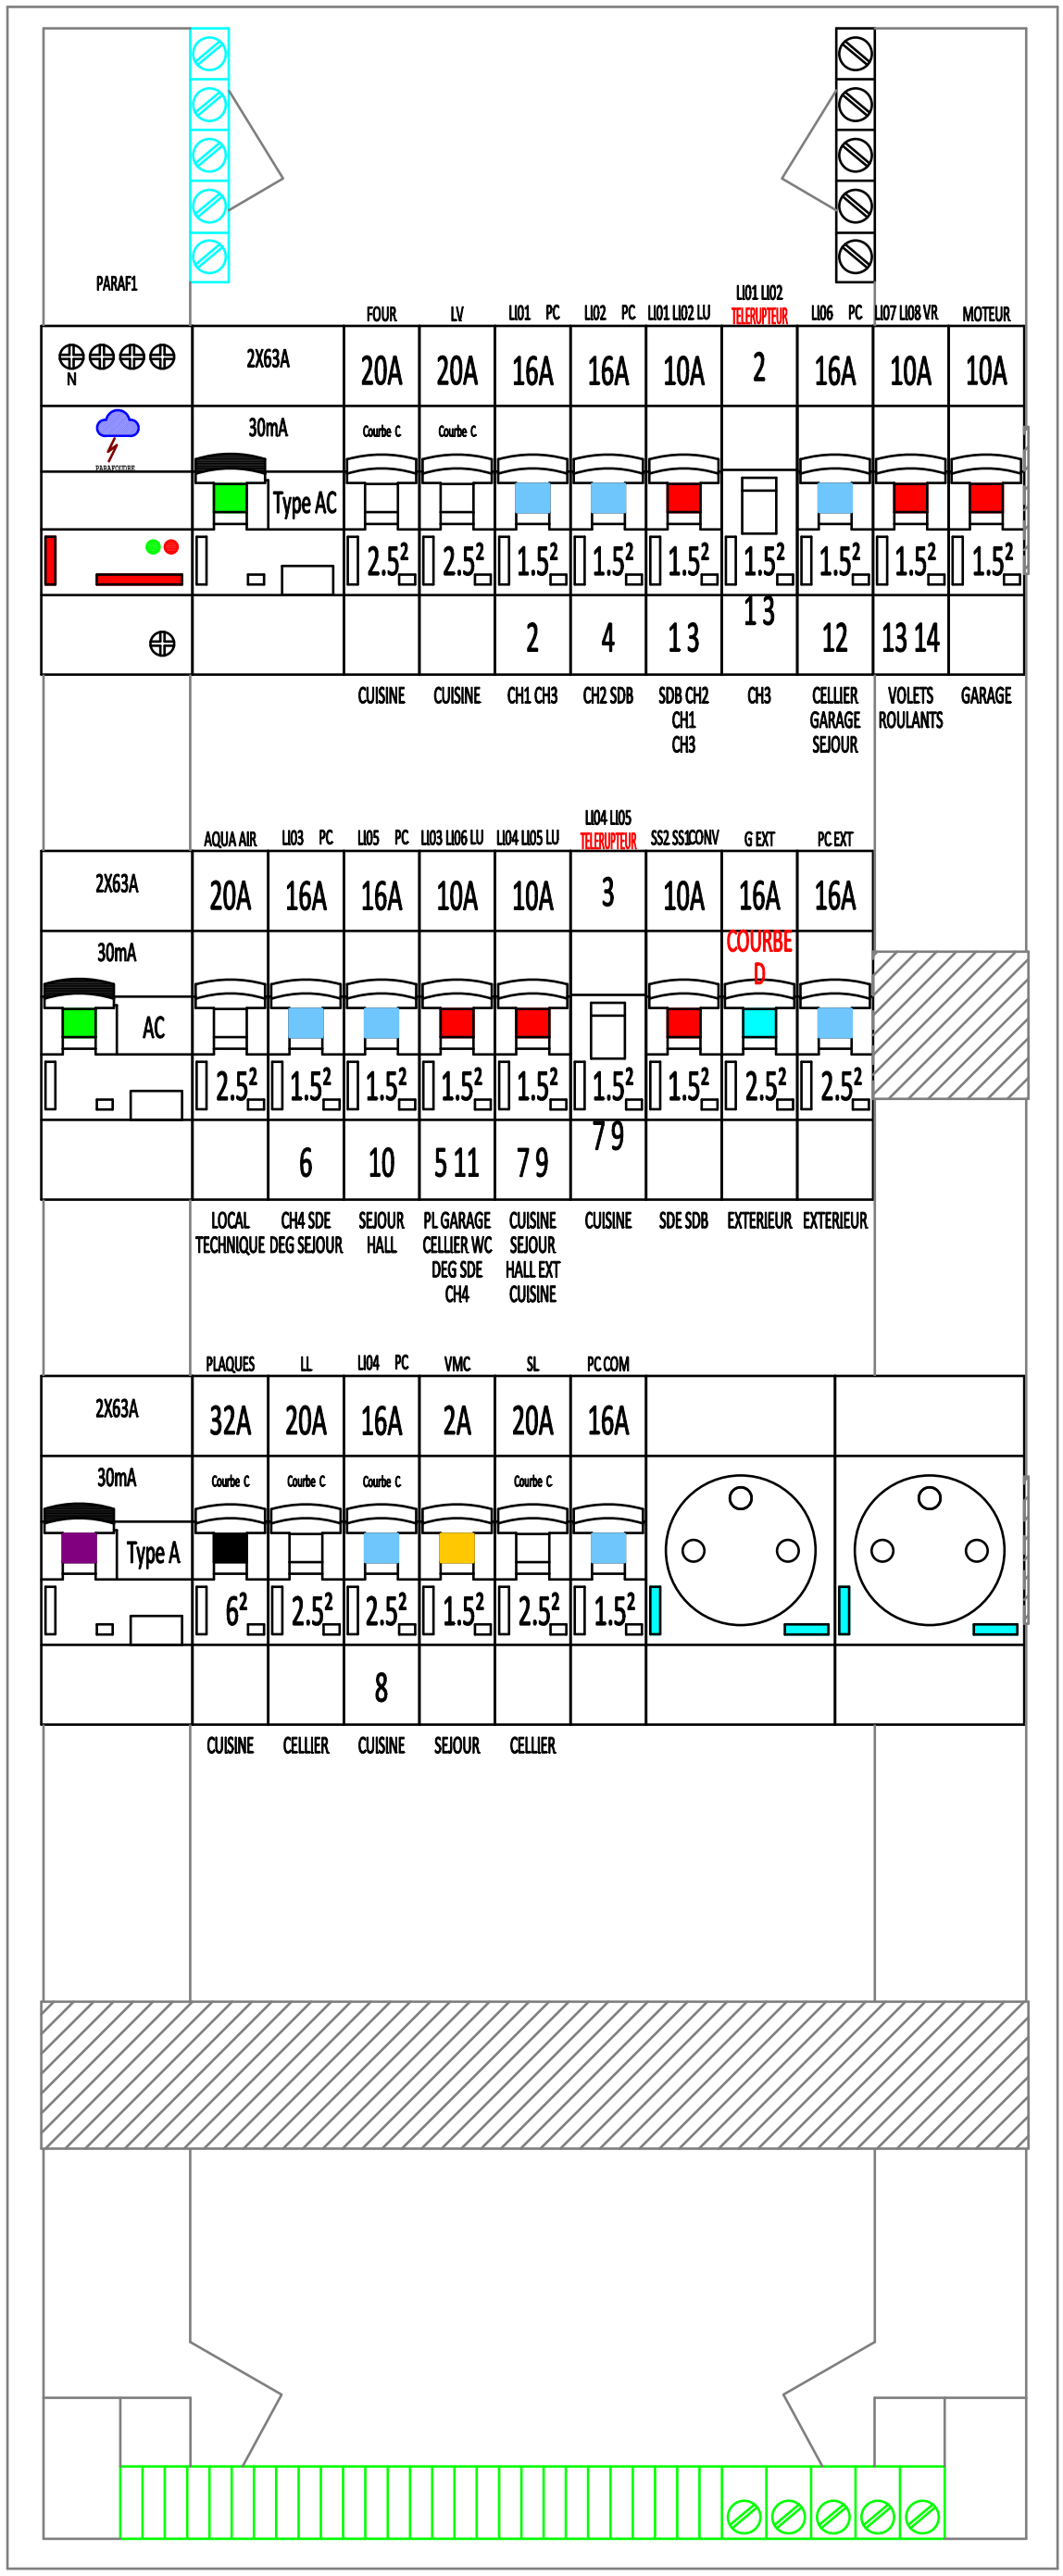

BOUCHON		
16 x16	8 x20	0 x25

TORES
CH ☐ CE ☐ PC ☐

TYPE CHAUFFAGE
AQUA AIR

TYPE ECS

CHAUFFAGE ELECTRIQUE

SS1 : SDB
SS2 : SDE

REPERE	TYPE D'APPAREIL	PIECE DESERVIE
VR1	Cde-C-VR	SEJOUR
VR2	Cde-C-VR	CH4
VR3	Cde-C-VR	CH3
VR4	Cde-C-VR	CH1
VR5	Cde-C-VR	CH2
VR6	Cde-C-VR	SEJOUR
VR7	Cde-C-VR	CUISINE

FOND

KiTēOHM pour une maison branchée

www.kiteohm.fr

Client	ALPHA CONSTRUCTIONS
Chantier	FALGUA E6390
N°	AF26064297

Echelle : 1 / 1.6
Dess : s.tarnaud
Date : 07/07/2026

PROG TABLEAU/CHANTIER		
CONNECTEURS / WAGOS		0
SCHNEIDER		13 MODULES
		MONOPHASE X
GTL	X	TRIPHASE
PORTE	X	FOND
BORNIER DE TERRE SUP		

ALPHA CONSTRUCTIONS
FALGUA E6390
AF26064297

Nb MODULES:

PORTE
REF : Porte 4*13M

CONTACTEUR CE NBRE:

BOUCHON	x16	x20	x25
DMT AVEC WAGGOS			
DMT SANS WAGGOS			
MONOPHASE			
TRIPHASE			
DISJONCTEUR REF :			

TORES
CH ☐ CE ☐ PC ☐

TYPE CHAUFFAGE

TYPE ECS

REPERE	TYPE D'APPAREIL	PIECE DESERVIE

