

MAISON 1

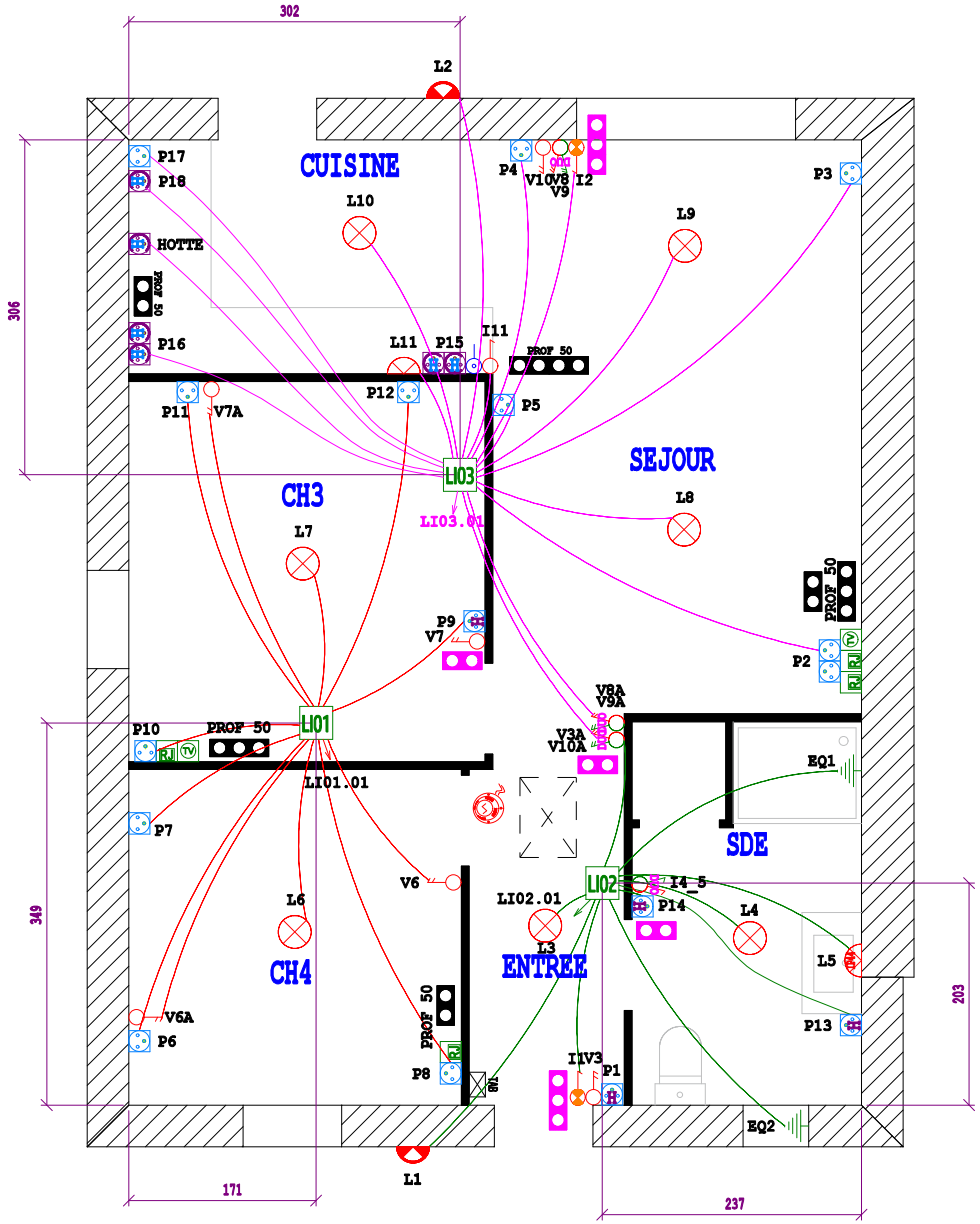



	Boite pavillonnaire
	Détecteur de fumée
	Interrupteur double allumage
	Interrupteur double Va-et-Vient
	Interrupteur simple allumage
	Interrupteur simple allumage lumineux
	Interrupteur Va-et-Vient
	Plaque double Horizontale
	Plaque double Verticale
	Plaque quadruple Horizontale
	Plaque triple Horizontale
	Plaque triple Verticale
	Applique étanche
	Applique murale salle de bain
	Applique murale
	Point lumineux
	Prise de courant 2.5² H1.20m
	Prise de courant Hotte
	Renvoi de tableau
	Liaison équipotentielle

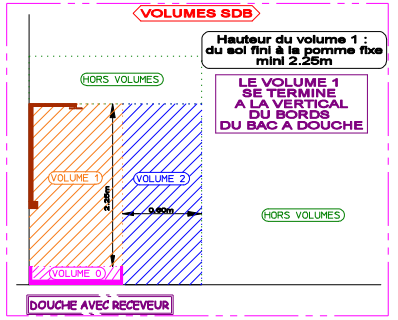

ATTENTION DANS SDB L'APP ELEC DOIT ETRE A PLUS 1.80M DU MITIGEUR (DOUCHE DE PLAIN-PIED) ET A PLUS 60CM DU BORD DE LA BAIGNOIRE OU D'UN BAC A DOUCHE OU CLOISONNER LE CHAUFFE-EAU AVEC UNE PORTE LA PRISE ELLE DOIT ETRE HORS VOLUME


Les appareillages sont positionnés sur le plan à titre indicatif, ils doivent être installés en fonction des normes en vigueur.
Les hauteurs en cm sont données à titre indicatif, suivre les valeurs indiquées sur le plan .
⚠ Les hauteurs sont données à partir du sol fini ! ⚠

KiTéOHM pour une maison branchée


www.kiteohm.fr

Client	POLYGONE 46 (POLYGONE46)	Echelle :	1 / 50
Chantier	FONTES D2129 MAISON 1	Dess :	NC
N°	AF25124651	Date:	15/09/2026

MAISON 1

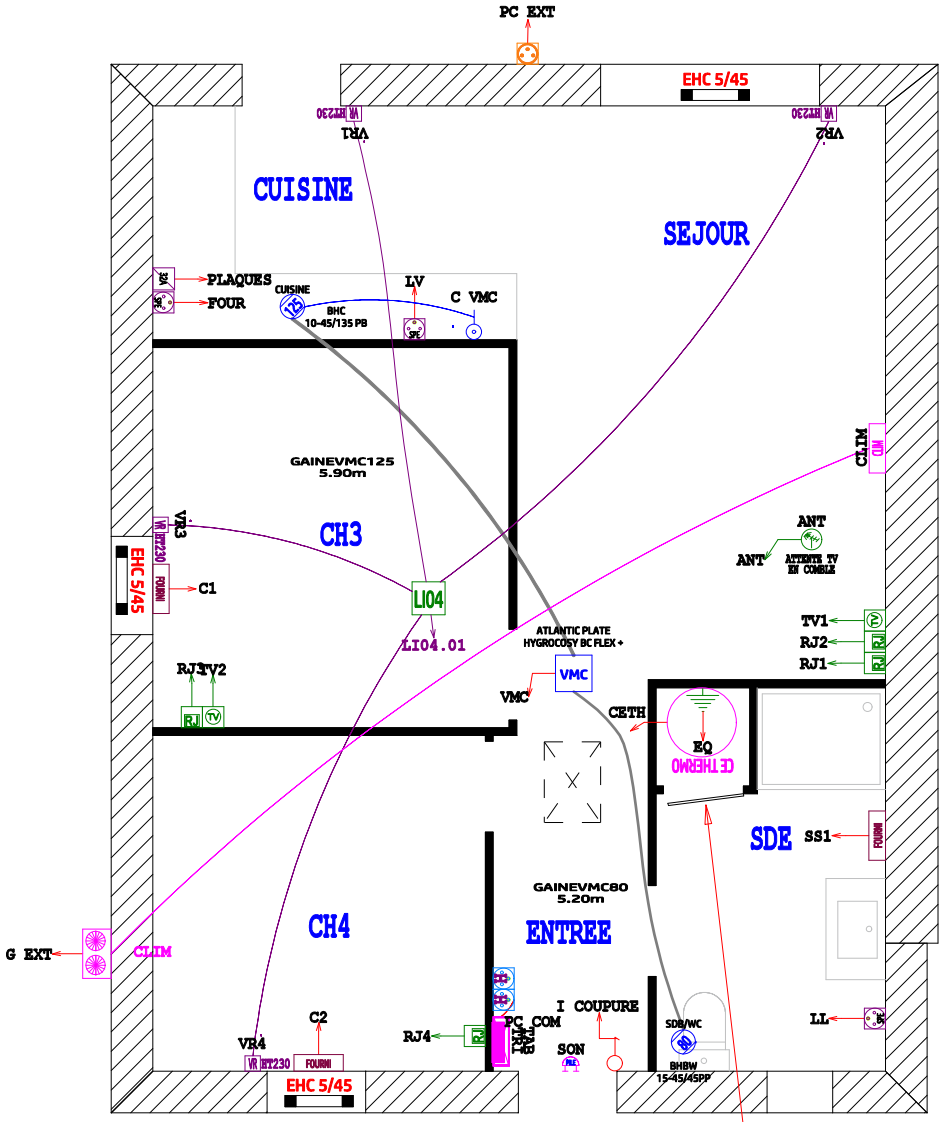

CE THERMO	Boite pavillonnaire
	Chauffe-eau électrique thermodynamique
CLIM	Climatisation
FOURNI	Convecteur de chauffage rayonnant
	Pompe à chaleur unité extérieur
FOURNI	Sèche serviette
ATTENTE TV EN COMBLE	Antenne TV H comble
RJ	Prise RJ45 H0.30m (PMR H0.40m)
TV	Prise télévision H0.30m (PMR H0.40m)
32A	Sortie de cable 32A
	Commande VMC
	Interrupteur simple allumage
	Prise de courant étanche ext H0.30m (PMR H0.40m)
SPE	Prise de courant spécialisée H0.30m (PMR H0.40m)
	Carillon sans fil
	Tableau d'alimentation générale basse tension
	Tableau de communication
	Prise de terre
VR BT230	Obturateur

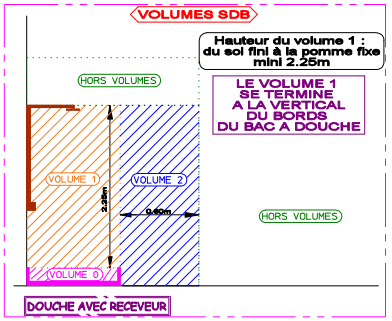



ATTENTION DANS SDB L'APP ELEC DOIT ETRE
A PLUS 1.80M DU MITIGEUR (DOUCHE DE PLAIN-PIED)
ET A PLUS 60CM DU BORD DE LA BAIGNOIRE OU D'UN BAC A DOUCHE
OU CLOISONNER LE CHAUFFE-EAU AVEC UNE PORTE
LA PRISE ELLE DOIT ETRE HORS VOLUME

KIT BOUCHONS ATLANTIC


Les appareillages sont positionnés sur le plan à titre indicatif, ils doivent être installés en fonction des normes en vigueur.
Les hauteurs en cm sont données à titre indicatif, suivre les valeurs indiquées sur le plan .
⚠ Les hauteurs sont données à partir du sol fini ! ⚠

KiTēOHM pour une maison branchée


www.kiteohm.fr

Client	POLYGONE 46 (POLYGONE46)	Echelle :	1 / 50
Chantier	FONTES D2129 MAISON 1	Dess :	NC
N°	AF25124651	Date:	11/09/2026

Pour les 2 logements, déplacement de la prise extérieure entre la BV et la porte cuisine.

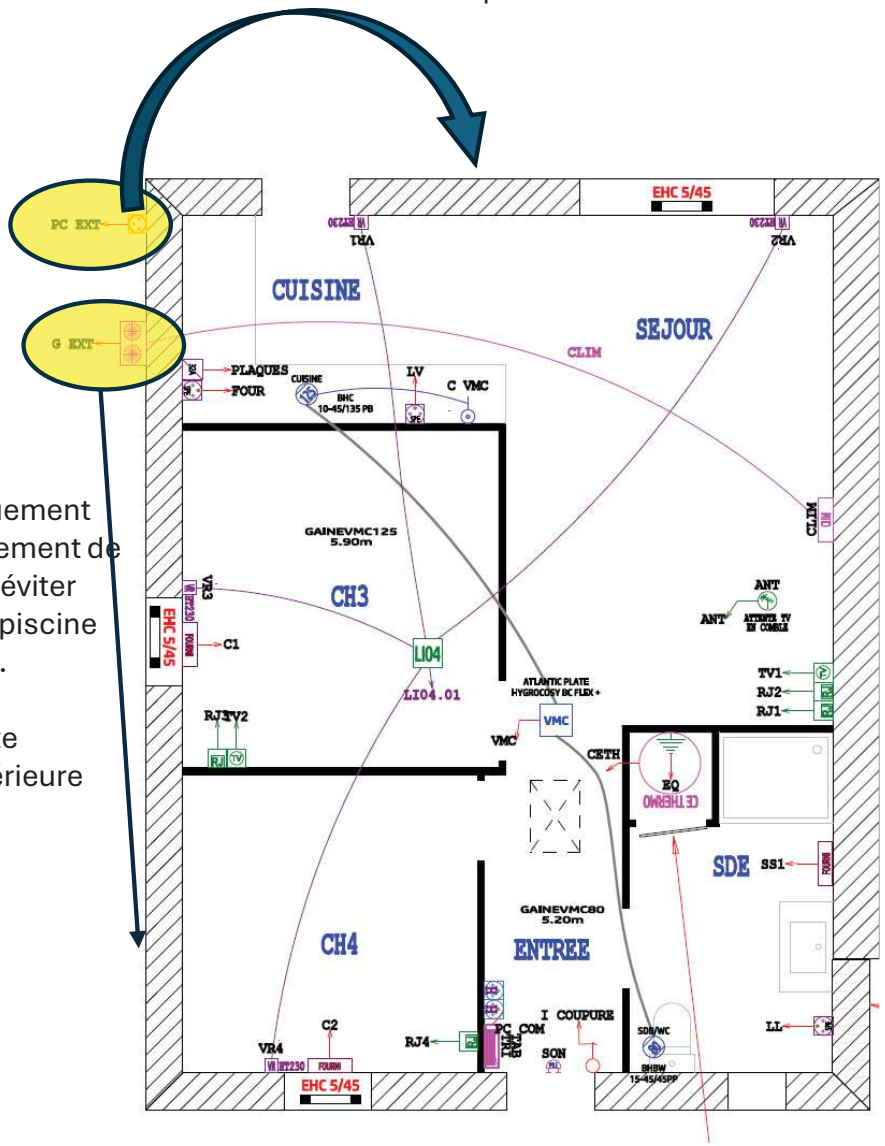


Pour 1 logement uniquement (logement Est) déplacement de l'unité extérieure pour éviter qu'elle soit à 5m de la piscine et terrasse des voisins.
Pour le 2nd logement (logement Ouest), cette position de l'unité extérieure est OK.

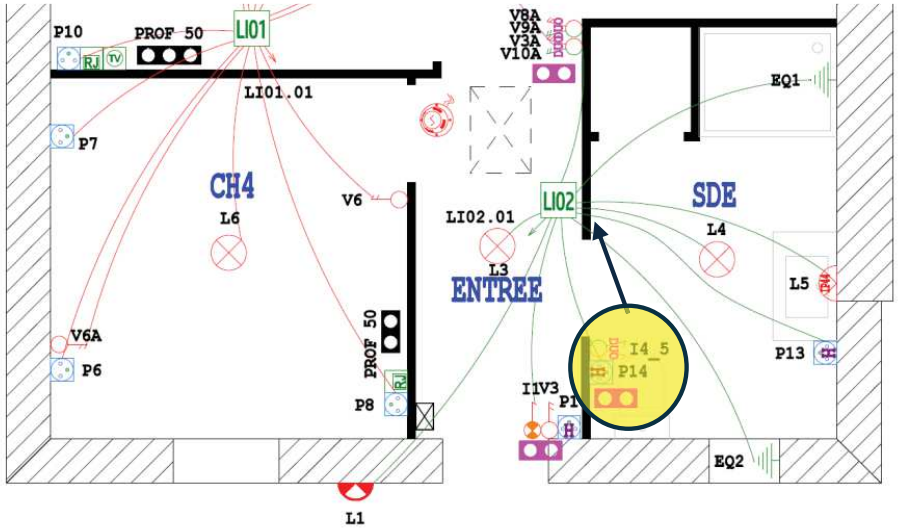


Pour les 2 logements, déplacement des interrupteurs et prise du coté de l'ouverture de la porte (jusqu'à maintenant impossible à cause du sèche serviette, mais qui est à présent possible grâce au déplacement du sèche serviette entre vasque et douche).

- Prise 20 A
- Prise 32A
- Interrupteur
- Point de centre DCL D54

Electricité cuisine ① maison **Est**

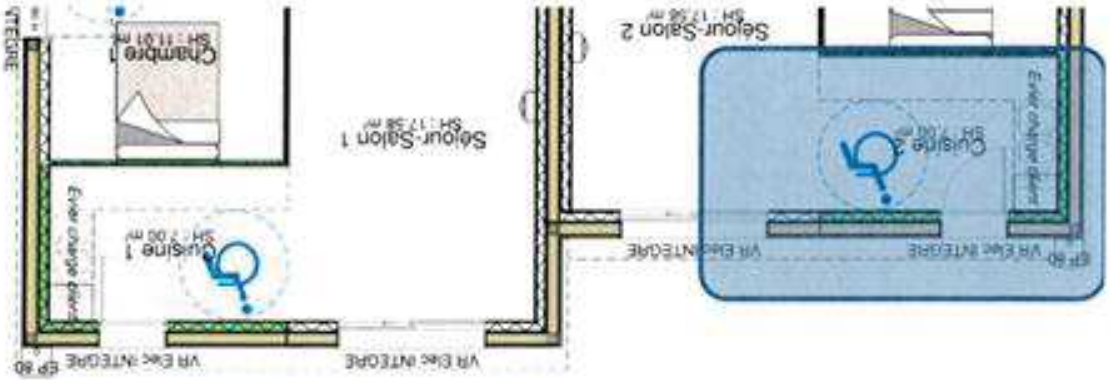



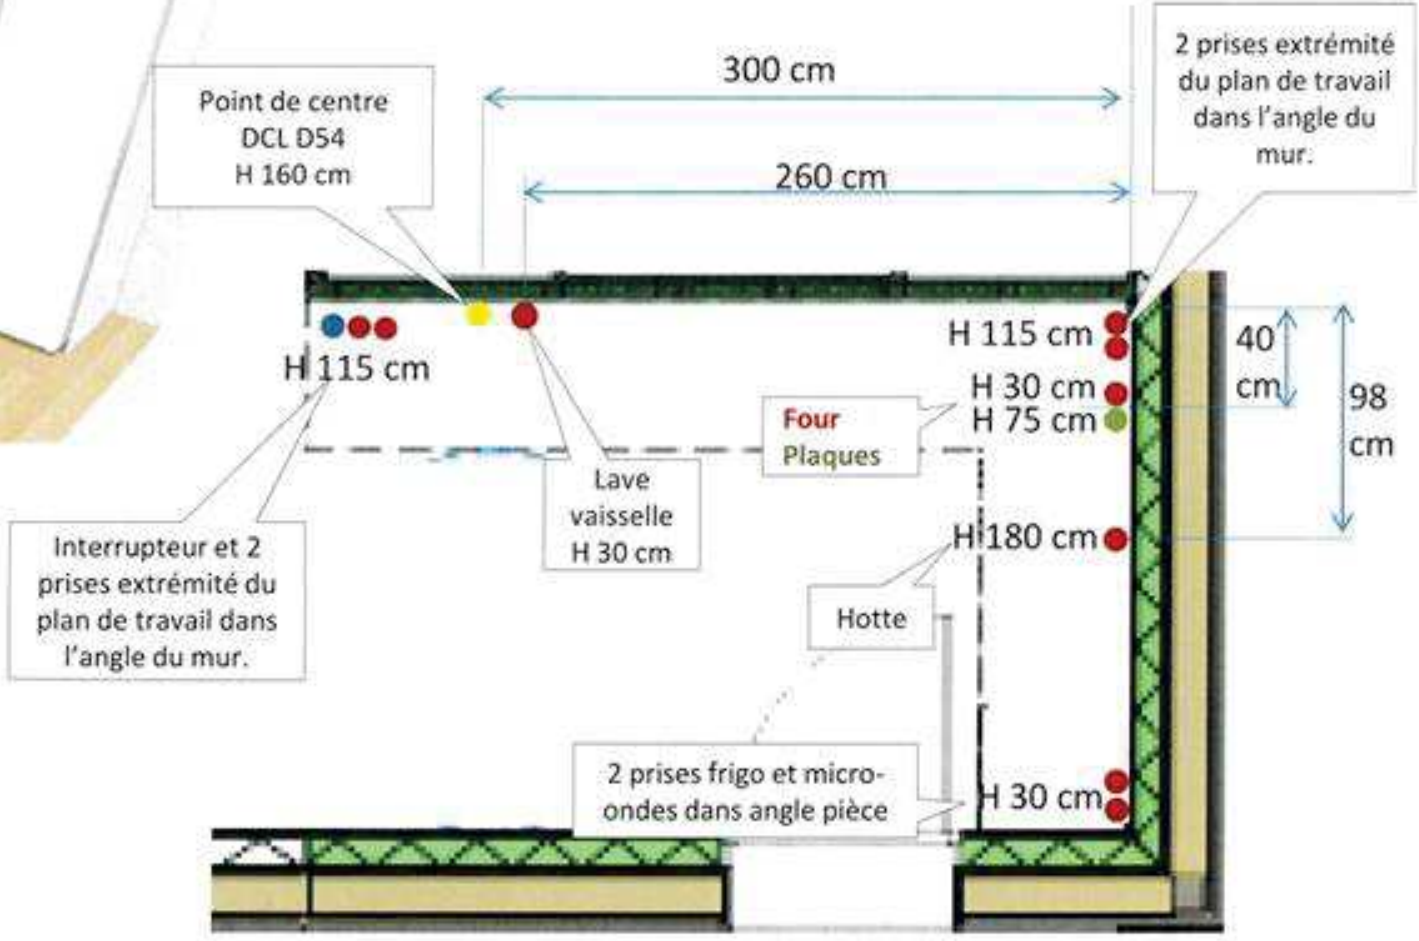

Toutes les hauteurs (H) par rapport au sol fini


Prise 20 A


Prise 32A


Interrupteur


Point de centre DCL D54

Electricité cuisine ② maison **Ouest**

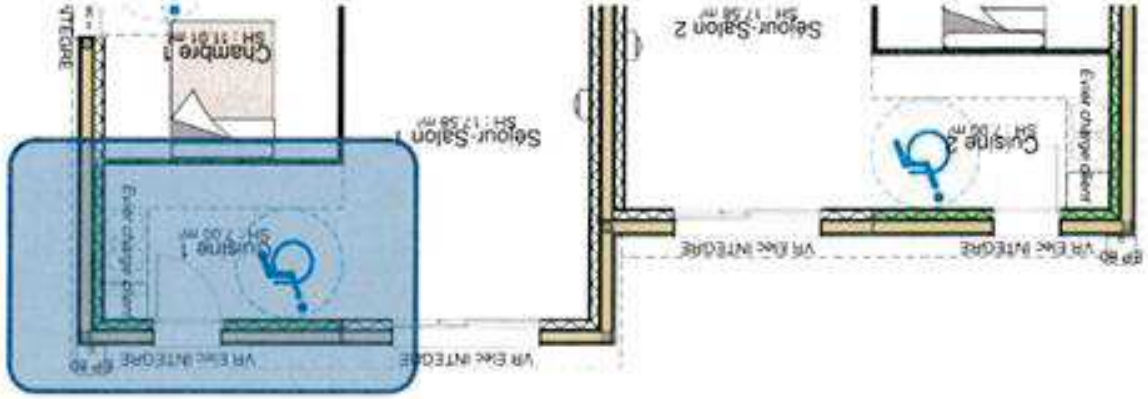

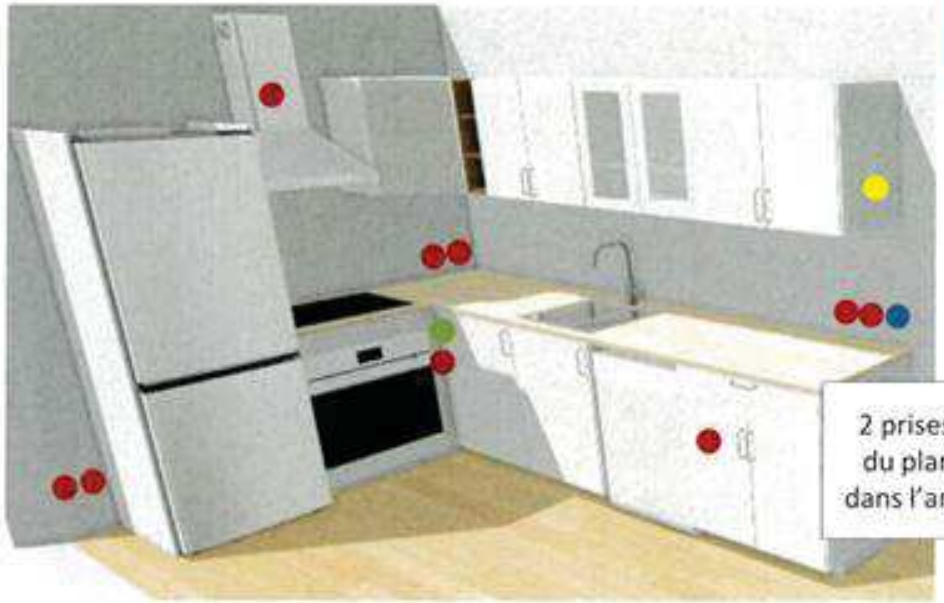

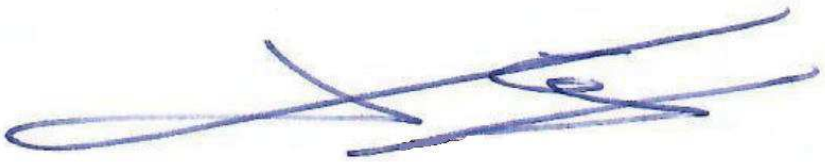

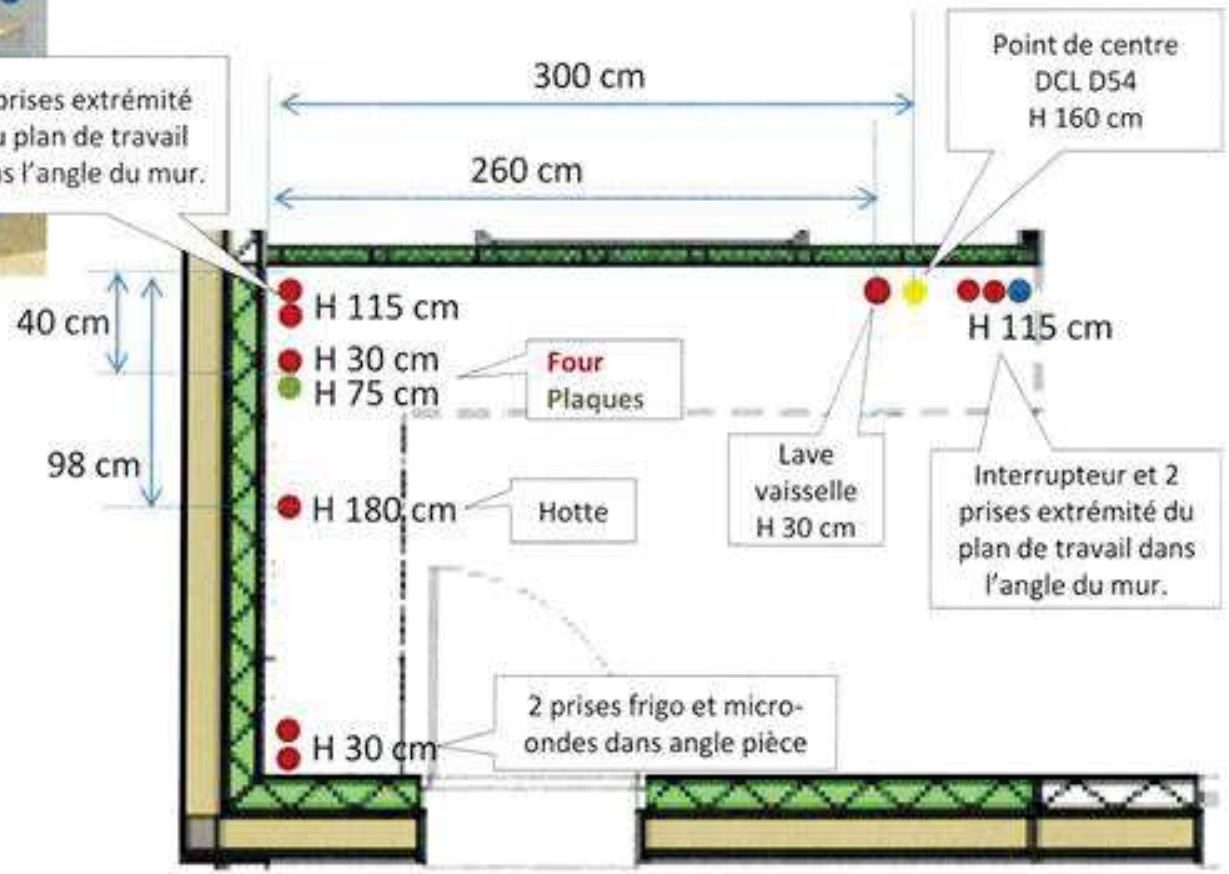

Toutes les hauteurs (H) par rapport au sol fini